



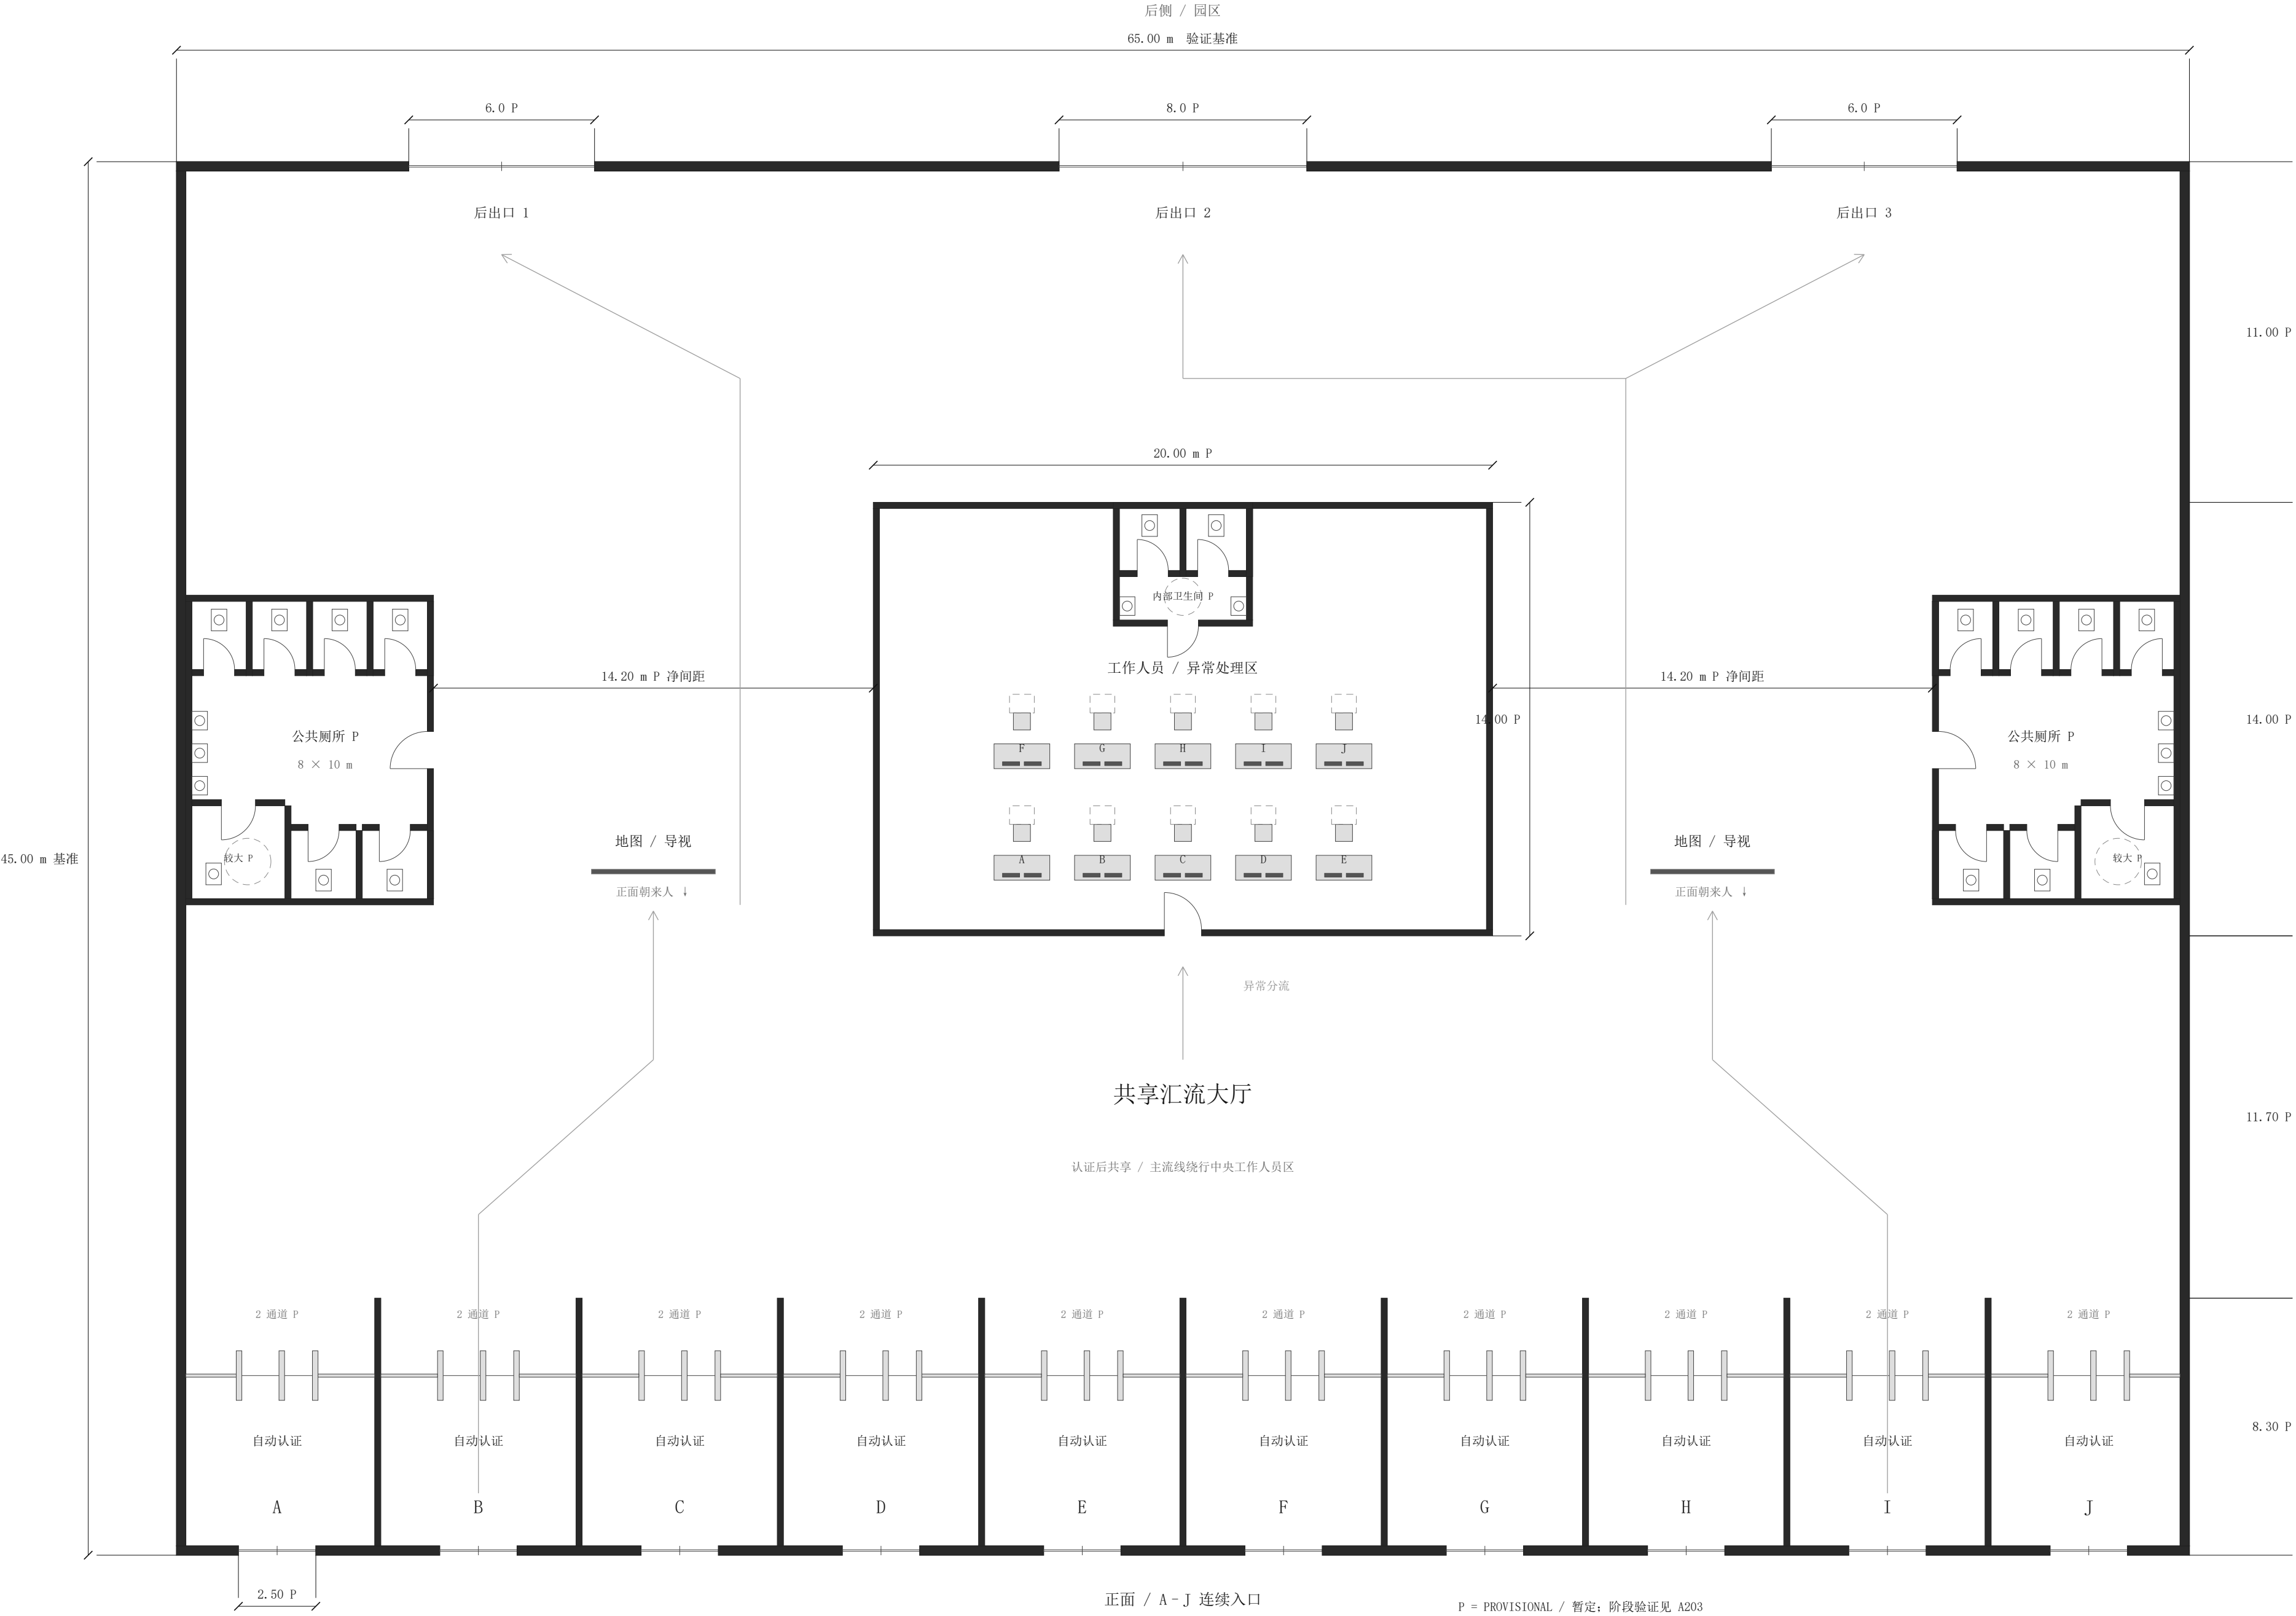

01 工作人员 / 异常处理区

边界 20×14 m P；内部布局 P | 1:100

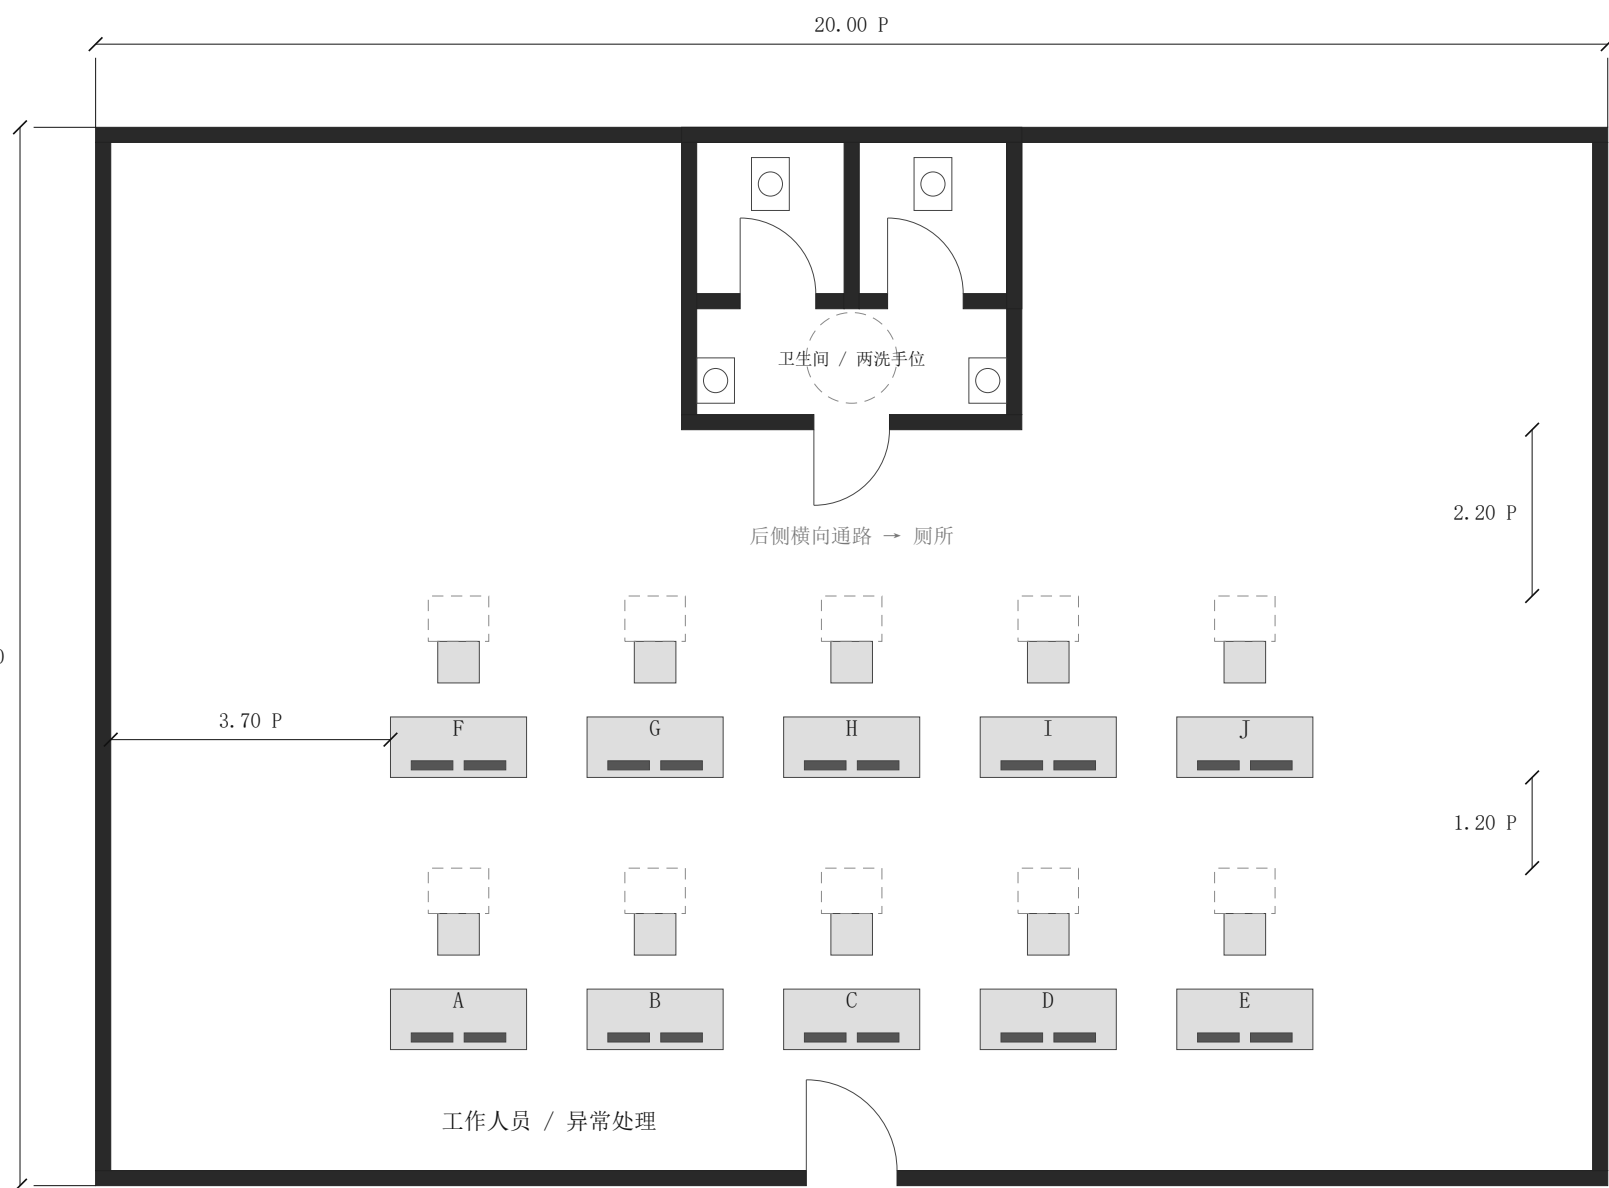

十工位 A-J，双屏，2排×5；桌面1.80×0.80 m P。


椅后另留0.60 m（虚线）；排间/厕所前净1.20/2.20 m。

侧通路3.70 m；前侧入门→侧通路→后横路→厕所。

卫生间4.5×4 m；2间净1.95×2 m、2洗手位；转身测试通过。

02 左公共厕所（右侧镜像）

外包 8×10 m P | 1:75

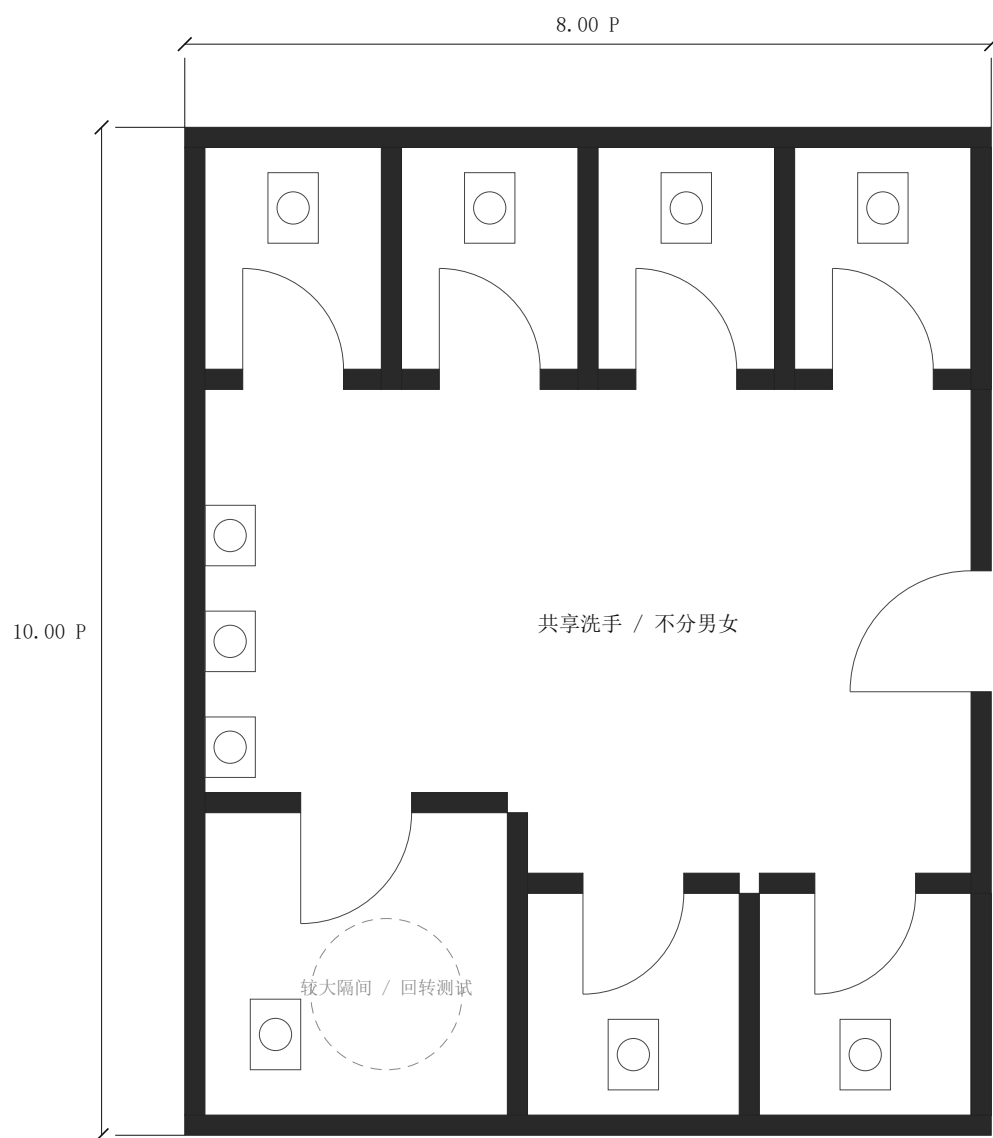


两排：6普通 + 1较大隔间 / 侧（P）

普通净1.75/2.10×2.20；较大3×3 m。

全封闭独立隔间；洗手区共享。

03 入口 A / 认证组

其余B-J同组重复 | 1:75

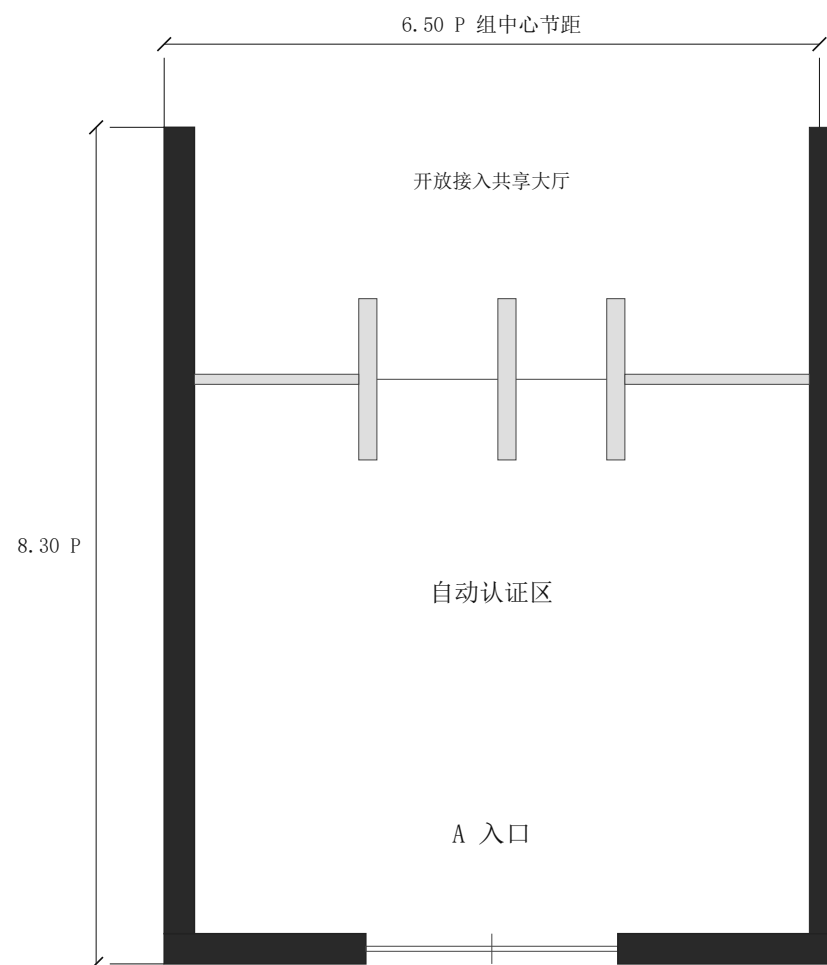

前开口 2.50 m；2条认证通道 P。

净宽1.20 / 0.90；设备长1.60 m。

闸机设备组总宽2.64 m P。

本轮设计阶段暂定值（P / PROVISIONAL）

外墙0.30 m；隔墙0.20 m；公共厕所入口1.20 m；较大隔间门1.10 m；普通隔间门1.00 m。

工作人员内部厕所门1.00 m；门扇、洁具、工作台与地图均为可测量的简化占位。

边界与尺寸均使用同一建筑坐标；局部放大保留主图坐标关系。

较宽门、低/无门槛及辅助设施预留为通用设计意图；本轮只做平面空间验证。

已确认 / 当前验证基准

单层：十入口→认证→共享大厅→两侧地图→三后出口；工作人员区有十个双屏工位。

外包65×45 m保留本阶段基准；工作人员区20×14 m与卫生间4.5×4 m均为P。

本轮 PROVISIONAL 参数

墙 / 门 外墙0.30；隔墙0.20；前开口2.50；后开口6 / 8 / 6 m；门型及开启P。

定位 工作人员X=22.50，Y=20.00；两公共厕所Y=21.00 m，均以外边界定位。

工作人员 厕所4.5×4 m，后墙居中；2独立隔间+2洗手位；10工位2×5；桌1.80×0.80；纵向节距3.60 m。

公共厕所 每侧外包8×10 m；两排6普通+1较大；普通净1.75/2.10×2.20；较大净3.00×3.00 m。

认证组 每组2通道，净宽1.20 / 0.90；条宽0.18、长1.60；前端Y=5.00；净深8.00 m。

通路 / 导视 椅后另留0.60；排间/厕所前1.20/2.20；侧路3.70；地图4×0.15 m，朝前，两旁≥5.10 m。

面积 / 参数修改

外包面积2925 m²；工作人员边界280 m²（含内部厕所18 m²）；两公共厕所合计160 m²。

各分区数字为方案边界面积，包含其墙体；不代表净使用面积或容纳人数。

FreeCAD Parameters内长度/XY直接驱动草图和A204；ParameterTable列出状态与单位。

出版页为快照；用build_freecad.py --parameters-from 已修改文件.FCStd重建，再运行GUI宏与PDF导出。

本阶段空间验证结果

工作人员区与卫生间适配；十工位、2独立隔间、2洗手位、转身测试及连续通路通过。

公共厕所两排独立隔间、共享洗手；门扇/洁具/洗手区无冲突；地图与三出口流线保持。

本阶段空间设计收工；不继续消防、结构、机电或法规深化。P为当前方案测试值。

后续仅保留吞吐验证；到场率、认证时长、失败分流比例、出口流率及停留时间待输入。

依据：FINAL_PASS优先于旧分区/厕所内容；CRYO_FACILITY_LAYOUT / REDRAW_BRIEF其余关系保持。