


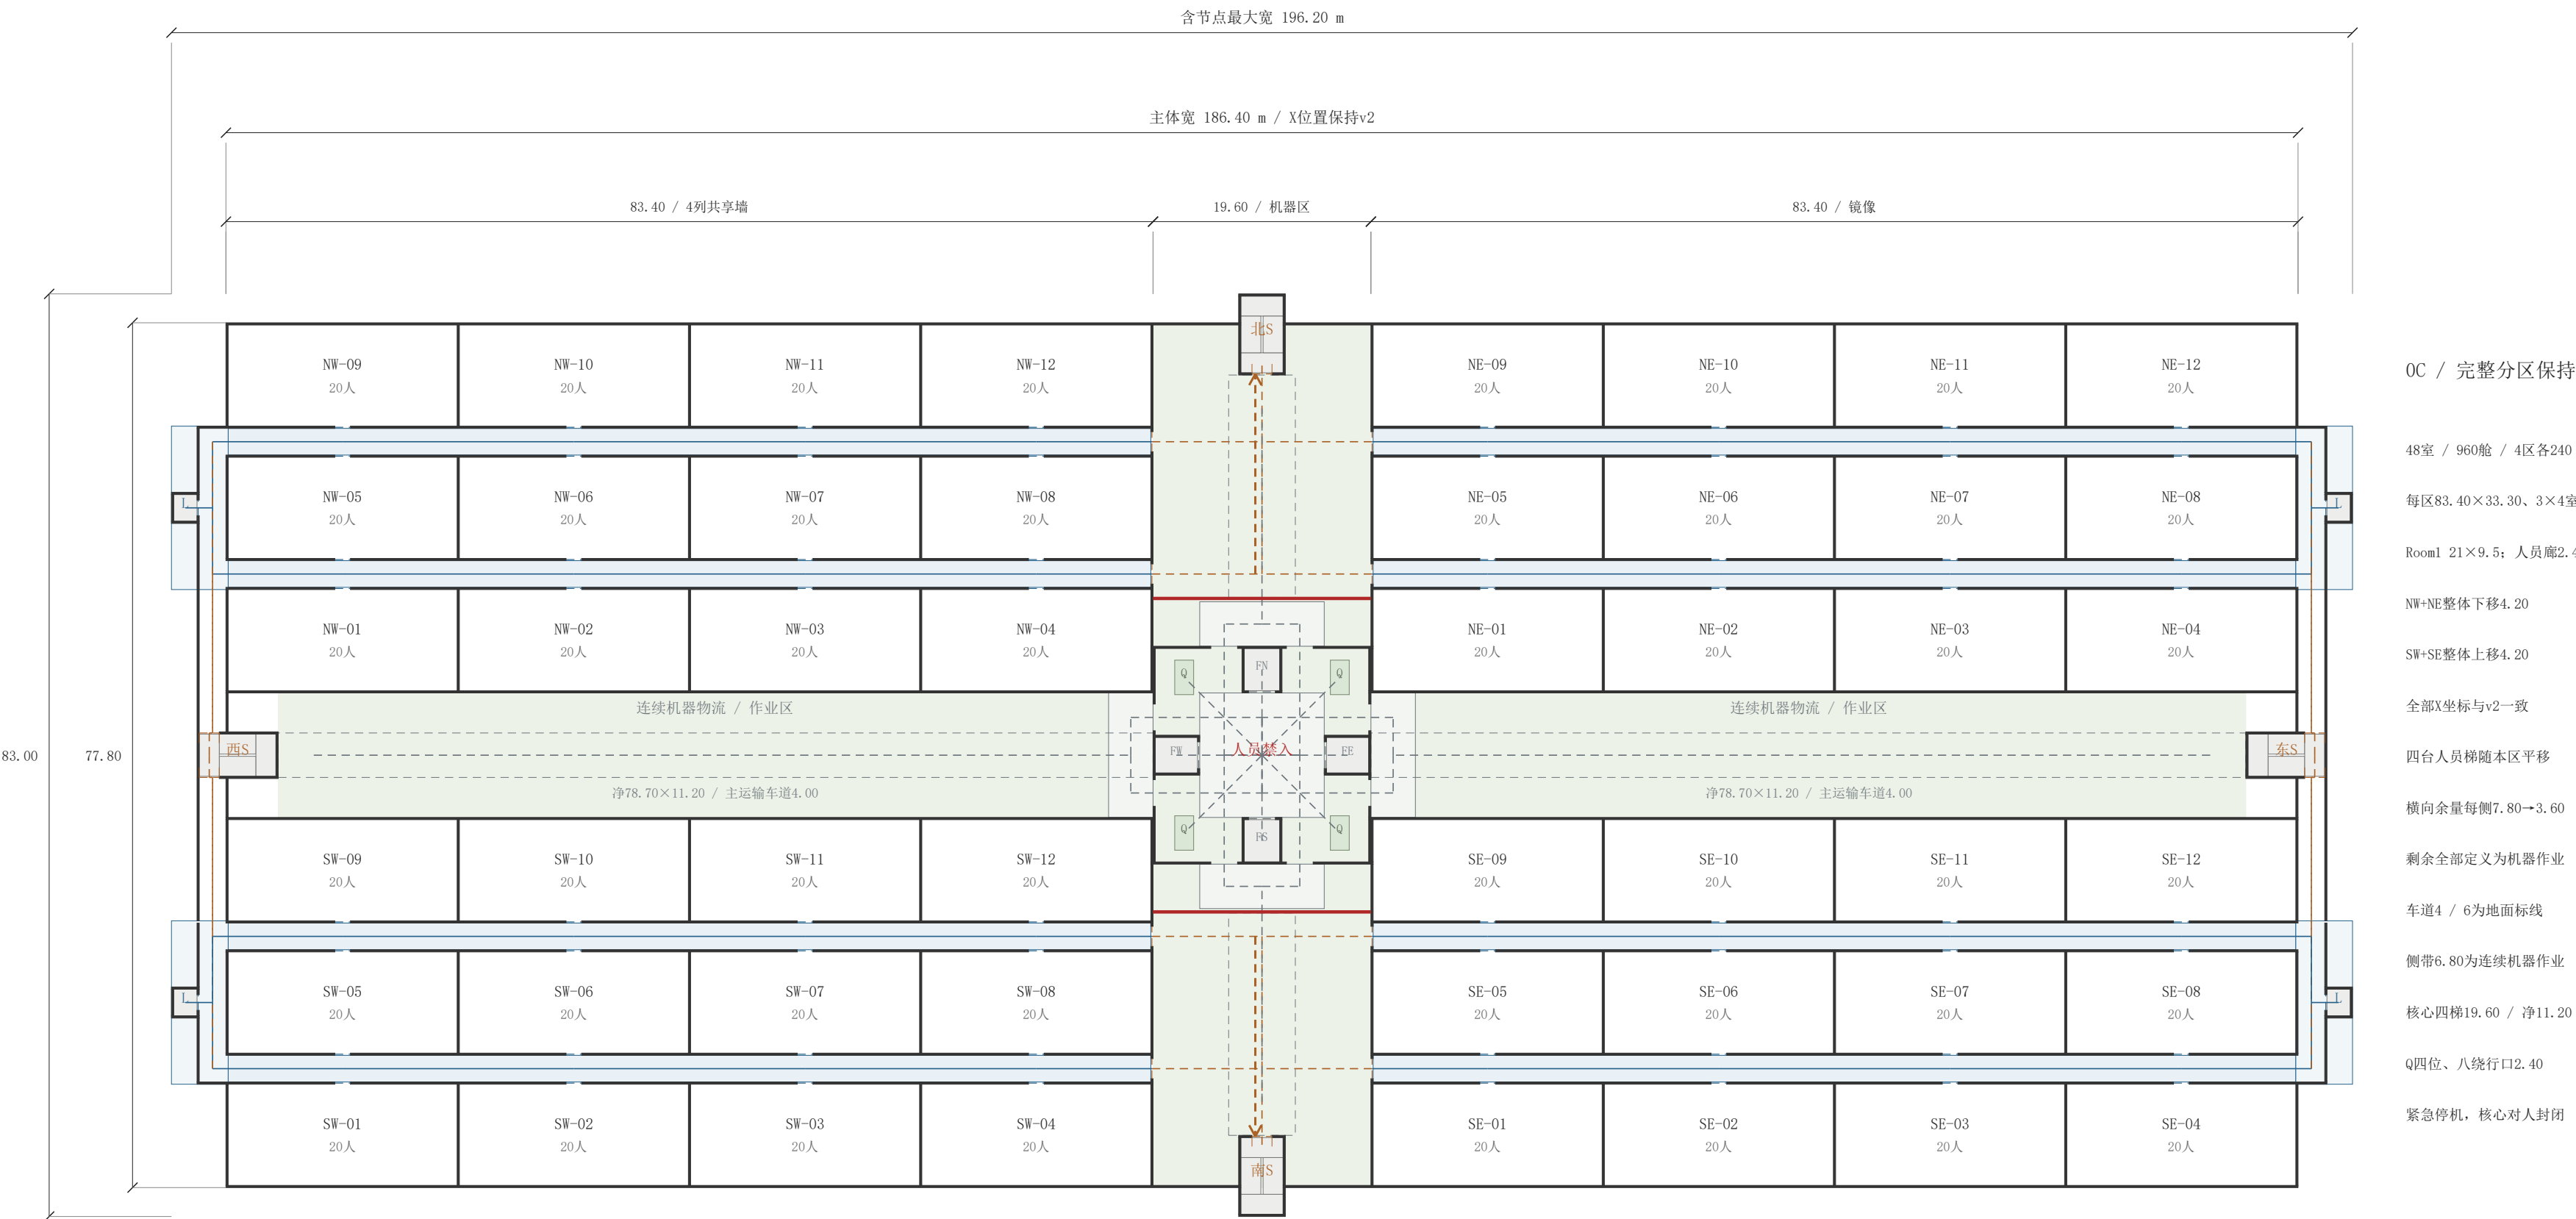

OC / 完整分区保持

48室 / 960舱 / 4区各240

每区83.40×33.30、3×4室

Room1 21×9.5; 人员廊2.4

NW+NE整体下移4.20

SW+SE整体上移4.20

全部X坐标与v2一致

四台人员梯随本区平移

横向余量每侧7.80→3.60

剩余全部定义为机器作业

车道4 / 6为地面标线

侧带6.80为连续机器作业

核心四梯19.60 / 净11.20

Q四位、八绕行口2.40

紧急停机，核心对人封闭

- 日常人员 / 本区外侧电梯
- 应急人员 / 四向楼梯、核心禁入
- 机器物流 / 四向绕行入中央核心

浅绿：连续机器作业地面 / 4m、6m为主车道


人员：日常走外侧L；紧急可沿纵段向外S

红线：整个19.60m纵段应急隔离，禁止绕入核心

最远中心 → 最近楼梯 66.95 m；舱侧保守 77.70 m。

最远房SW-02（另SE-03 / NW-10 / NE-11同值）；全部48室均有外侧及北/南两种疏散方向。

已验几何与路线：960人疏散容量/时间、消防隔断构造、门扇扫掠仍待详设。仅2D，无正式3D。

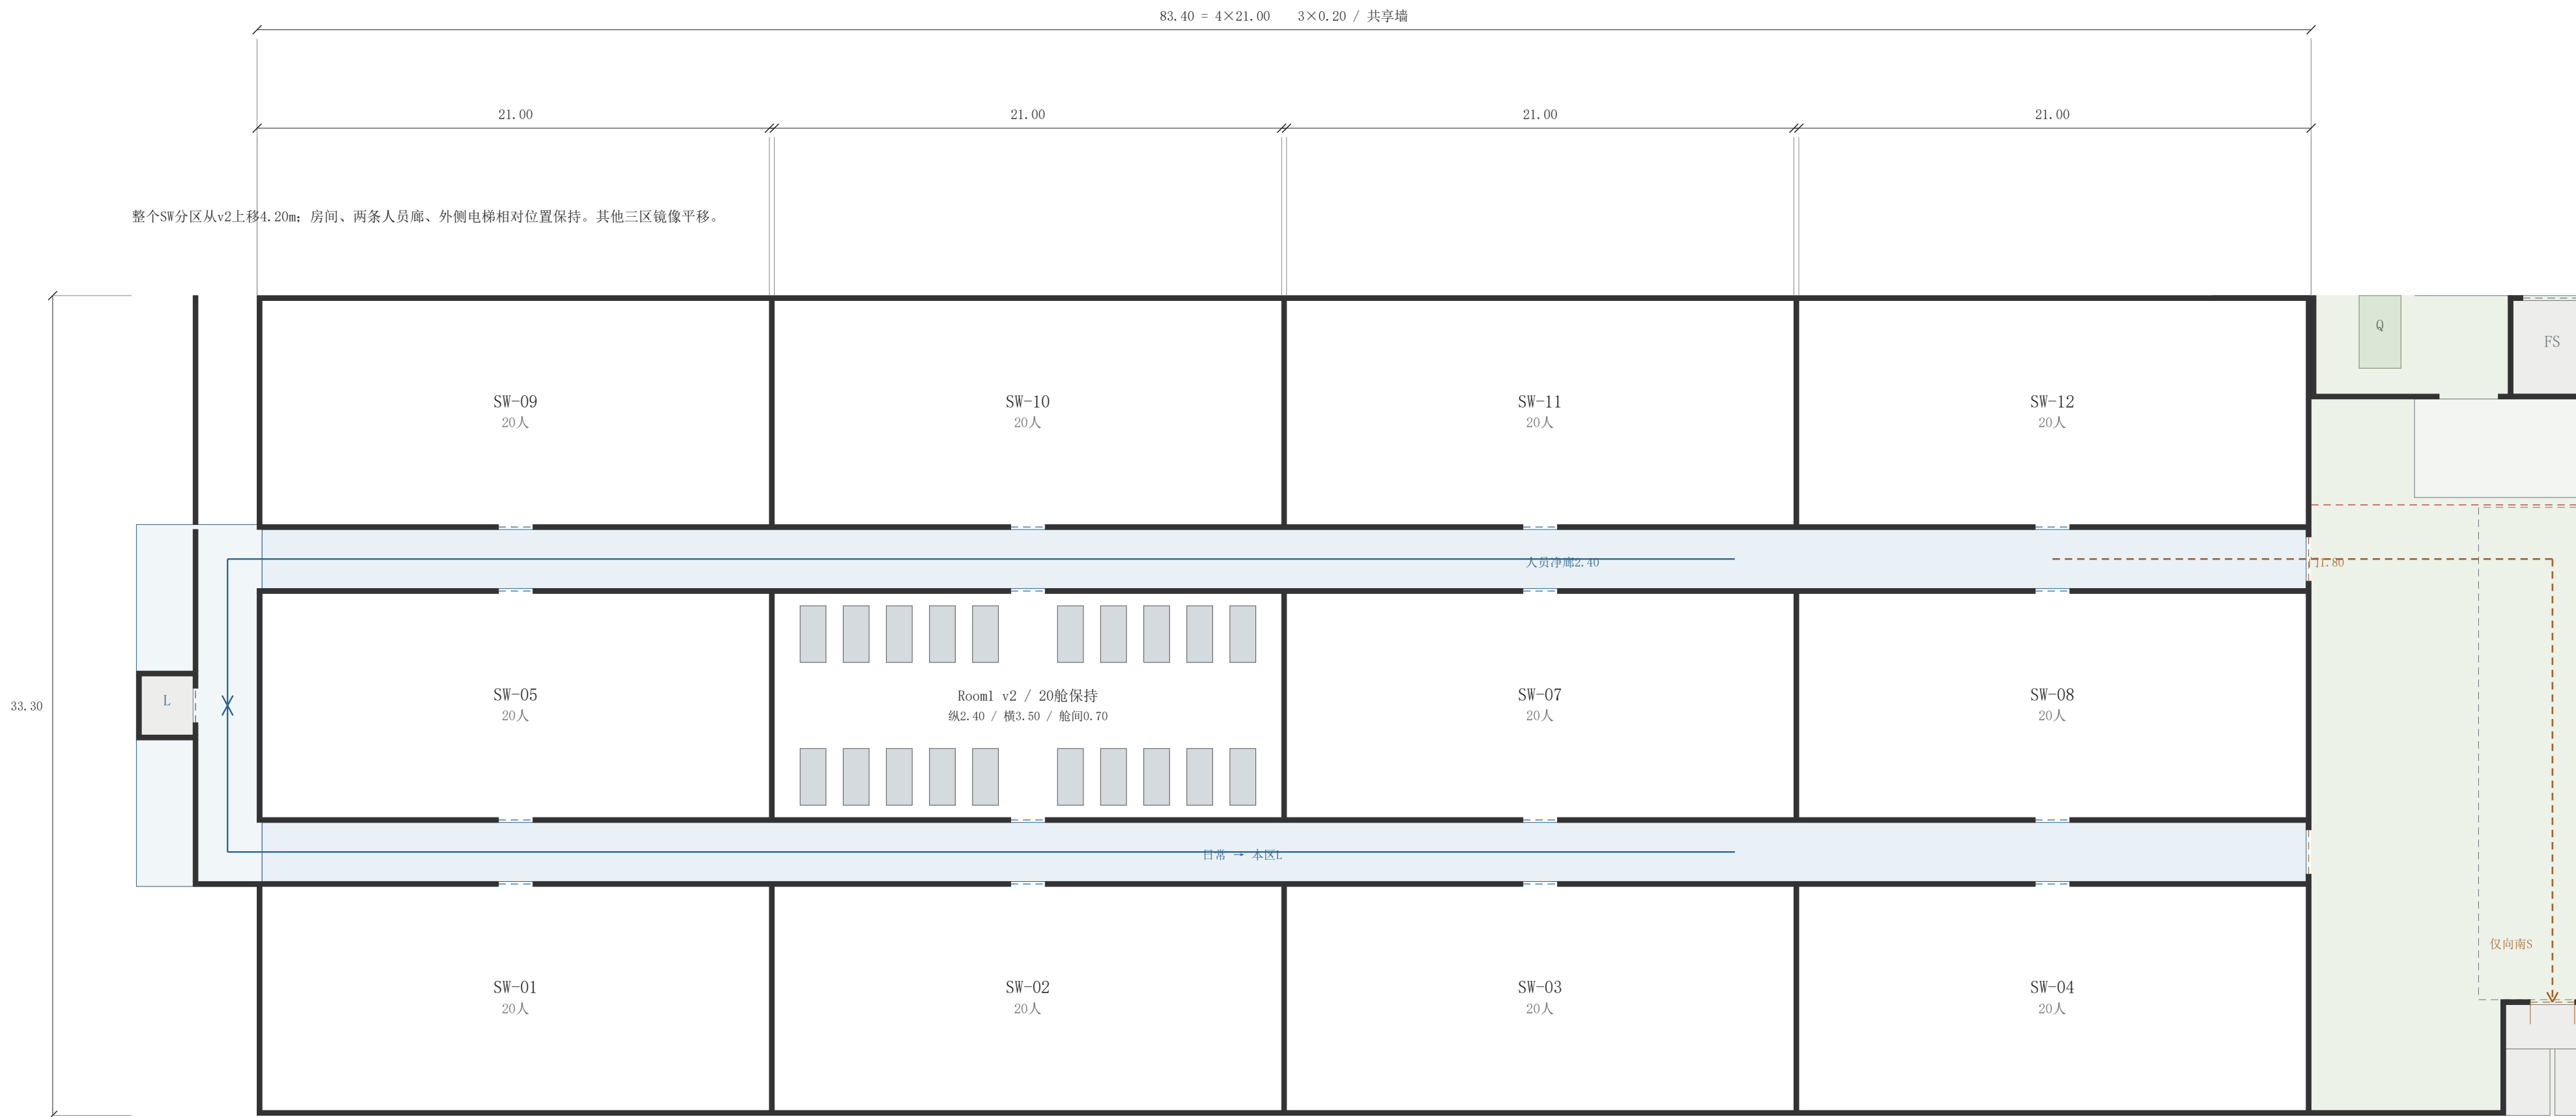

01 原点与平移: SW (0, 0) → (0, 4.20); SE (103, 0) → (103, 4.20)。

02 NW (0, 52.90) → (0, 48.70); NE (103, 52.90) → (103, 48.70)。未移动任何单间。


03 下区北边界37.50 / 上区南边界48.70; 二者间净11.20成为连续机器作业地面。

04 中央主车道4.00、边侧操作带各3.60; 沿线没有额外墙把车道切成喇叭口。

05 相邻舱室共墙0.20; 所有房间内部净20.60×9.10。中排双门; 外排单门, 门净1.40。

06 紧急开启内端门: 机器停运, 南段只向南楼梯; 核心全宽隔离。日常不走中央机器区。

01 北段 / 北楼梯（南侧镜像）

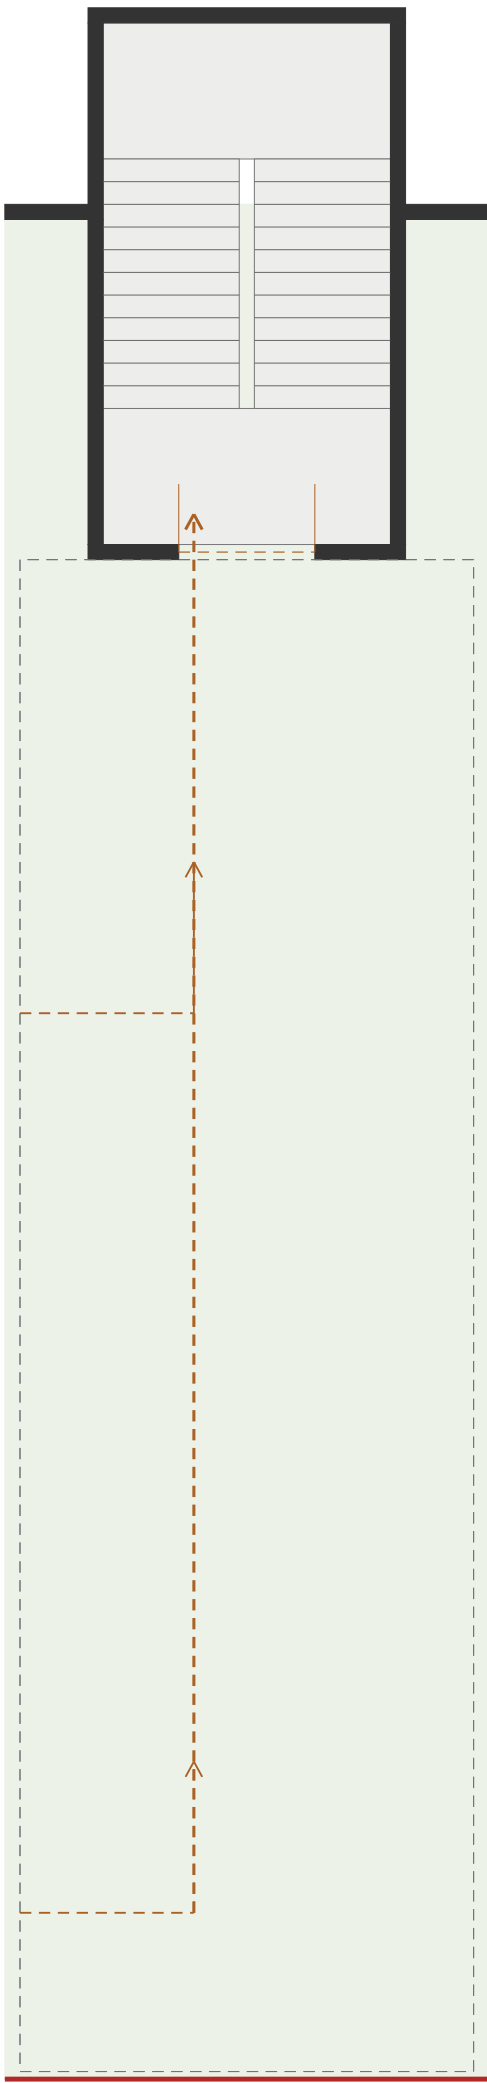

单门1.80，直入平台

北梯4.20×7.30 P

净梯段1.80 / 平台1.80

内嵌4.70 / 外伸2.60

24级 / 158.33mm级高

南北主车道地面净6.00


两侧各6.80机器作业

紧急：纵段全区停机

隔离线横跨整个19.60

人员只向外，不进核心

02 西/东楼梯：保持两门直入

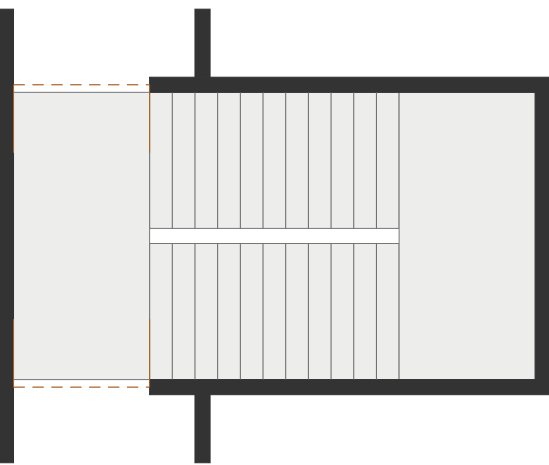

7.30×4.20；上/下各门1.80。


无第三门、无额外前室；东侧镜像。

红线是应急对人隔离边界。

需落实消防隔断构造与停机联锁。

图示门扇仅示意，扫描仍待验证。

03 原位保留四货梯与Q / 连续机器作业地面

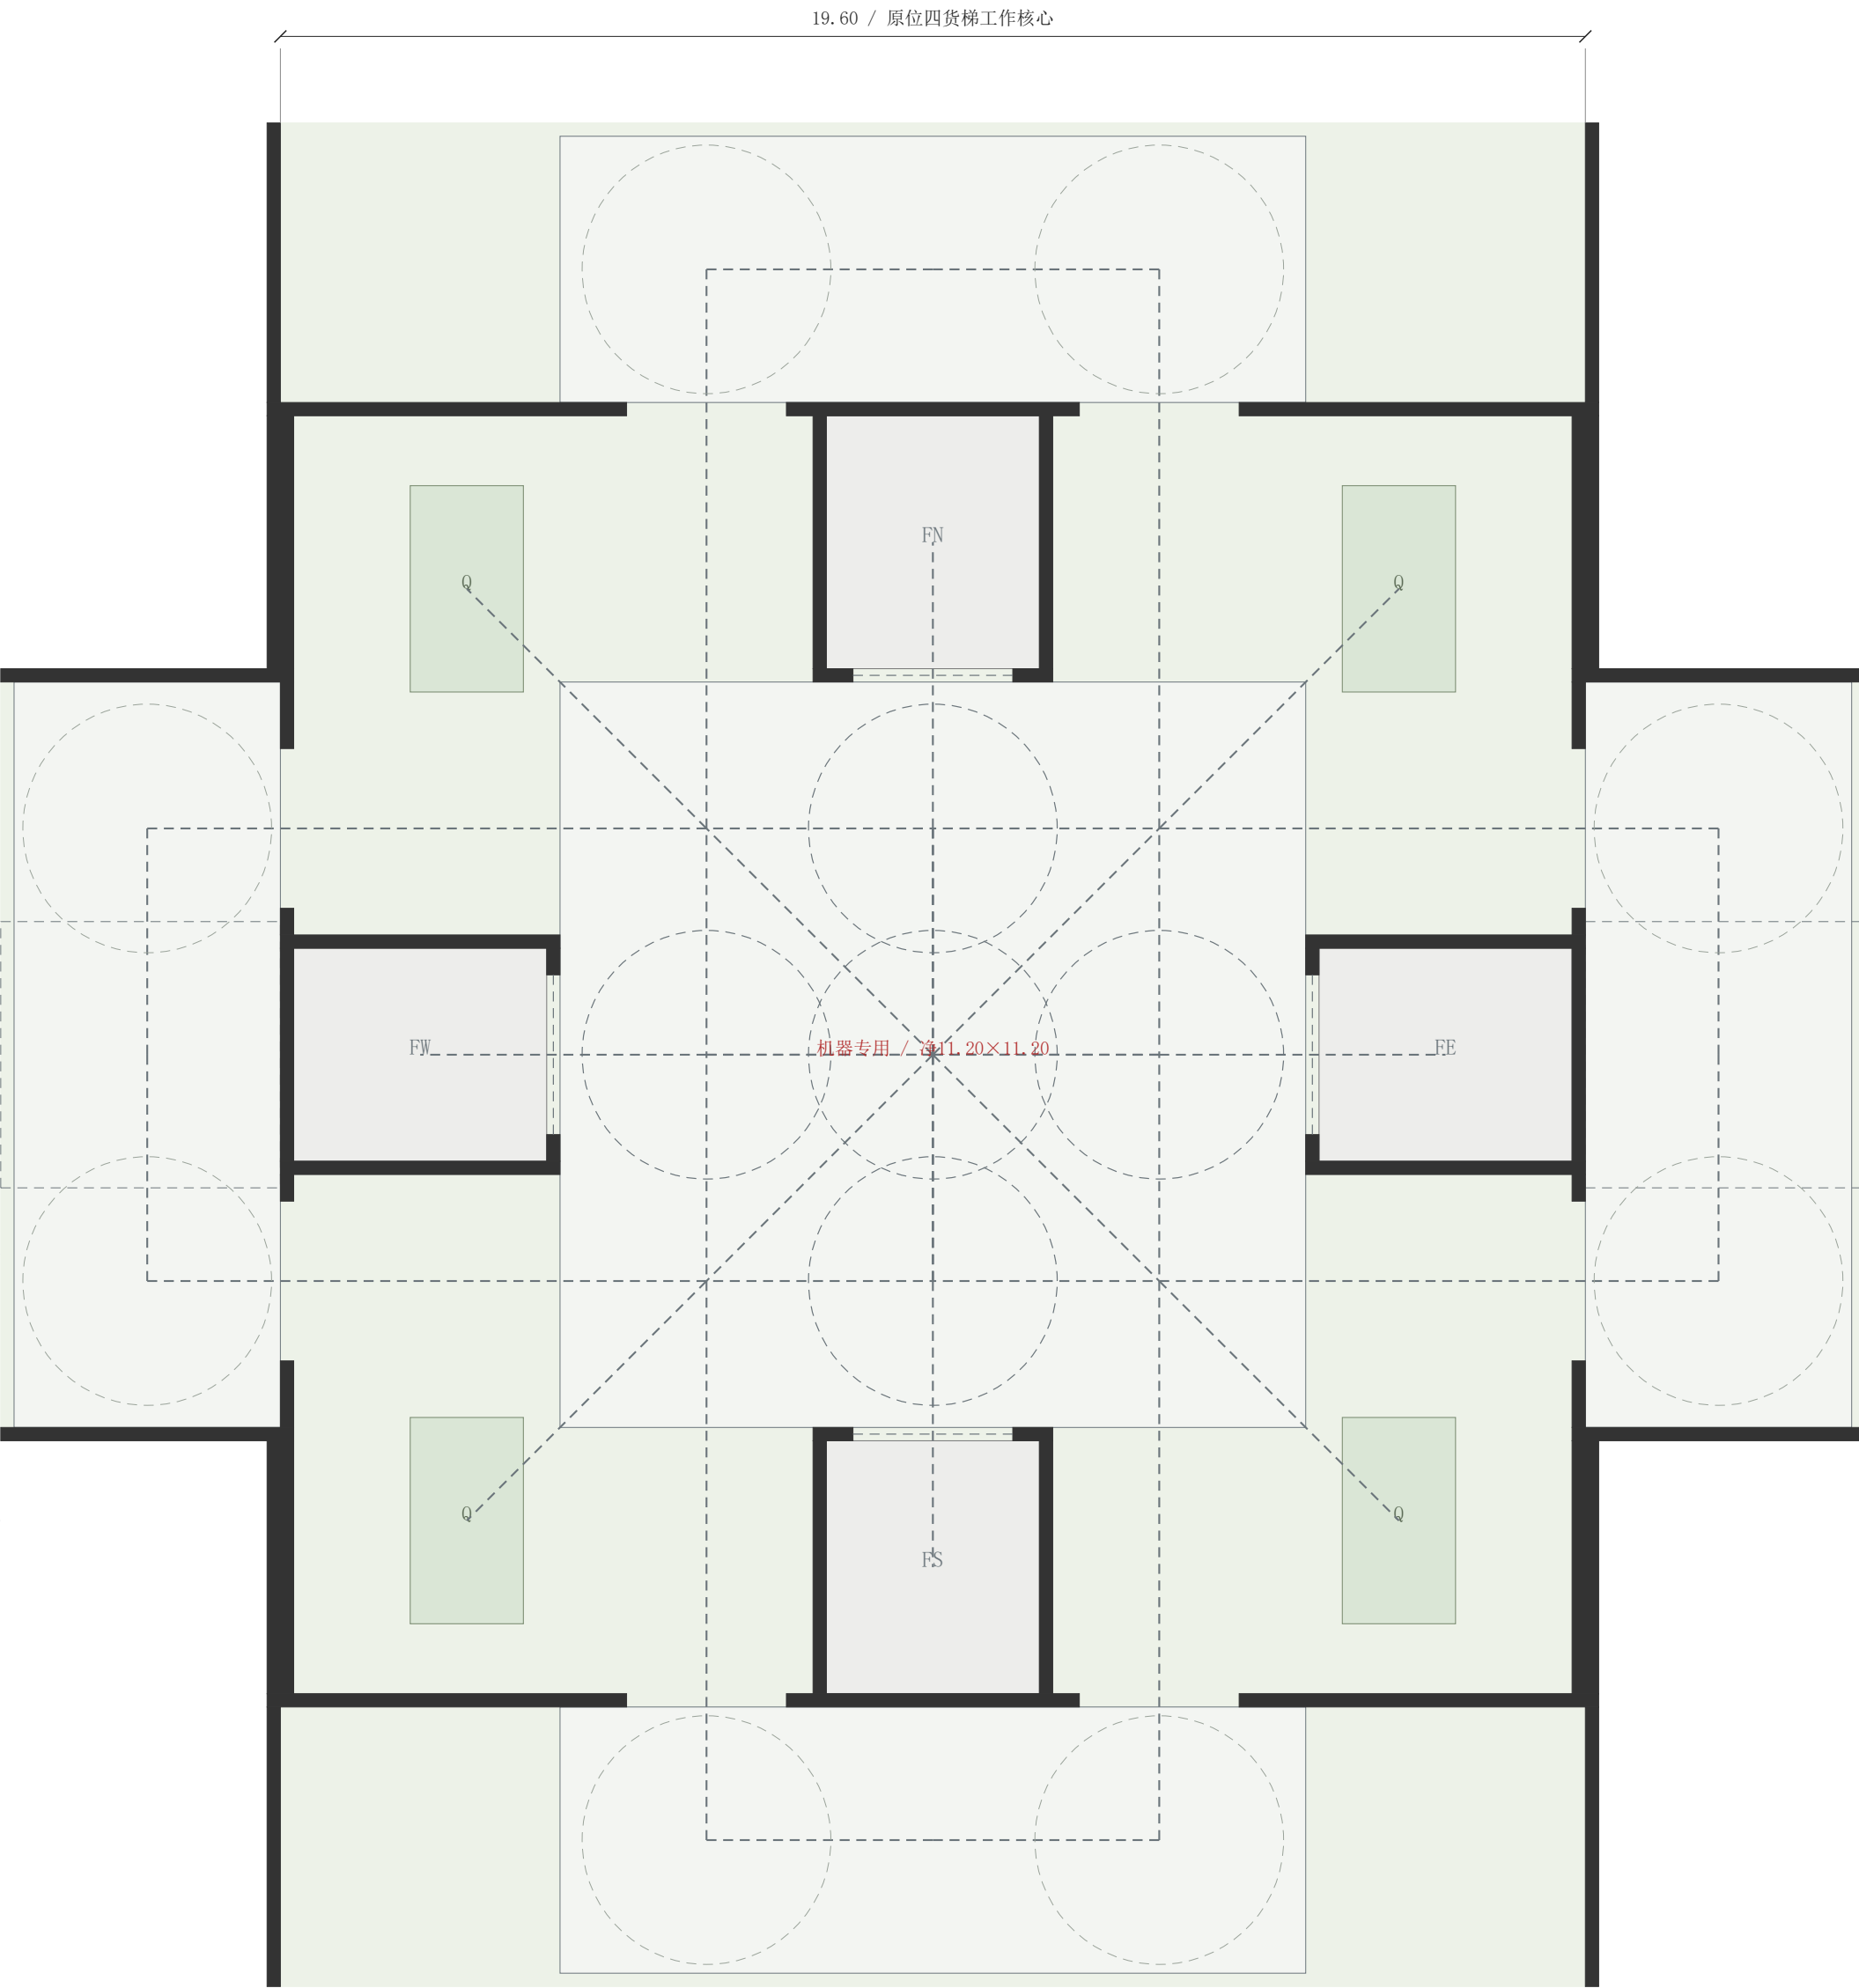

四梯净3.20×3.80 / 门2.40；八绕行口2.40；Q四个1.70×3.10。

回转圆03.736；四Q满位通行、逐台停梯绕行均经实体复核。