



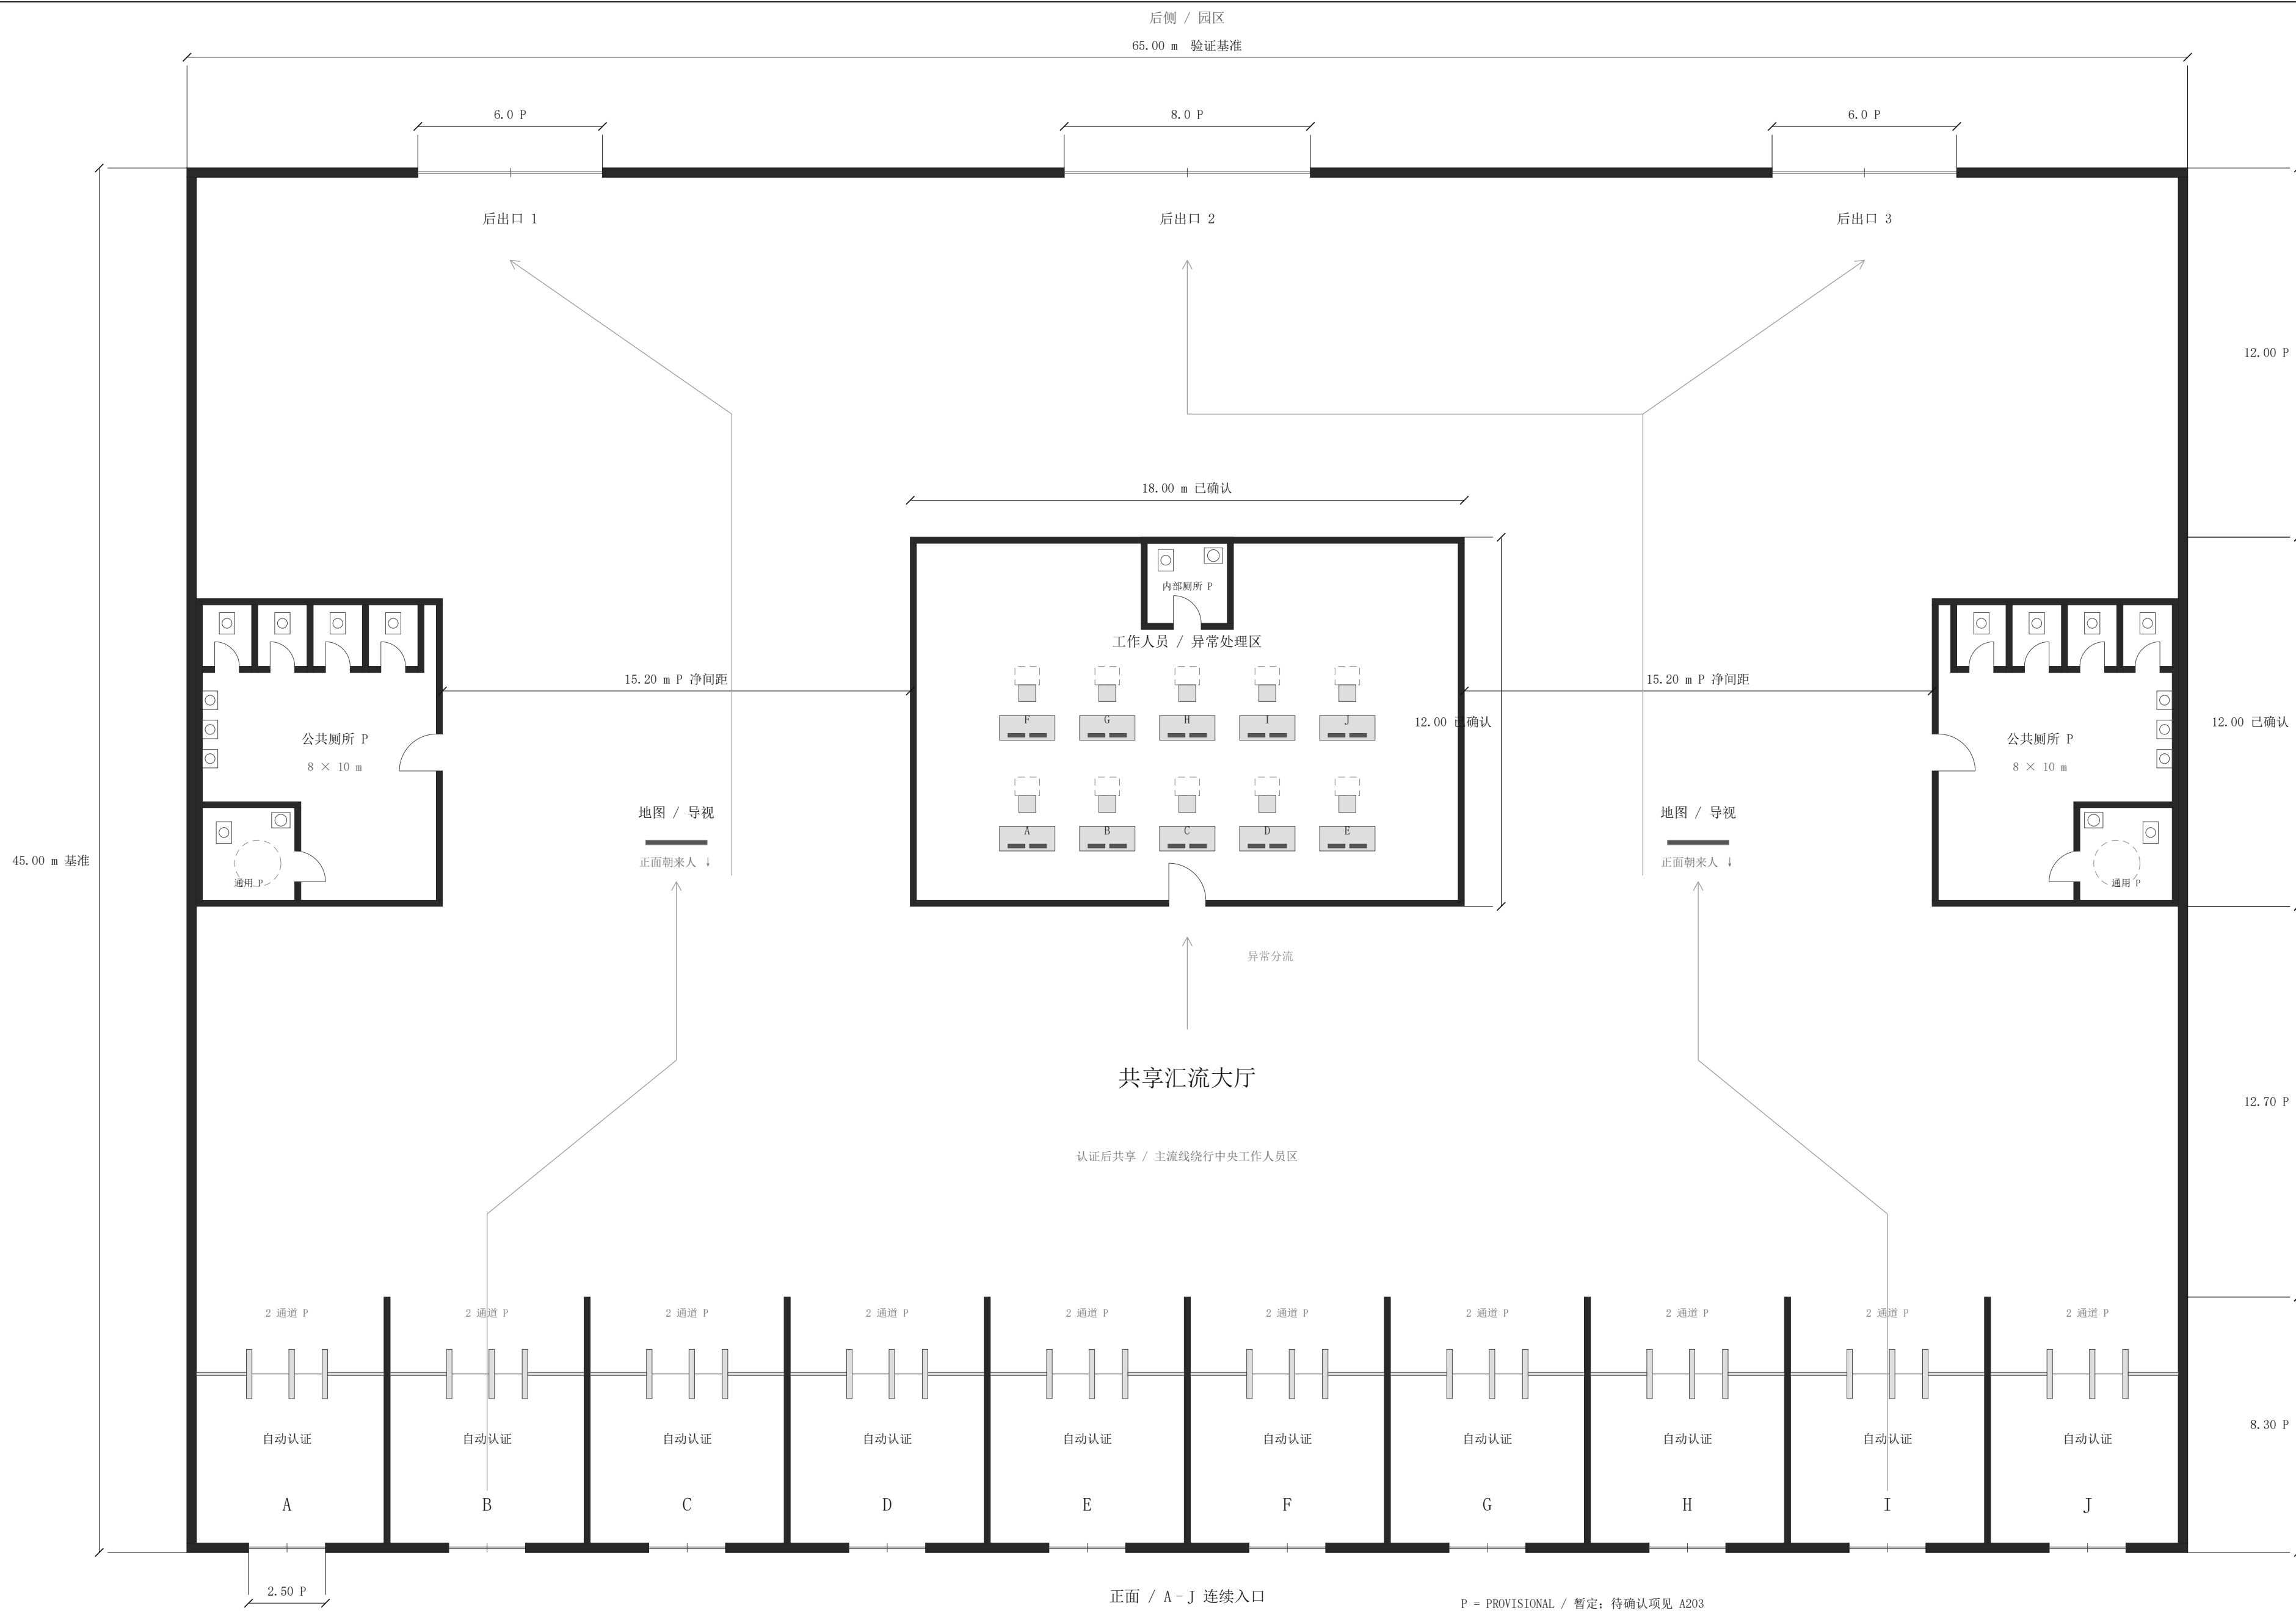

01 工作人员 / 异常处理区

边界 18×12 m 已确认；内部布局 P | 1:100

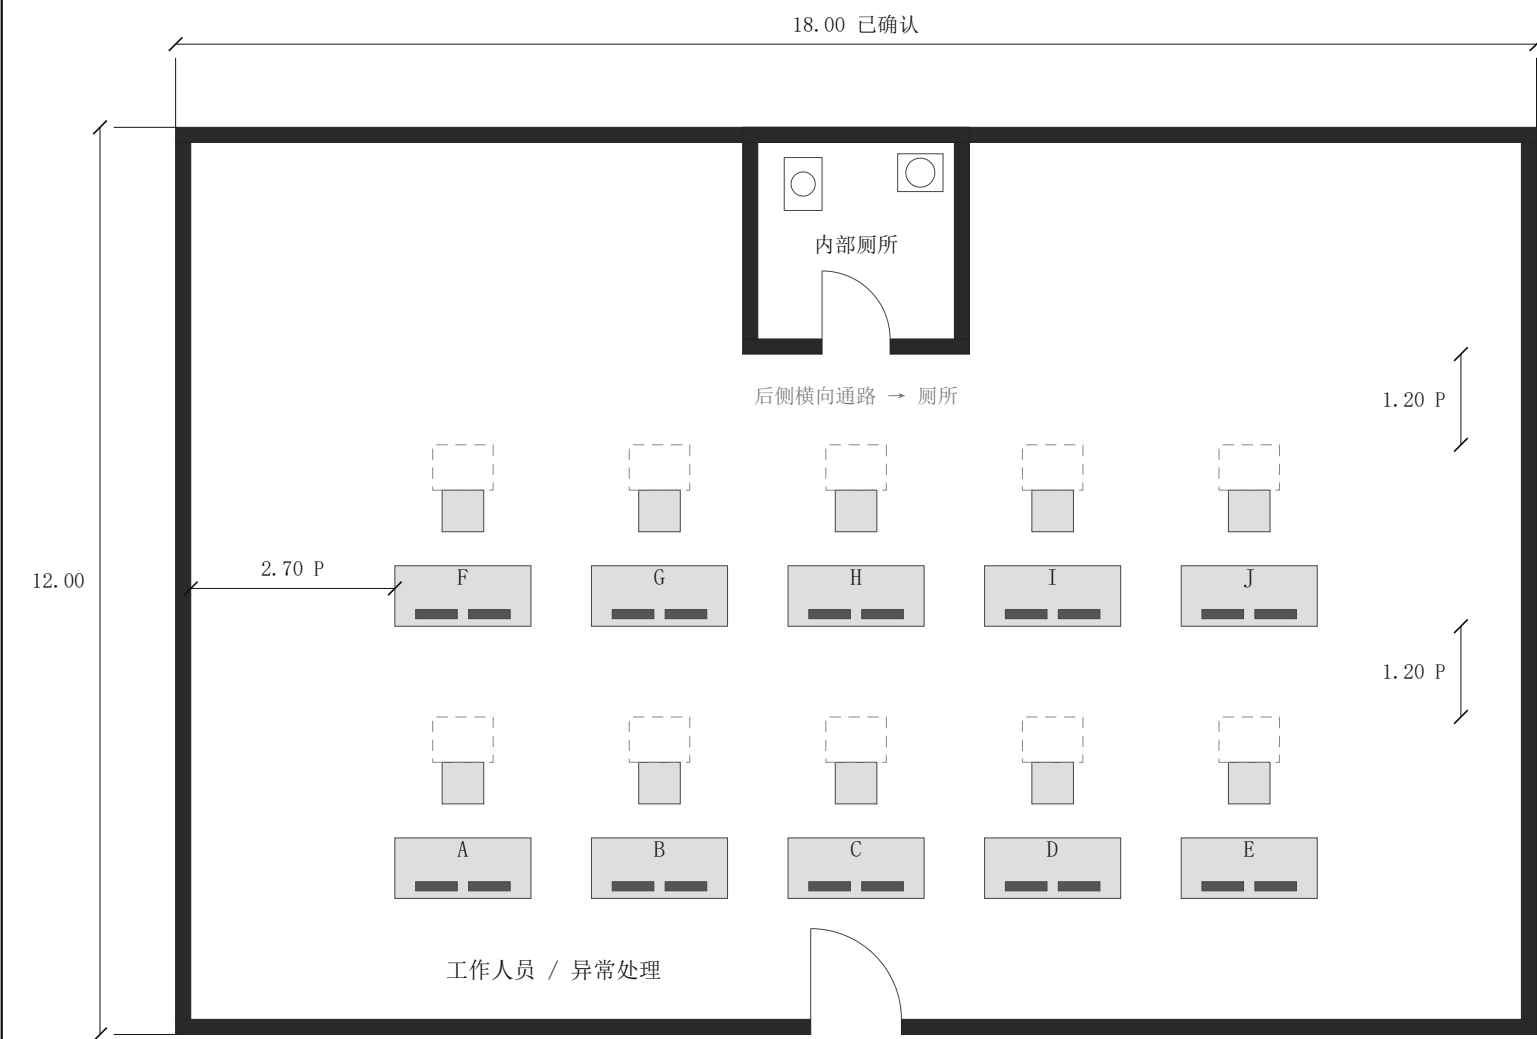

十工位 A-J，双屏，2排×5；桌面1.80×0.80 m P。


椅后另留0.60 m（虚线）；排间/厕所前净1.20/1.20 m。

侧通路2.70 m；前侧入门→侧通路→后横路→厕所。

工位编号前排A-E、后排F-J为本轮暂定落位。

02 左公共厕所（右侧镜像）

外包 8×10 m P | 1:75

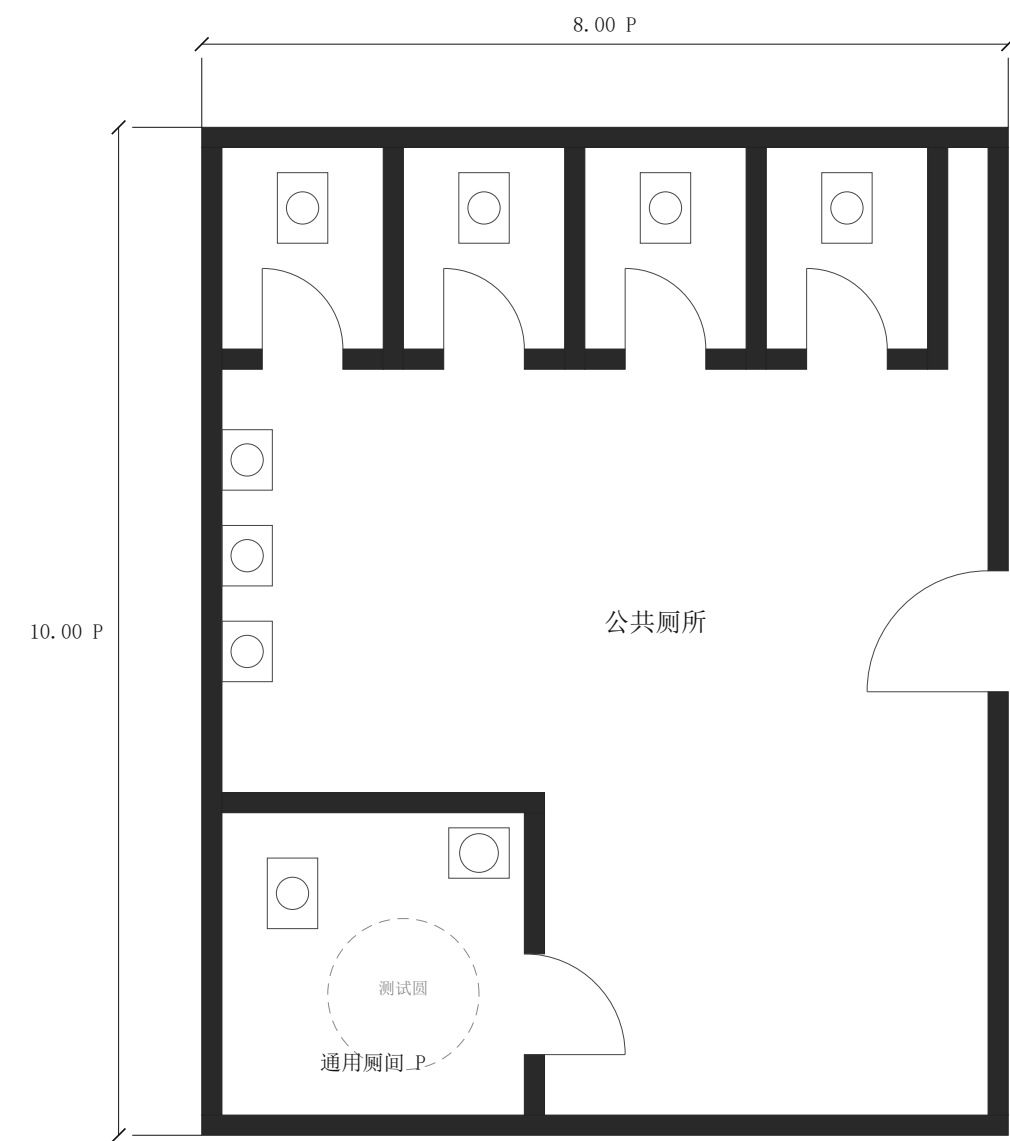


4普通厕间 + 1通用厕间 / 每侧 (P)

普通净1.60×2.00；通用净3.00×3.00 m。

1.50 m测试圆及图示洁具仅作几何检查。

03 入口 A / 认证组

其余B-J同组重复 | 1:75

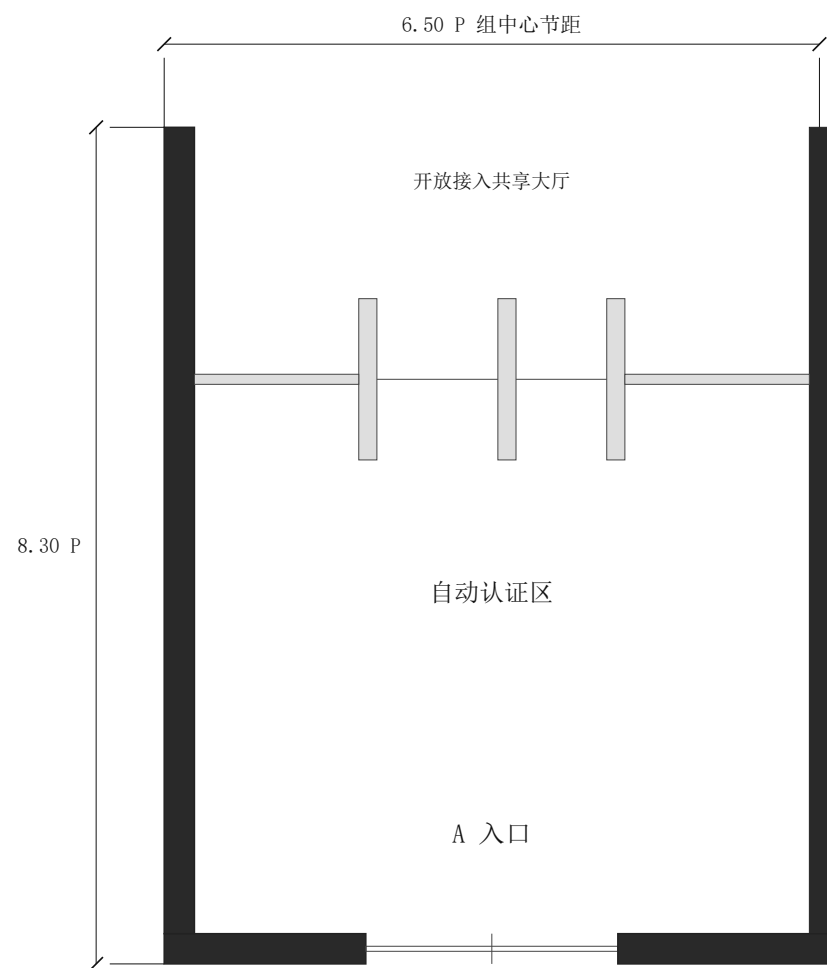

前开口 2.50 m；2条认证通道 P。

净宽1.20 / 0.90；设备长1.60 m。

闸机设备组总宽2.64 m P。

本轮设计阶段暂定值（P / PROVISIONAL）

外墙0.30 m；隔墙0.20 m；公共厕所入口1.20 m；通用门1.00 m；普通门0.80 m。

工作人员内部厕所门0.90 m；门扇、洁具、工作台与地图均为可测量的简化占位。

边界与尺寸均使用同一建筑坐标；局部放大保留主图坐标关系。

门扇开启方向为方案测试；无障碍、疏散、结构与机电合规复核 TBD。

已确认 / 当前验证基准

单层：十入口→认证→共享大厅→两侧地图→三后出口；工作人员区有十个双屏工位。

工作人员区边界18×12 m：用户确认。建筑外包65×45 m：当前验证基准，最终外包待确认。

本轮 PROVISIONAL 参数

墙 / 门 外墙0.30；隔墙0.20；前开口2.50；后开口6 / 8 / 6 m；门型及开启P。

定位 工作人员X=23.50，Y=21.00；两公共厕所Y=21.00 m，均以外边界定位。

工作人员 厕所3×3 m，靠后墙居中；10工位2×5；桌1.80×0.80；纵向节距3.60 m。

公共厕所 每侧外包8×10 m；4普通+1通用；普通净1.60×2.00；通用净3.00×3.00 m。

认证组 每组2通道，净宽1.20 / 0.90；条宽0.18、长1.60；前端Y=5.00；净深8.00 m。

通路 / 导视 椅后另留0.60；排间/厕所前1.20/1.20；侧路2.70；地图2×0.15 m，朝前，两旁≥6.60 m。

面积 / 参数修改

外包面积2925 m²；工作人员边界216 m²（含内部厕所9 m²）；两公共厕所合计160 m²。

各分区数字为方案边界面积，包含其墙体；不代表净使用面积或容纳人数。

FreeCAD Parameters内长度/XY直接驱动草图和A204；ParameterTable列出状态与单位。

出版页为快照；用build_freecad.py --parameters-from 已修改文件.FCStd重建，再运行GUI宏与PDF导出。

仍需确认 / TBD

最终外包与各P参数；厕位配置与通用厕间要求；门型/开启；工作人员真实设备与控制范围。

结构、标高、层高、屋面、机电、防火疏散与适用规范；导视信息及园区出口衔接。

峰值到场率、认证服务时间、失败分流比例、出口流率及大厅停留时间：未输入，吞吐结论TBD。

依据：CRYO_FACILITY_LAYOUT现行版 / REDRAW_BRIEF；仅几何适配通过，尚未验证法规或运行容量。