


尺寸单位 m；约值为当前验证基准。实线为有依据的尺寸线；虚线/关系符号不构成定位。

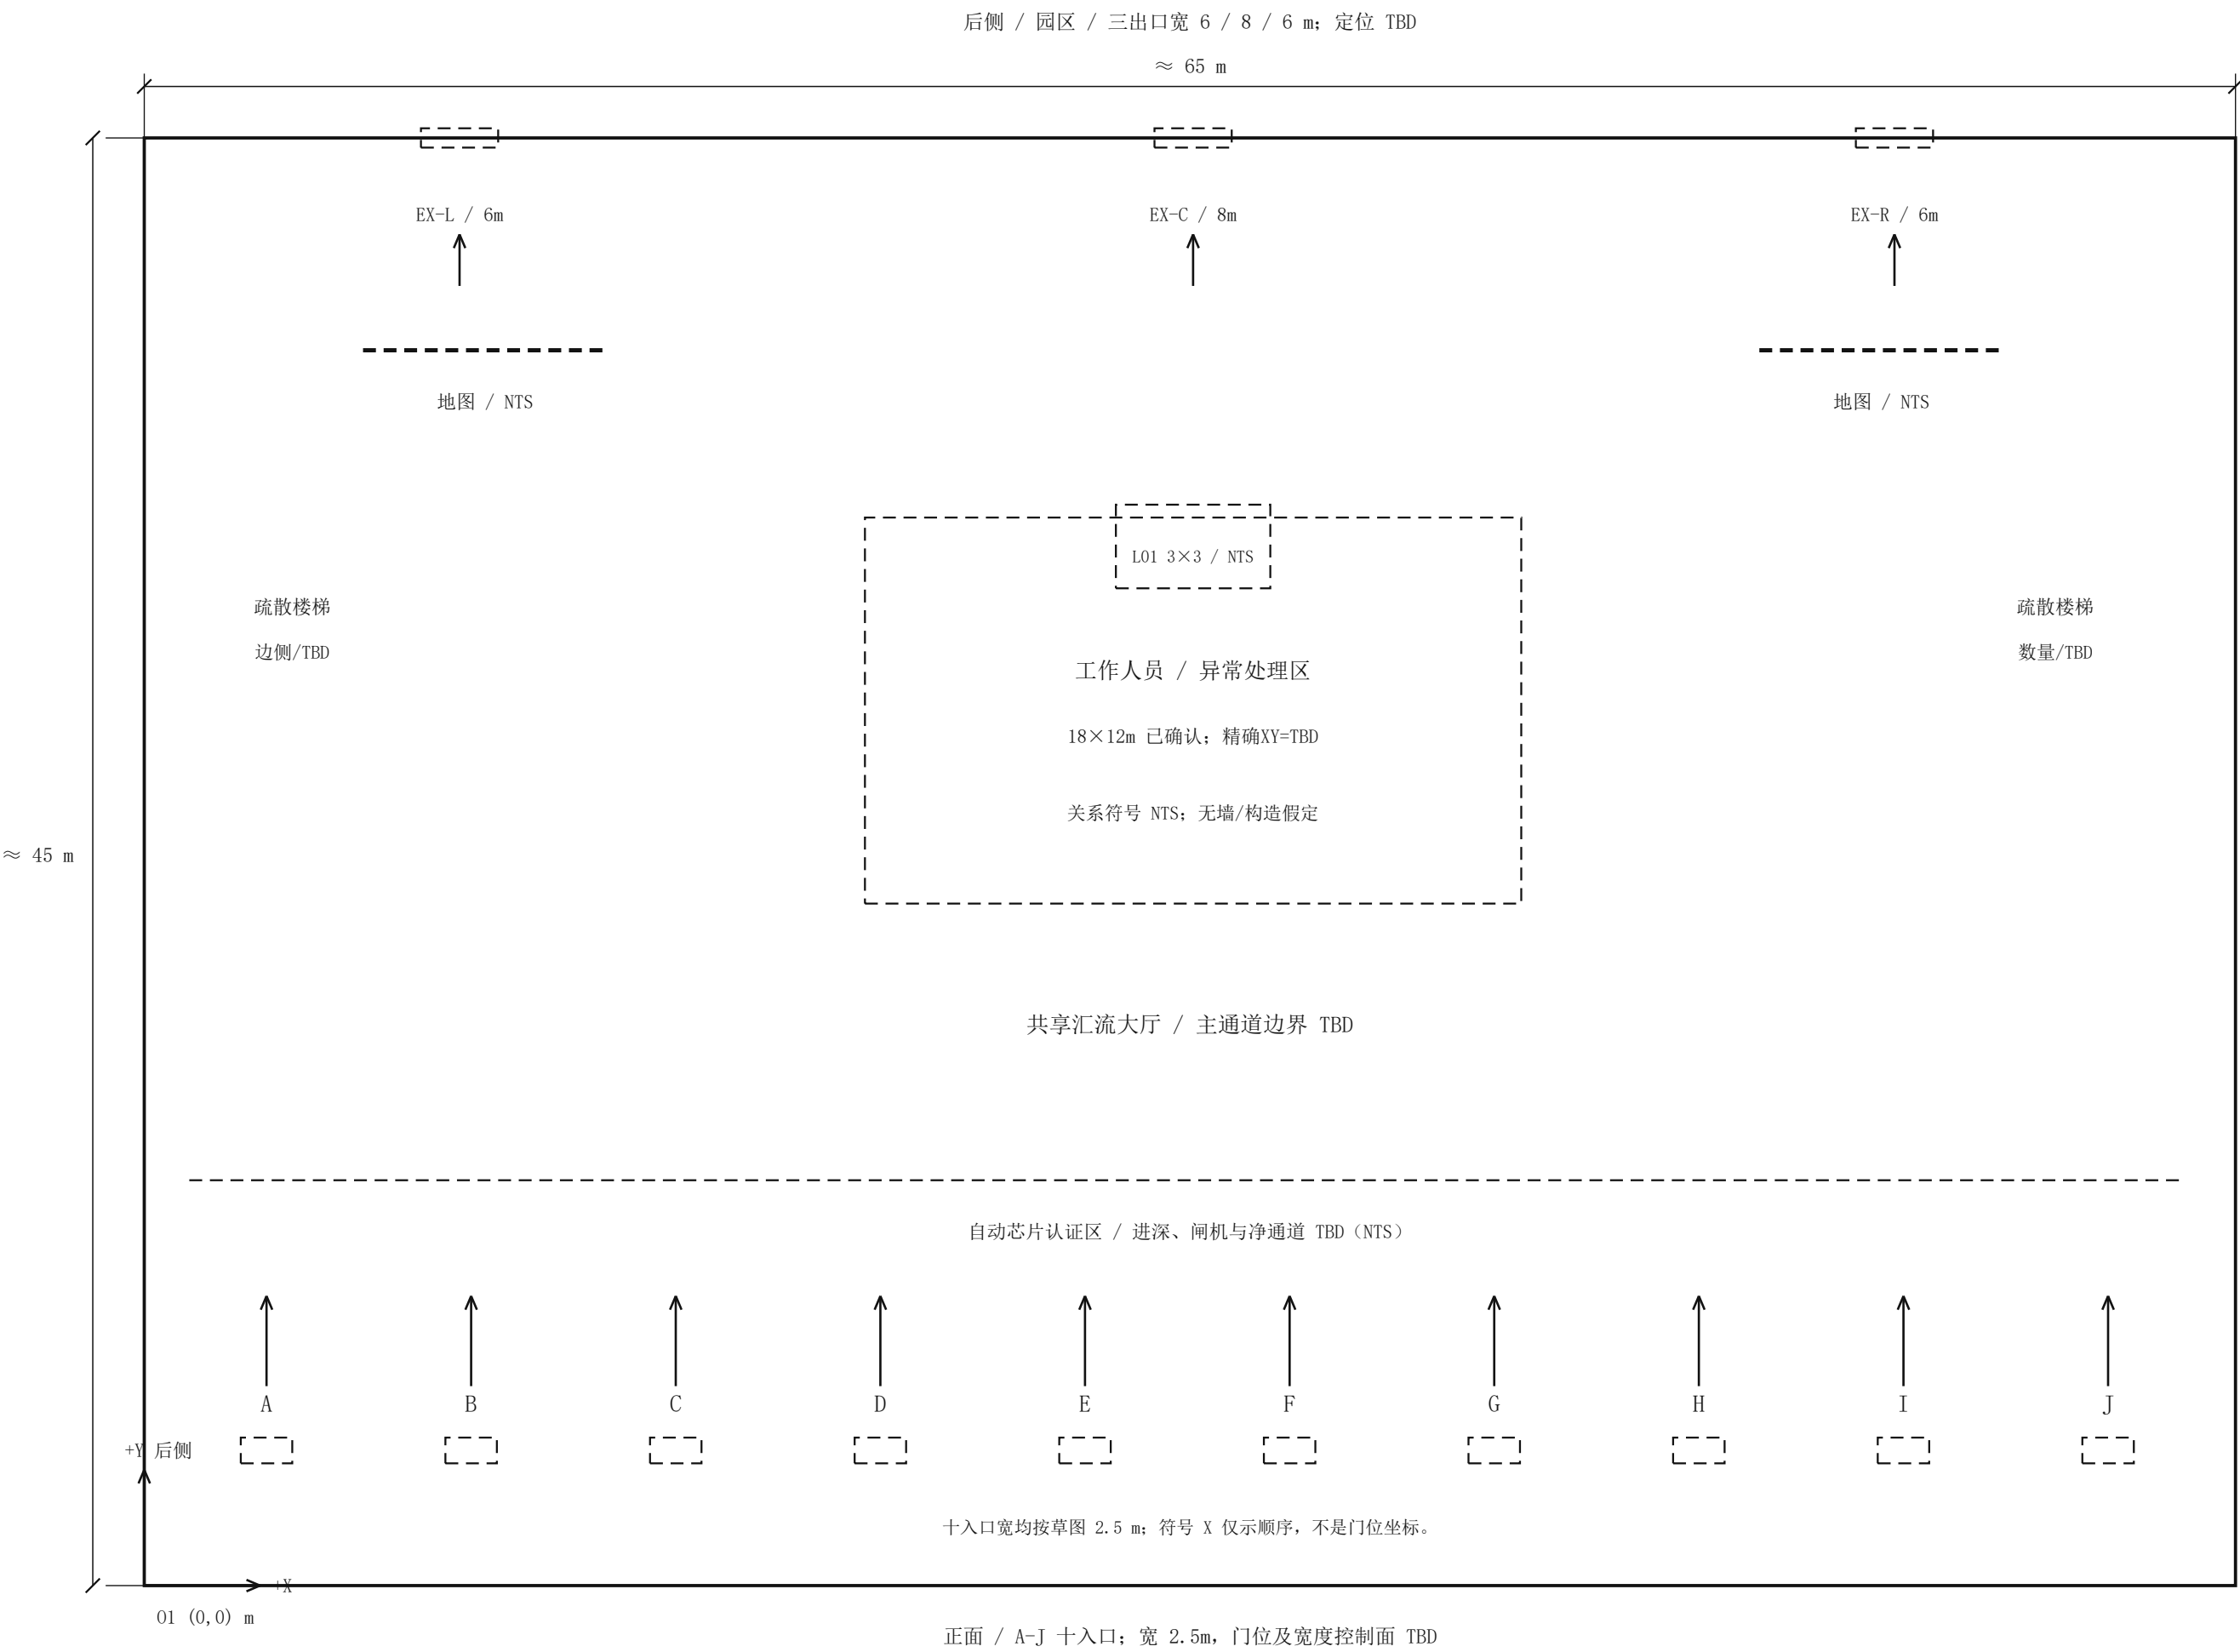

运营流线 / 不按比例，不用于量取位置



例外支路：认证异常 → 工作人员岛

日常上下：后侧升降台 → 2F

紧急疏散：边侧封闭楼梯

T02-T07：位置、边界及工程构造 TBD

1F 外包基准面积：2,925 m²


内部符号 NTS：不可量取门位/区域位置。

楼梯按文档边侧要求；与草图冲突见 T07。

1F 公共/无障碍卫生间：是否设置 TBD。

主要尺寸部件见 A103；待确认清单见 A104。

尺寸单位 m；约值为当前验证基准。实线为有依据的尺寸线；虚线/关系符号不构成定位。

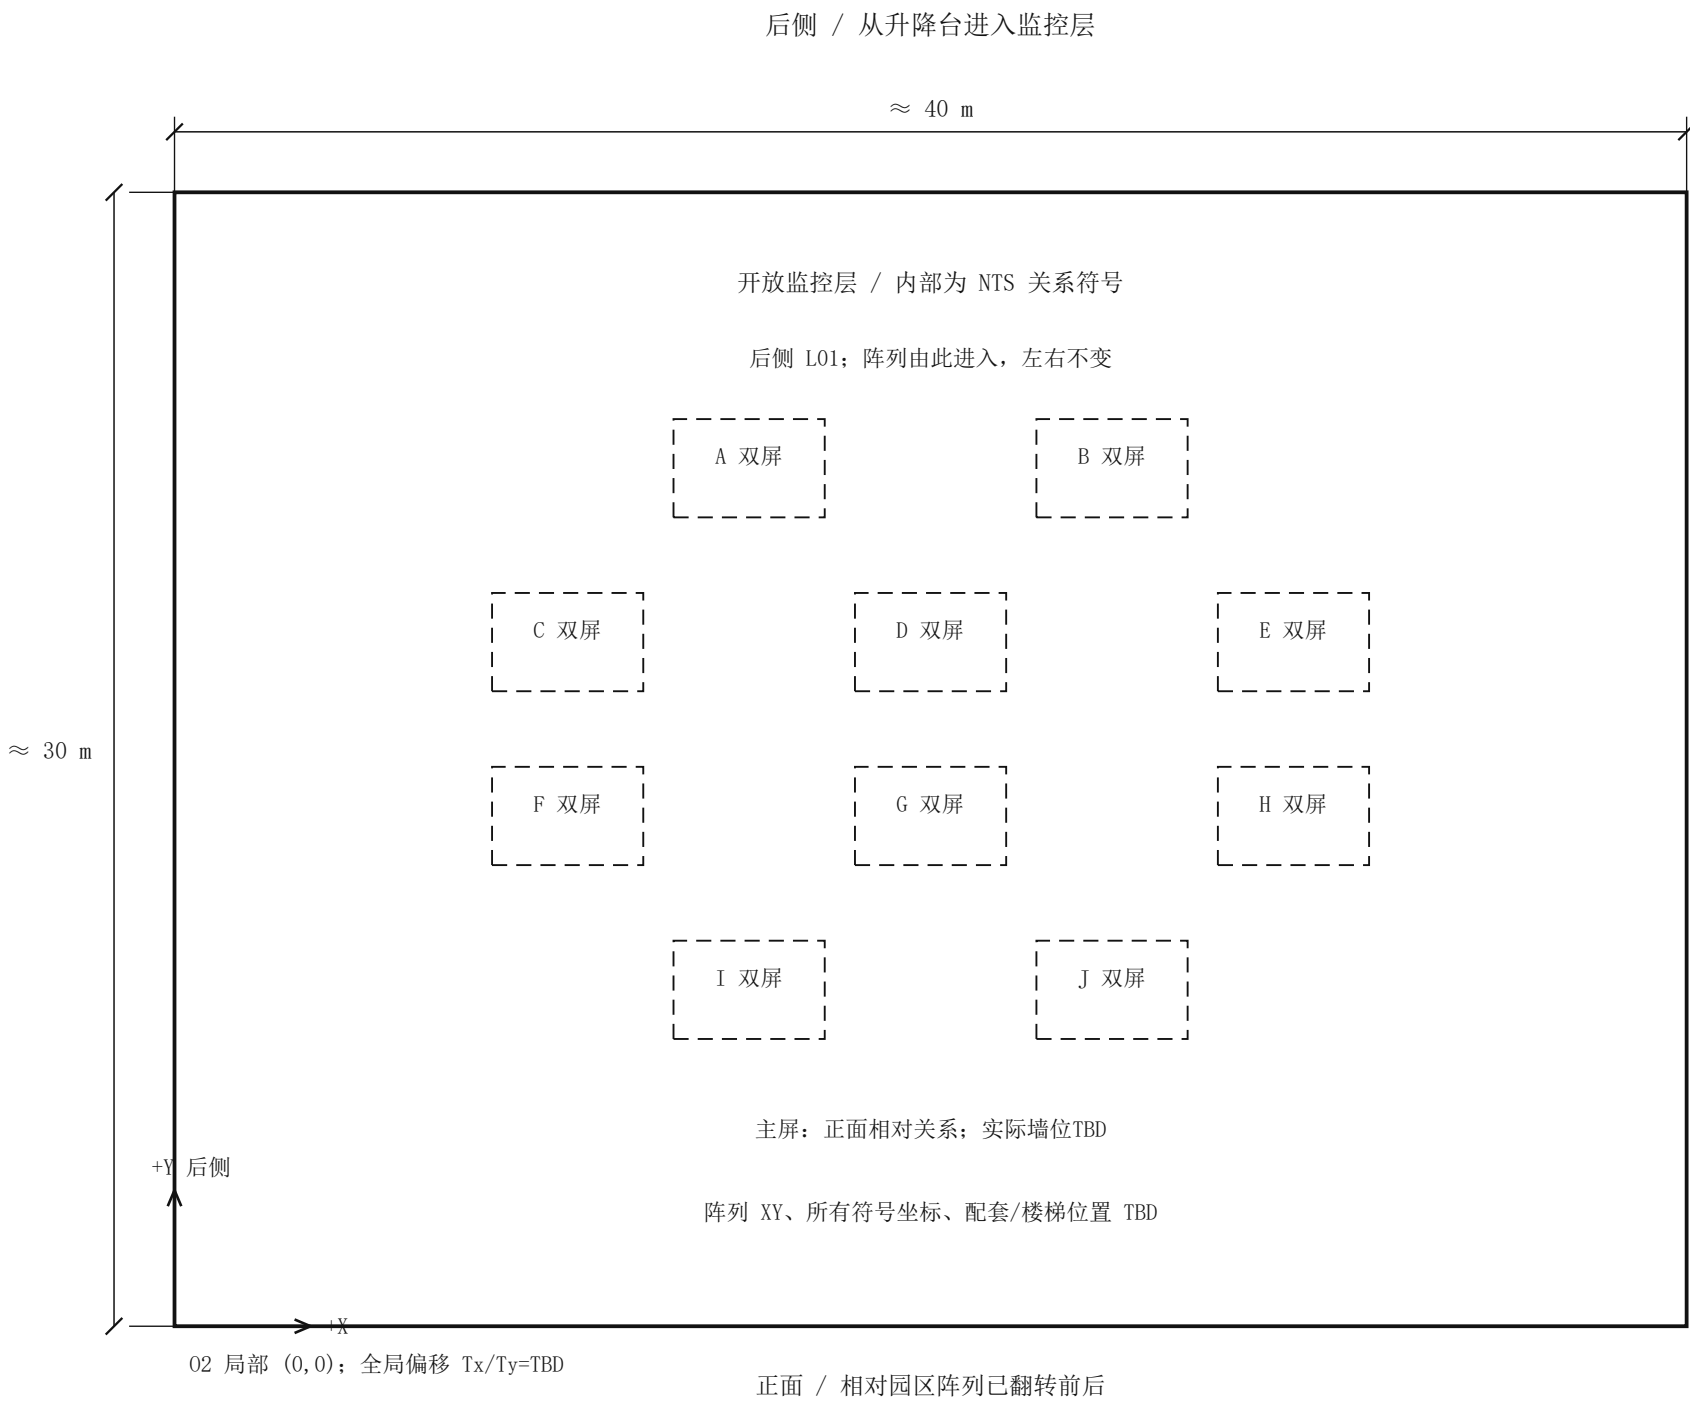

统一轴向：+X 左→右；+Y 正面→后侧。

2F 全局坐标：X=X2+Tx；Y=Y2+Ty；Tx/Ty=TBD。

本版未做上下层实体对位；不以任意层高或居中偏移替代。


WC01 边角；EQ01 靠墙开放柜列；边侧楼梯与1F对应。

主屏、卫生间、设备柜的已知尺寸详见 A103。

2-3-3-2 / 工位模块范围验证

独立局部原点：本图不表示阵列在 2F 的位置

后侧升降台 → A/B → C/D/E → F/G/H → I/J

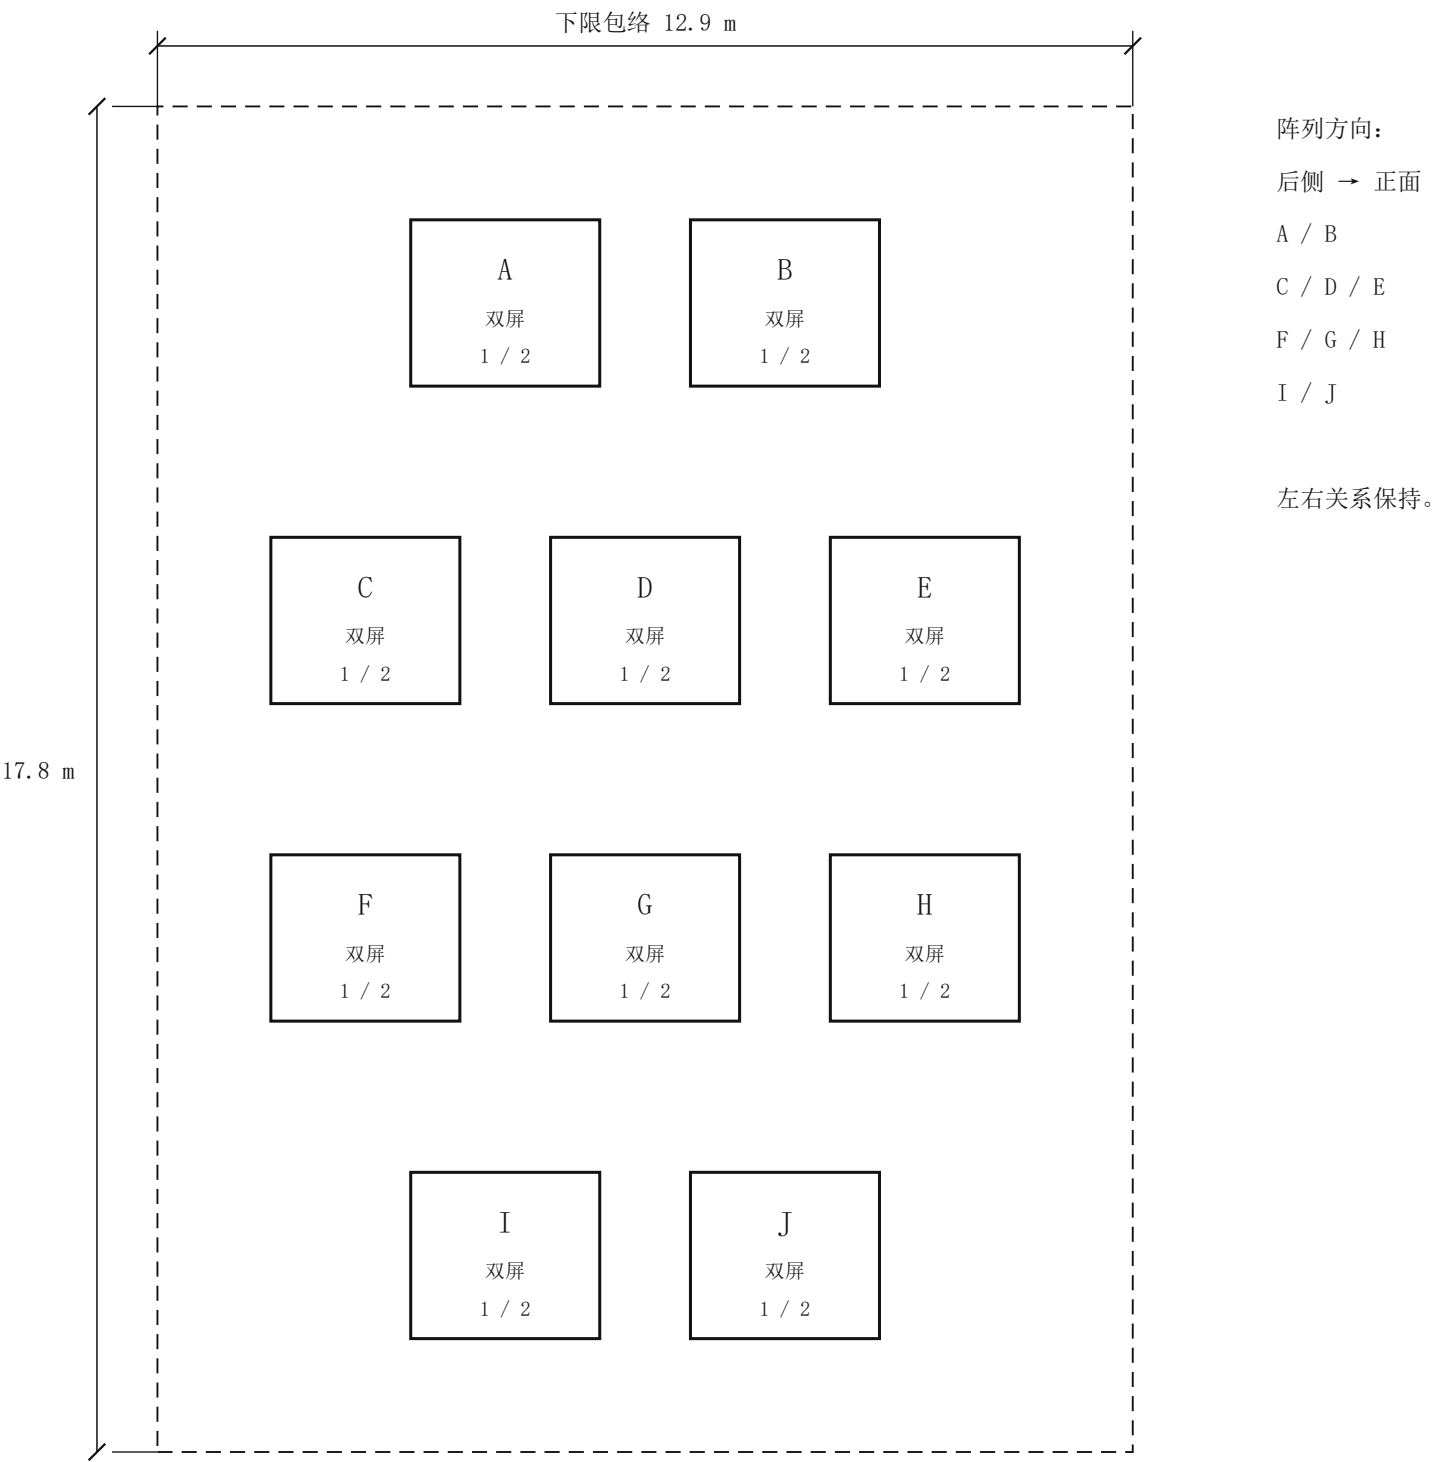

此处仅检验文档通道范围的下限组合，不选定最终通道。


同排净距 1.2-1.5 m；前后通道 2.0-2.4 m；外圈 1.5-2.0 m。

全取下限：12.9×17.8 m；全取上限：14.5×20.0 m。


含外圈通道，两种边界均小于 40×30 m 外包；

墙厚、配套、疏散及阵列最终落位未定，不能据此证明完整净空。


尺寸单位 m；约值为当前验证基准。实线为有依据的尺寸线；虚线/关系符号不构成定位。

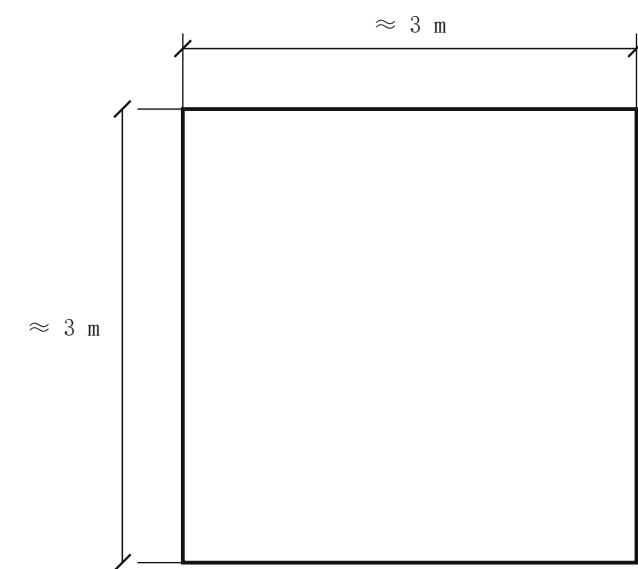

L01 升降台 / 1F与2F共用同一母版

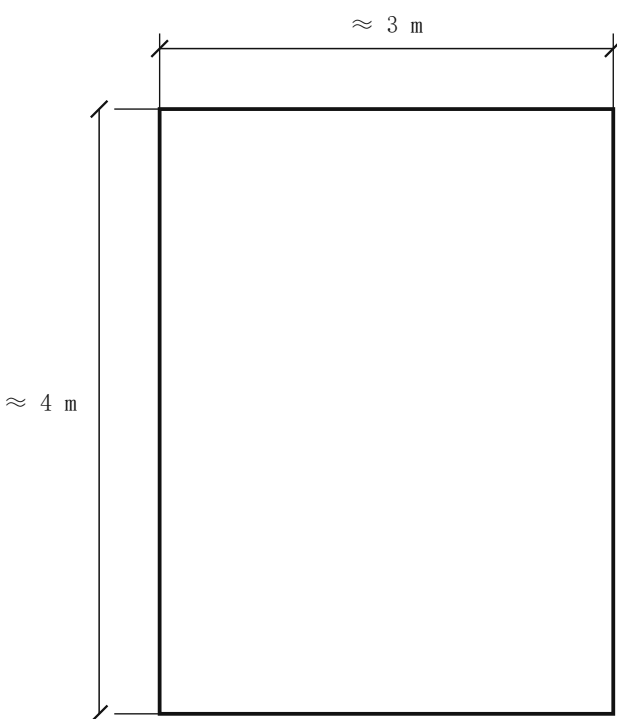





WC01 工作人员卫生间

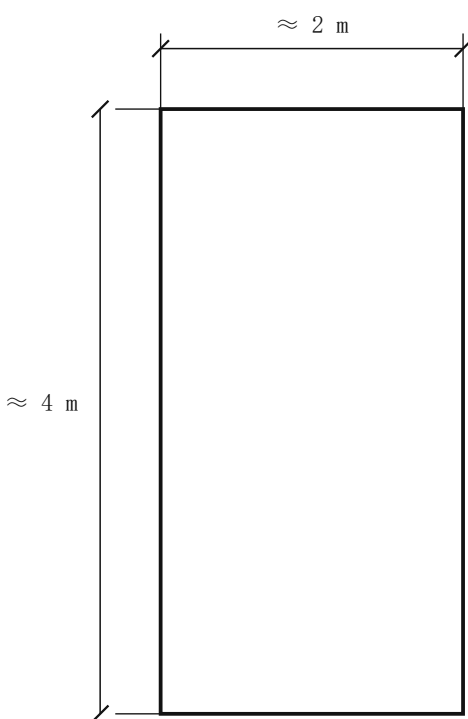


EQ01 靠墙设备柜区（开放区域）

草图标注门宽 / 1:100


正面十入口：每处2.5m

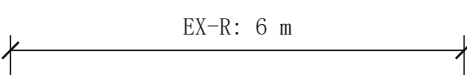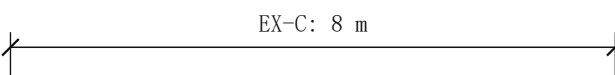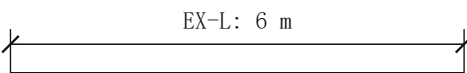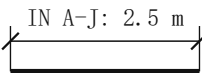

门位/洞高/门型/宽度控制面 TBD

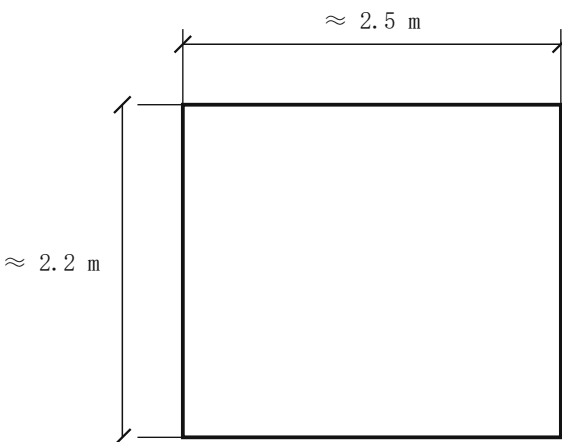

W01 工位模块（含椅子/操作余量）

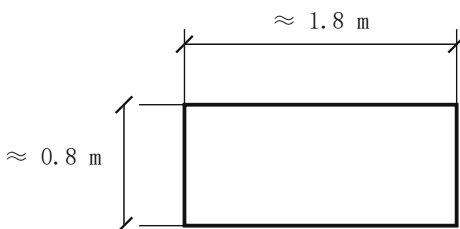


D01 桌面 / 10套；双屏尺寸 TBD

桌面与模块分别标注尺寸。

内部相对位置、朝向、座椅与双屏

仅有功能要求，未新增物理尺寸。

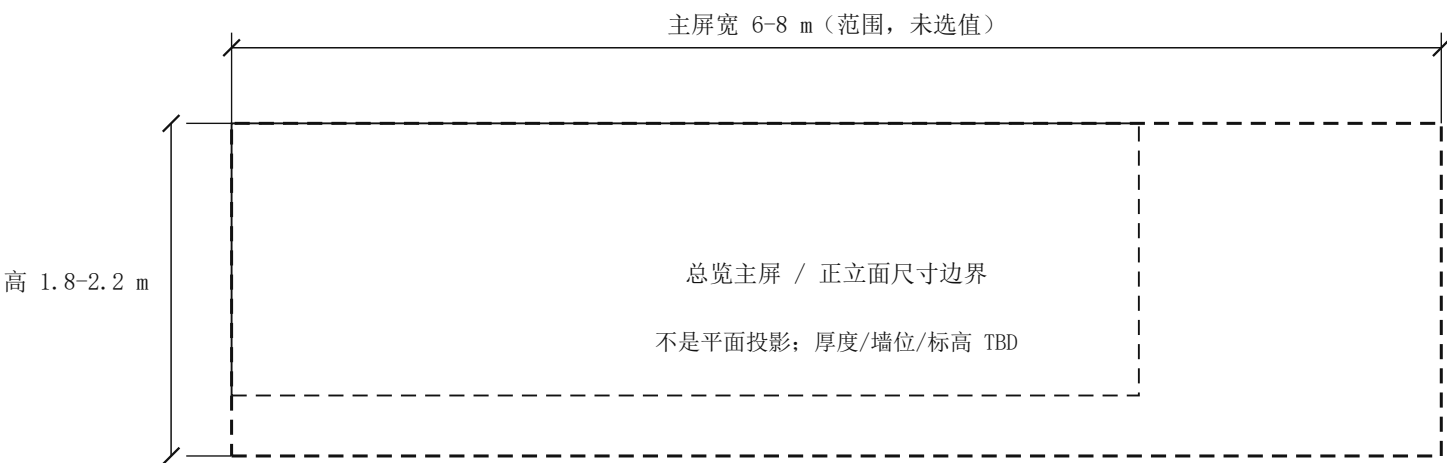


工位通道范围：同排 1.2~1.5 m；前后 2.0~2.4 m。

外圈巡查通道 1.5~2.0 m；最终取值及控制面 TBD。

疏散楼梯无可引用的管理楼工程尺寸，本版不画踏步。

尺寸单位 m；约值为当前验证基准。实线为有依据的尺寸线；虚线/关系符号不构成定位。

只列影响本轮管理设施工程平面的事项；没有以建筑经验补齐任何未定值。

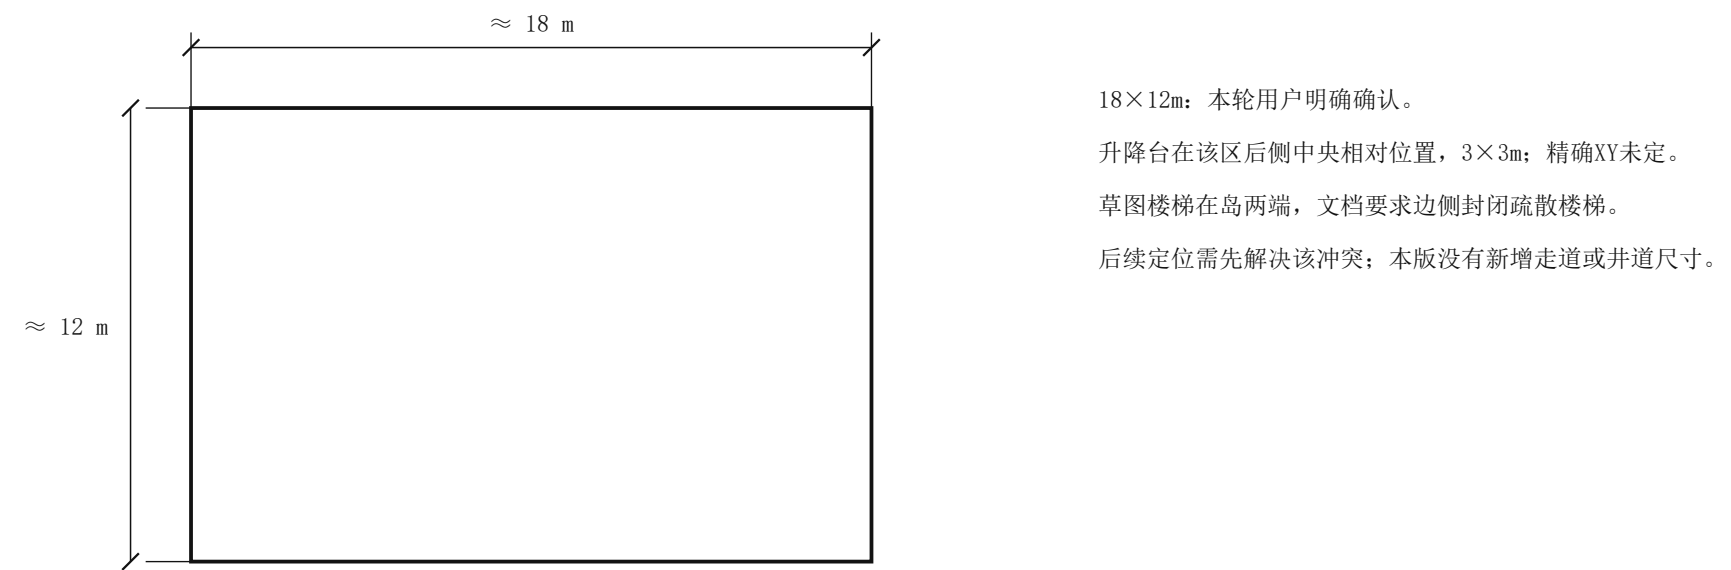

ST01 工作人员区 / XY、边界控制面 TBD

T01	墙与结构	墙厚、墙体类型、内外表面定义；柱网、柱截面、结构与防火分隔。
T02	1F 十入口	A-J顺序和宽2.5m见草图；各门中心X、宽度控制面、洞高、门型/开启方式未定。
T03	自动认证	认证区进深、闸机尺寸/数量、通道宽和异常分流位置。
T04	1F 三后出口	草图宽6/8/6m；三门中心X、宽度控制面、洞高、门型；不绑定楼栋。
T05	工作人员岛	18×12m由用户确认；精确XY、边界控制面、区域围护/出入口TBD。
T06	升降台	后侧中央区域内的精确 XY、井道/外围护、上下口方向和平台净尺寸定义。
T07	疏散楼梯	草图在岛两端，文档要求建筑边侧封闭楼梯；按文档。位置/数量/全部构造TBD。
T08	上下层对位	2F 相对 1F 的 X/Y 偏移、准确楼面标高、楼板厚度；草图没有定位尺寸。
T09	2F 工位定位	阵列在 2F 的坐标与朝向；范围内实际通道值；桌面、椅子与模块内部位置。
T10	双屏与主屏	各显示器物理尺寸/支架；主屏实际宽高、墙位、厚度、安装标高。
T11	2F 配套	卫生间具体边角、门洞/围护/洁具；柜列墙位、柜数、朝向及操作净距。
T12	导视与公共卫生间	导视具体位置/占地；1F 公共/无障碍卫生间是否设置及尺寸。

所有 CAD 尺寸内部单位为 mm，导出图用 m；约值为验证基准而非最终建造公差。

零件和范围阵列有各自局部原点；未填写的建筑定位不是（0,0）。

2F 相对 1F 偏移、精确楼面标高、楼梯/升降台定位未确认，故未生成虚假的上下层3D对位。