


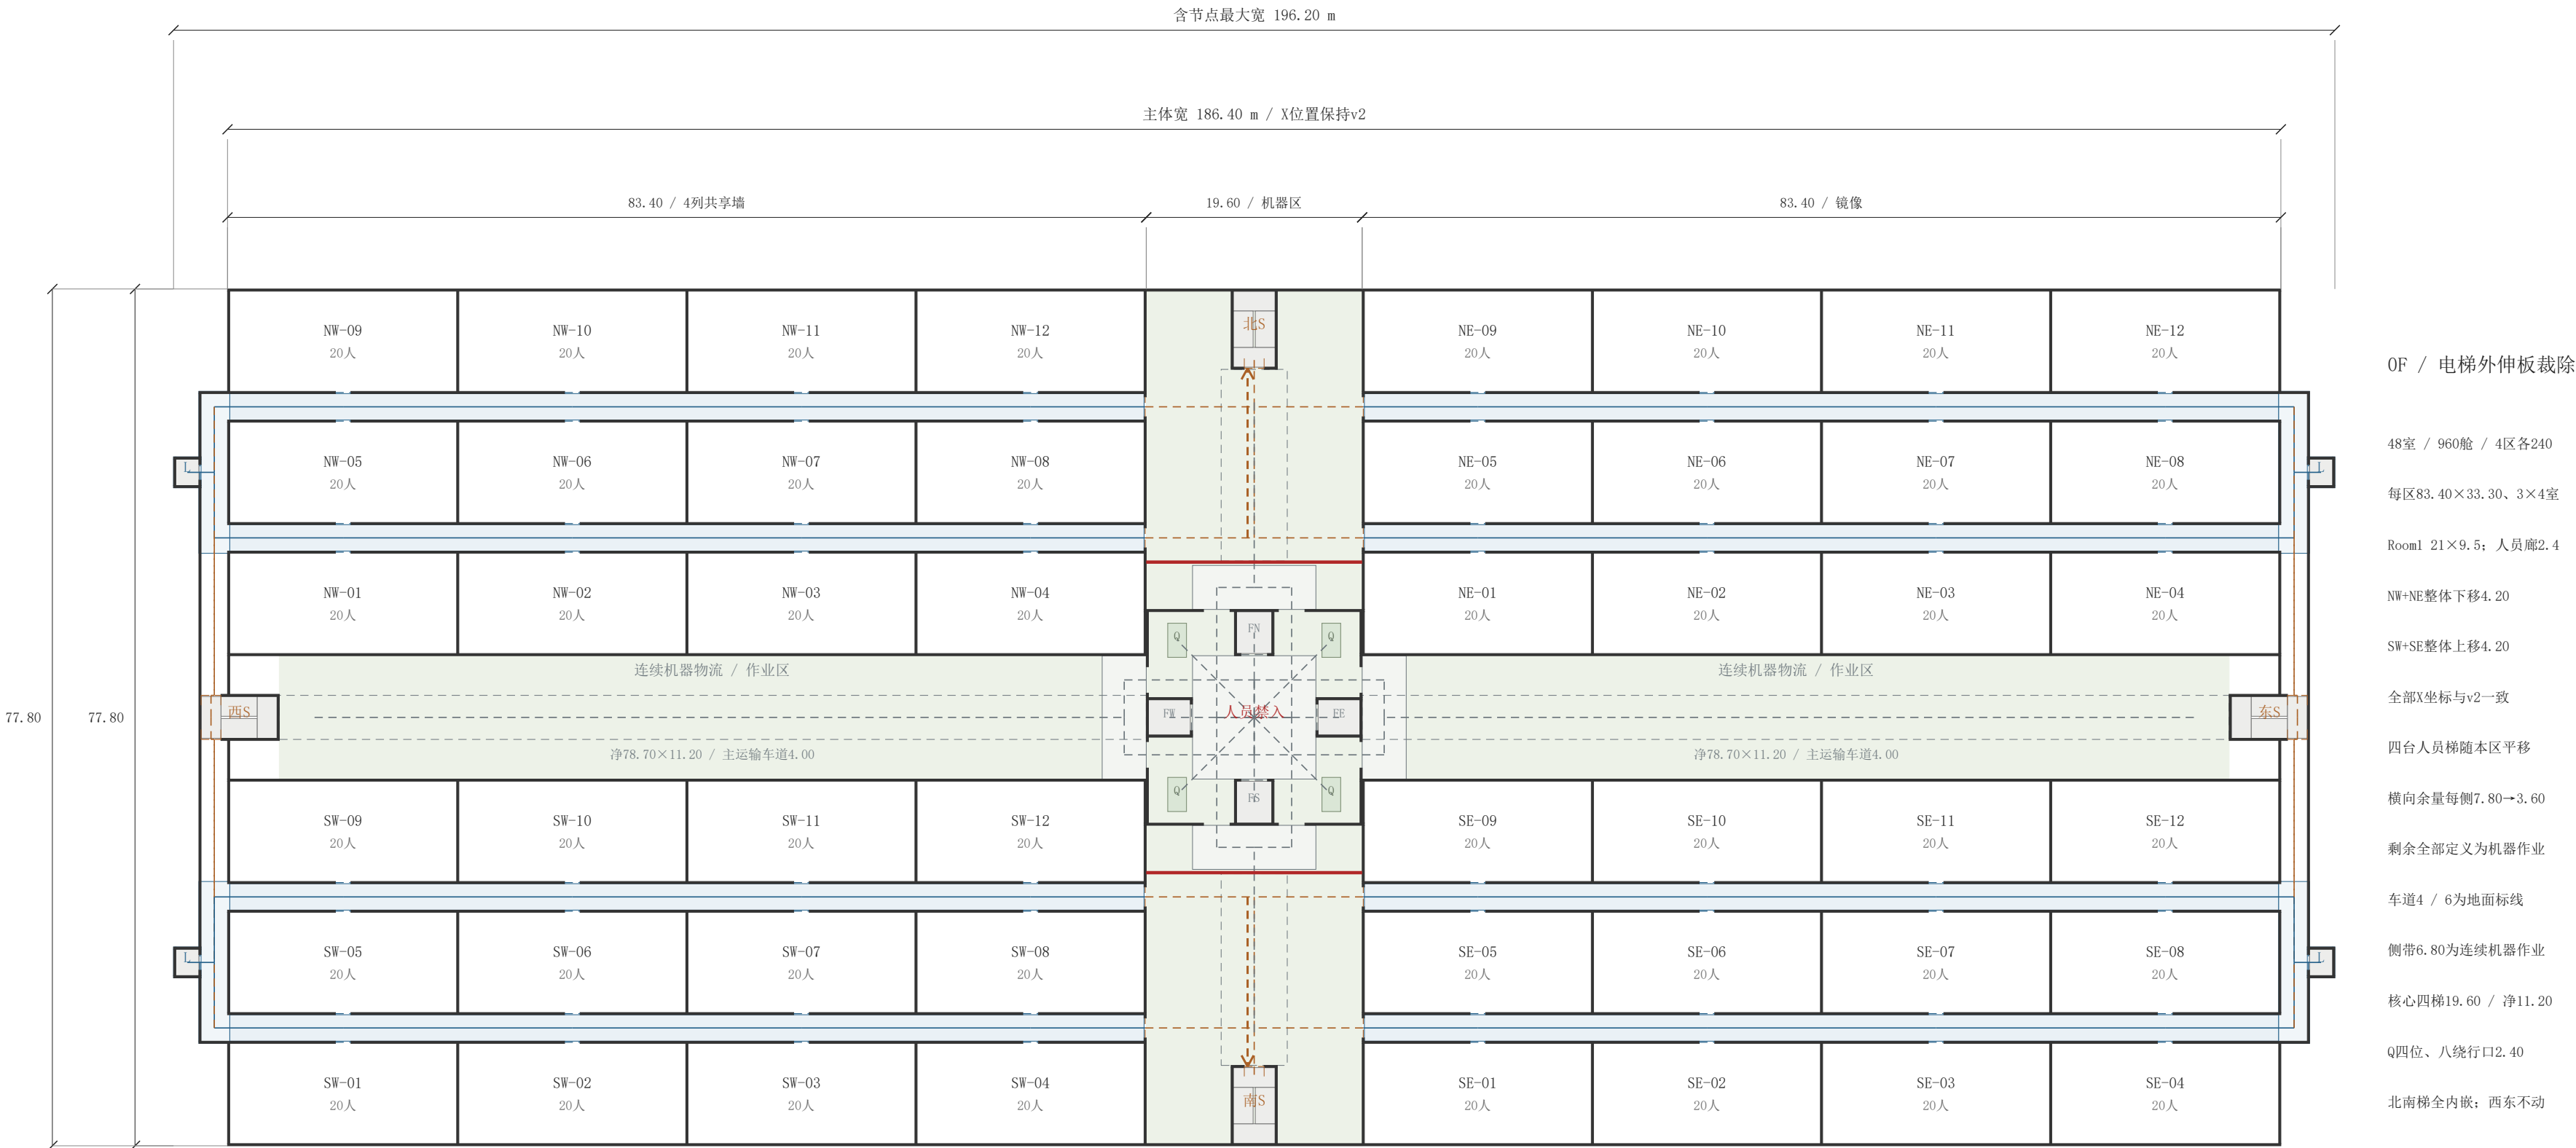

0F / 电梯外伸板裁除

48室 / 960舱 / 4区各240

每区83.40×33.30、3×4室

Room1 21×9.5; 人员廊2.4

NW+NE整体下移4.20

SW+SE整体上移4.20

全部X坐标与v2一致

四台人员梯随本区平移

横向余量每侧7.80→3.60

剩余全部定义为机器作业

车道4 / 6为地面标线

侧带6.80为连续机器作业

核心四梯19.60 / 净11.20

Q四位、八绕行口2.40

北南梯全内嵌; 西东不动

—— 日常人员 / 本区外侧电梯

- - - - - 应急人员 / 四向楼梯、核心禁入

- - - - - 机器物流 / 四向绕行入中央核心

浅绿: 连续机器作业地面 / 4m、6m为主车道


人员: 日常走外侧L; 紧急可沿纵段向外S

红线: 整个19.60m纵段应急隔离, 禁止绕入核心

最远中心 → 最近楼梯 66.95 m; 舱侧保守 77.70 m。

最远房SW-02 (另SE-03 / NW-10 / NE-11同值); 全部48室均有外侧及北/南两种疏散方向。

已验几何与路线; 960人疏散容量/时间、消防隔断构造、门扇扫掠仍待详设。另附整层3D Blockout。

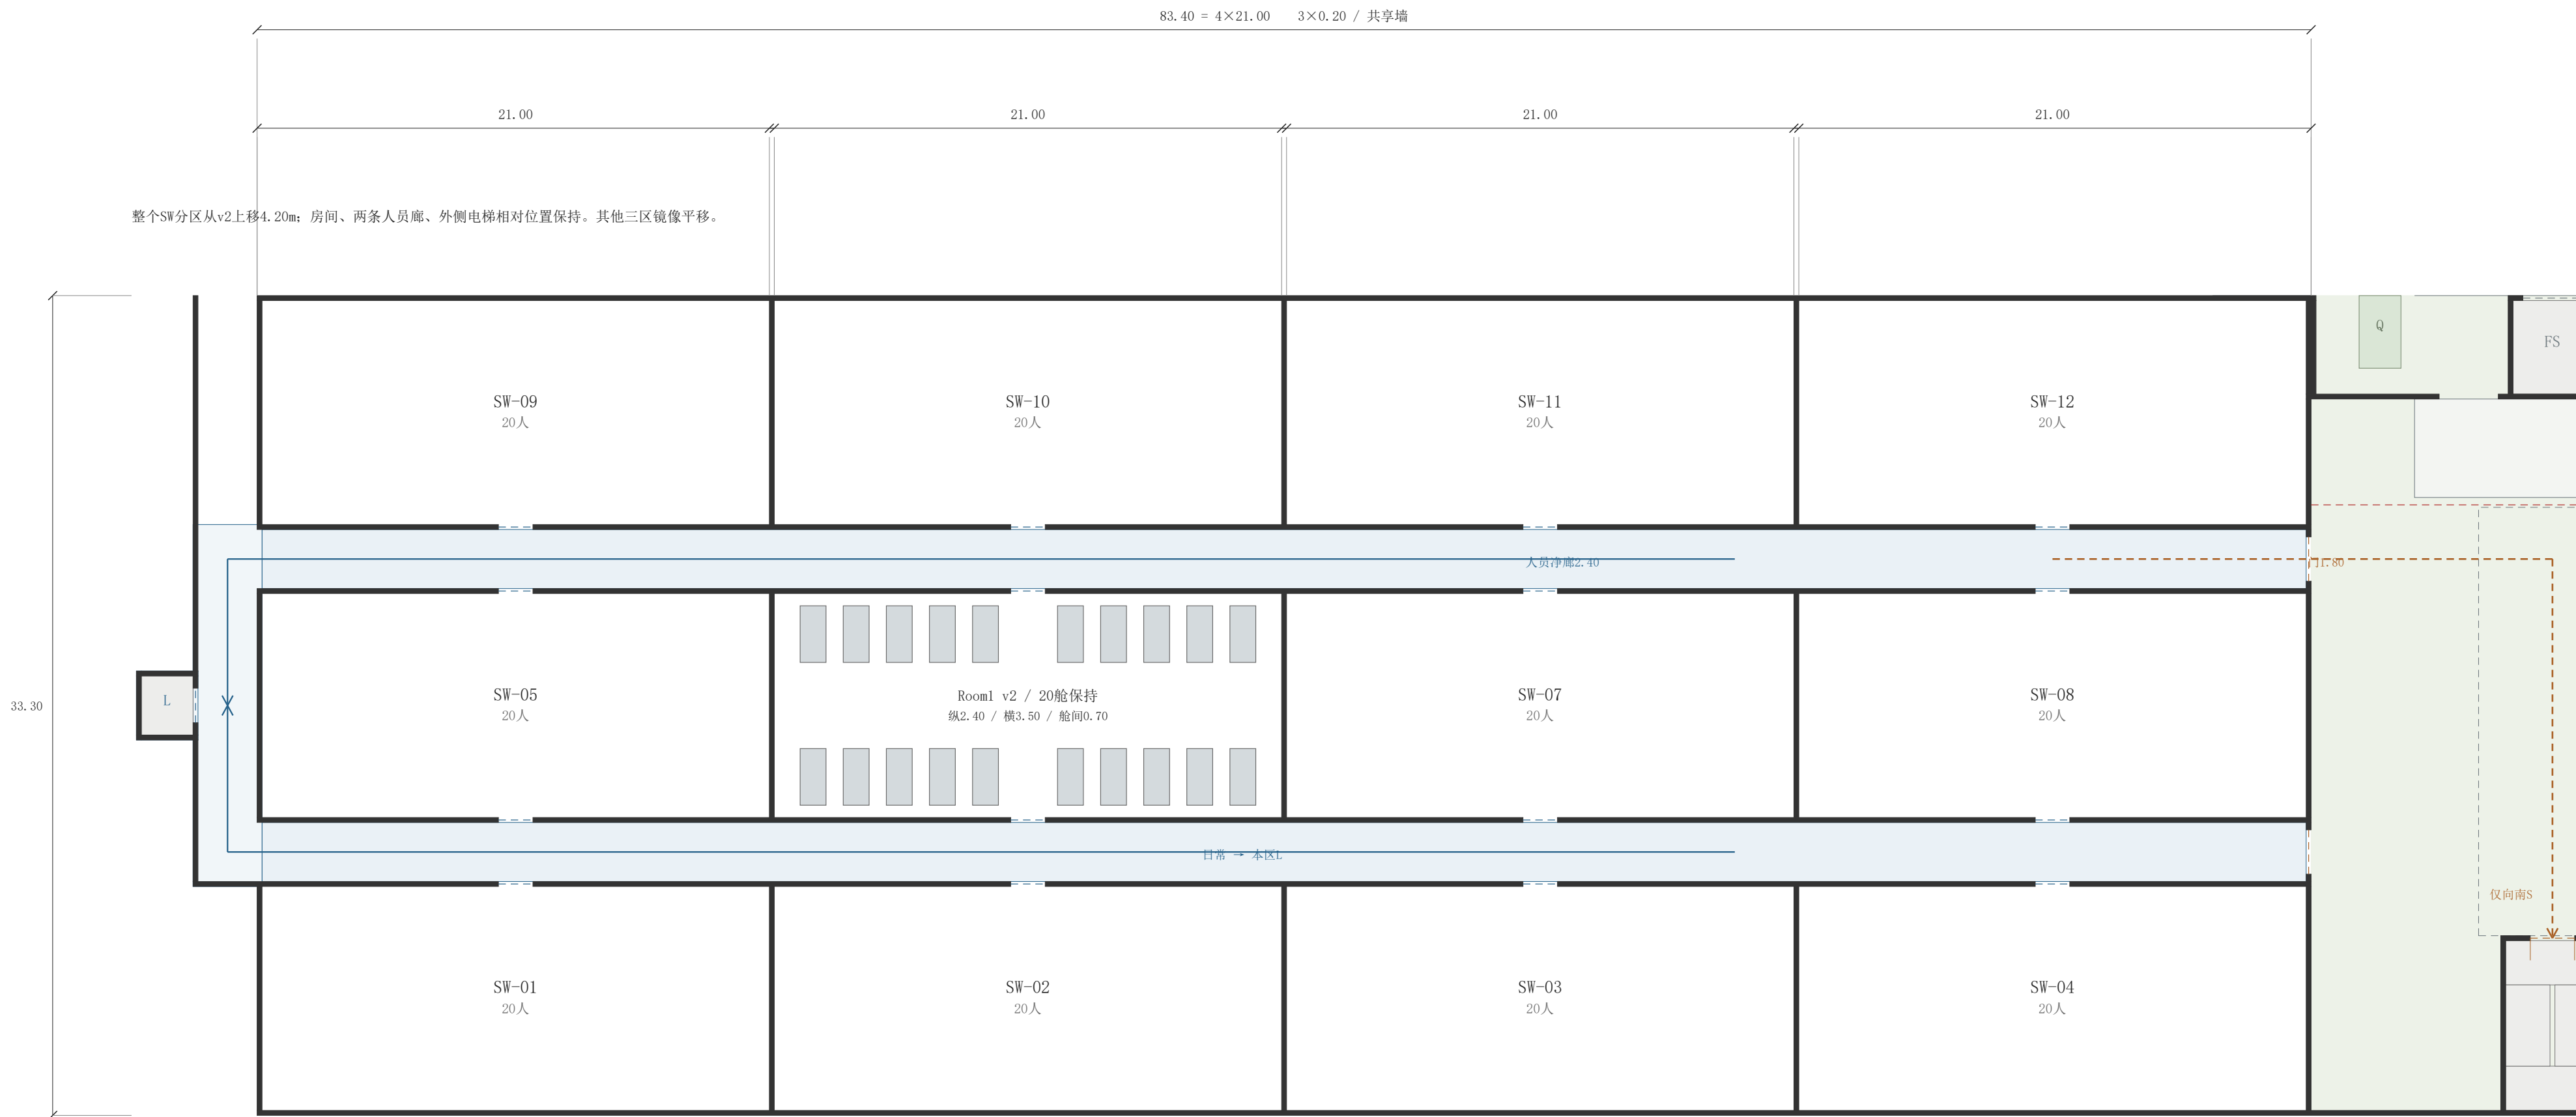

01 原点与平移: SW (0, 0) → (0, 4.20); SE (103, 0) → (103, 4.20)。

02 NW (0, 52.90) → (0, 48.70); NE (103, 52.90) → (103, 48.70)。未移动任何单间。


03 下区北边界37.50 / 上区南边界48.70; 二者间净11.20成为连续机器作业地面。

04 中央主车道4.00、边侧操作带各3.60; 沿线没有额外墙把车道切成喇叭口。

05 相邻舱室共墙0.20; 所有房间内部净20.60×9.10。中排双门; 外排单门, 门净1.40。

06 紧急开启内端门: 机器停运, 南段只向南楼梯; 核心全宽隔离。日常不走中央机器区。

01 北段 / 北楼梯（南侧镜像）

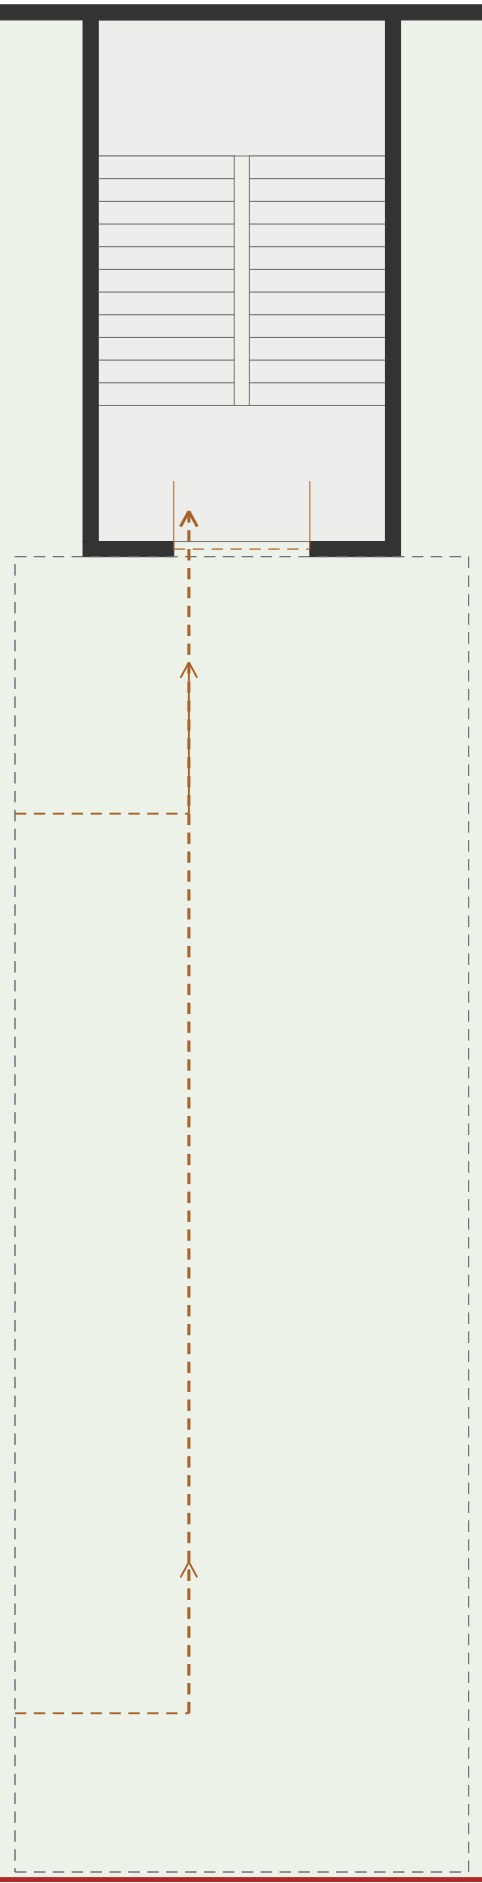

单门1.80，直入平台

北梯4.20×7.30 P

净梯段1.80 / 平台1.80

完全内嵌7.30 / 外伸0.00

24级 / 158.33mm级高

南北主车道地面净6.00


两侧各6.80机器作业

紧急：纵段全区停机

隔离线横跨整个19.60

人员只向外，不进核心

02 西/东楼梯：保持两门直入

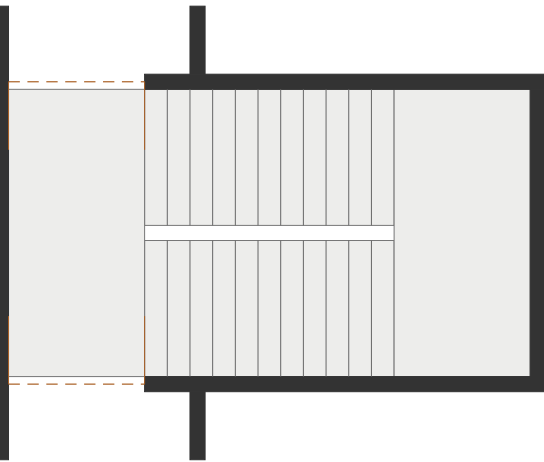

7.30×4.20；上/下各门1.80。


无第三门、无额外前室；东侧镜像。

红线是应急对人隔离边界。

需落实消防隔断构造与停机联锁。

图示门扇仅示意，扫描仍待验证。


03 原位保留四货梯与Q / 连续机器作业地面

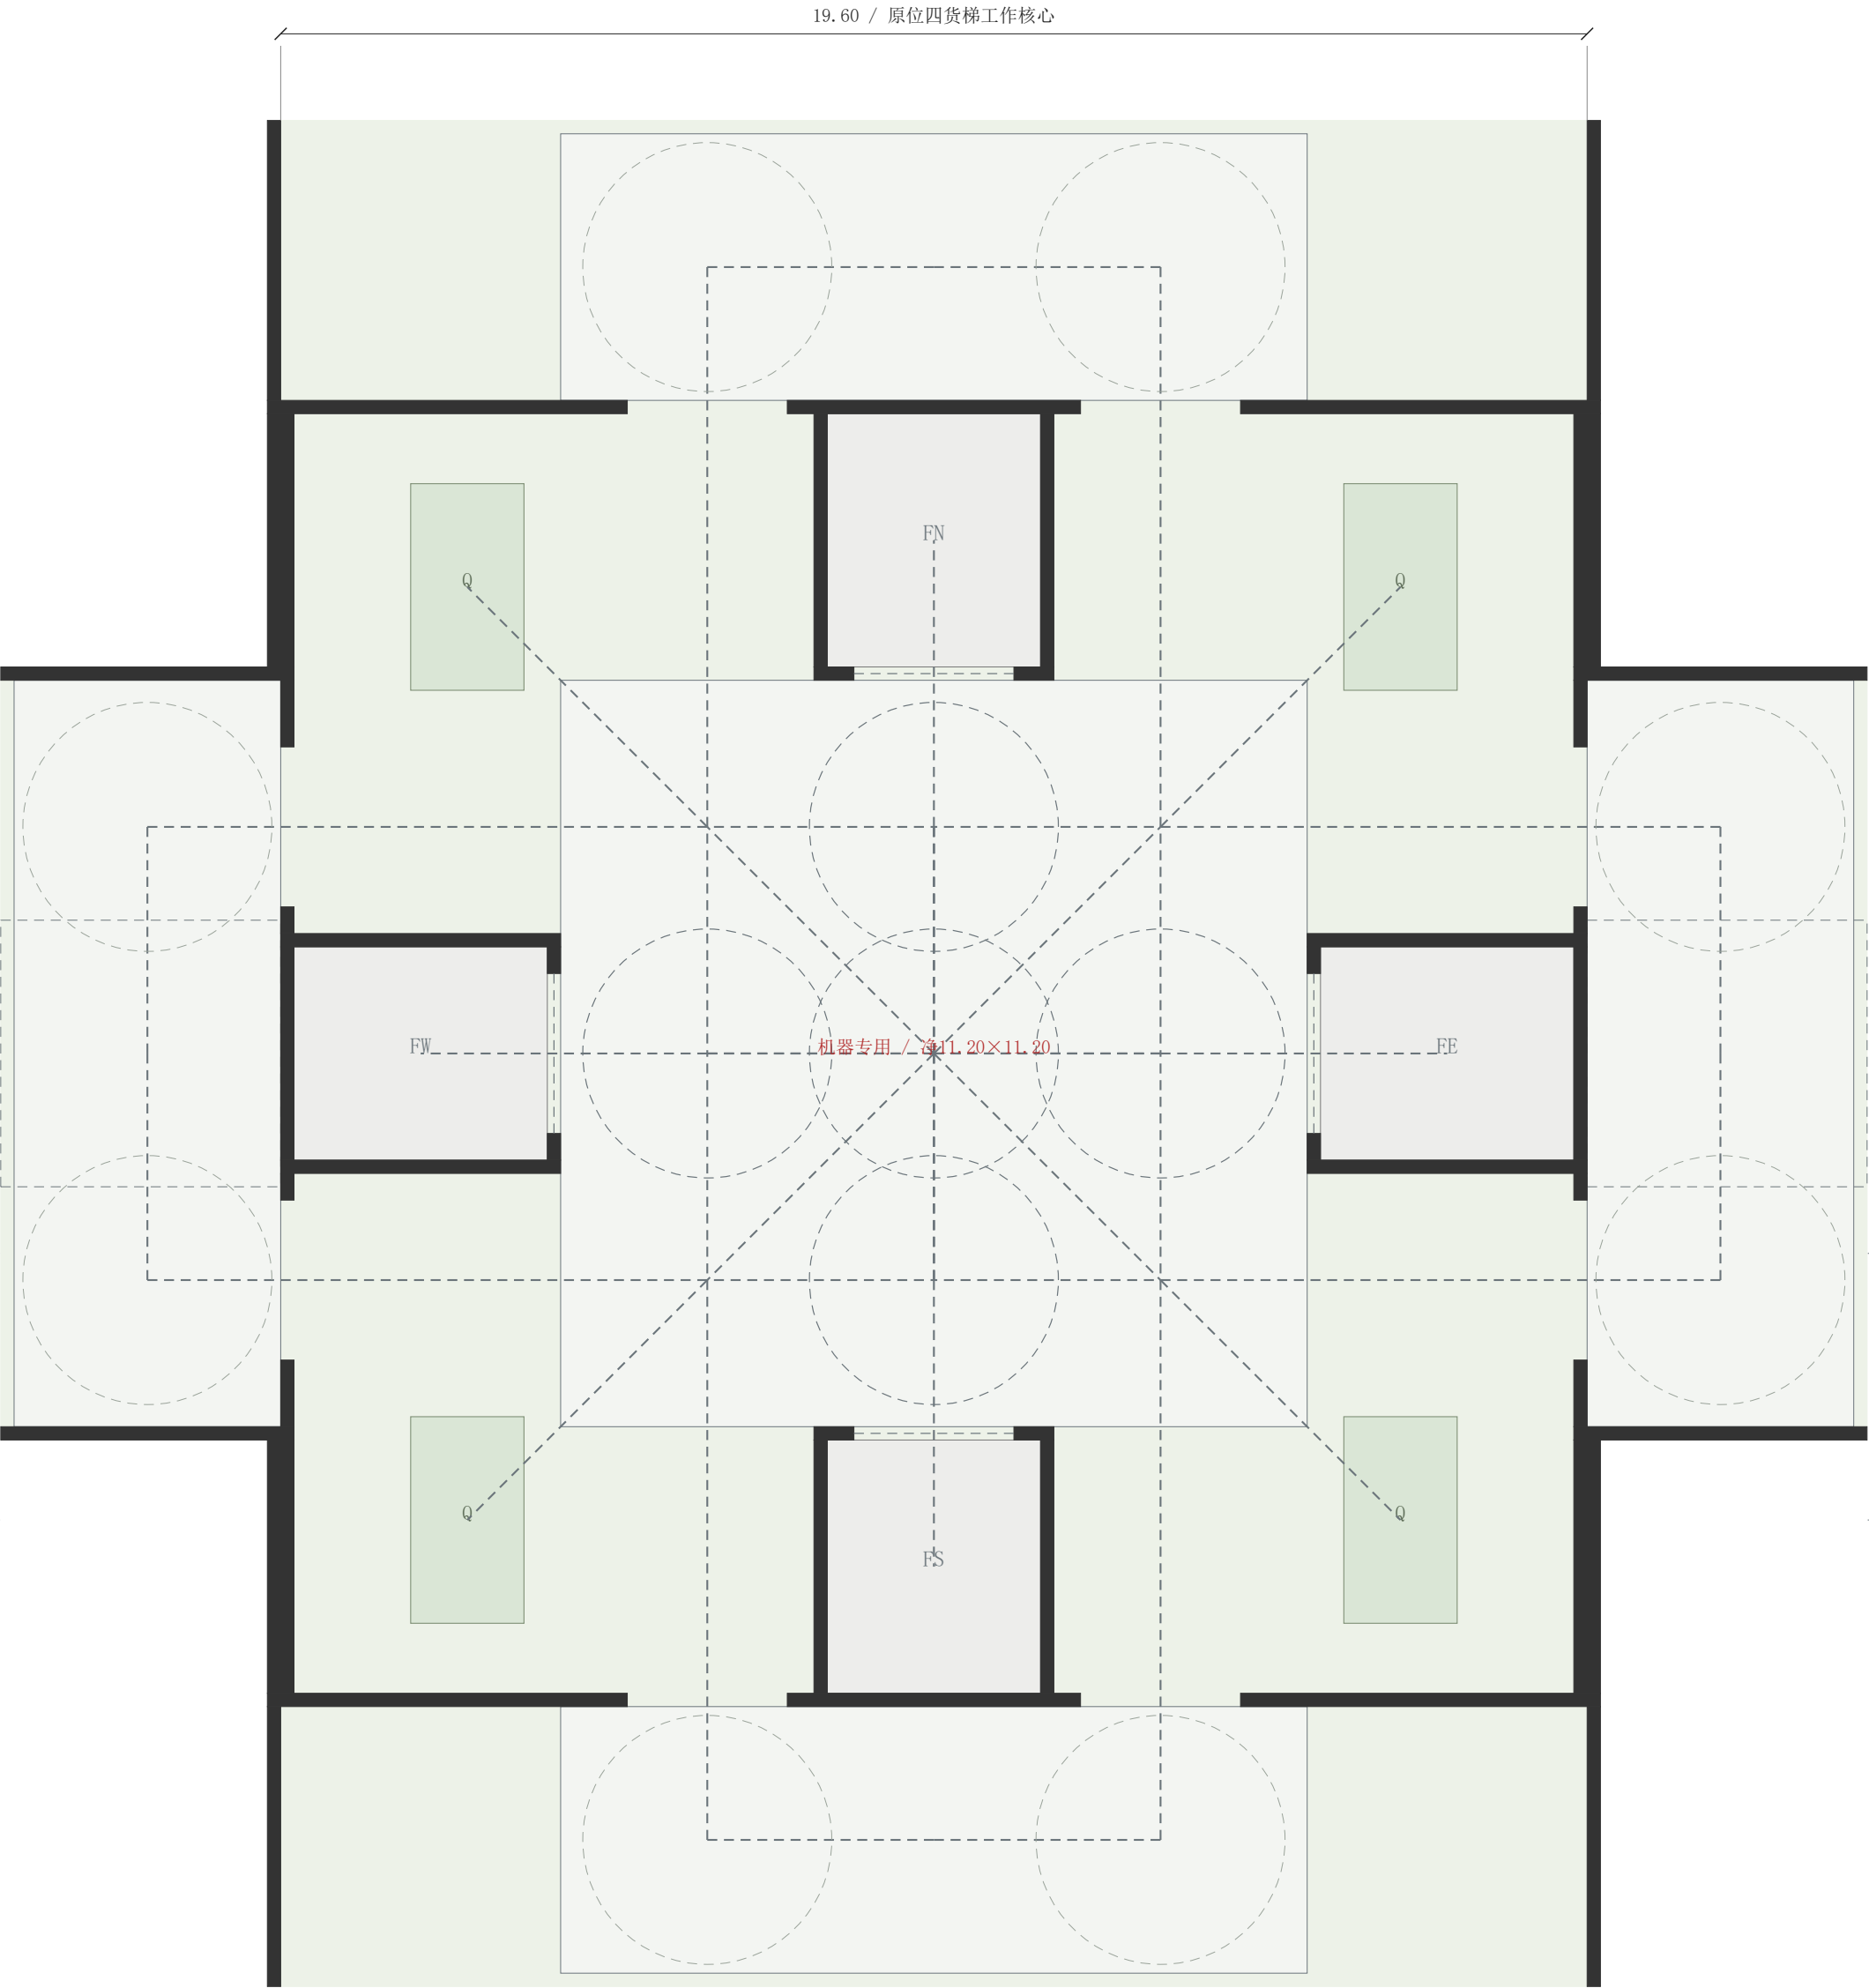


四梯净3.20×3.80 / 门2.40；八绕行口2.40；Q四个1.70×3.10。

回转圆03.736；四Q满位通行、逐台停梯绕行均经实体复核。


西侧节点 / 0E裁切前

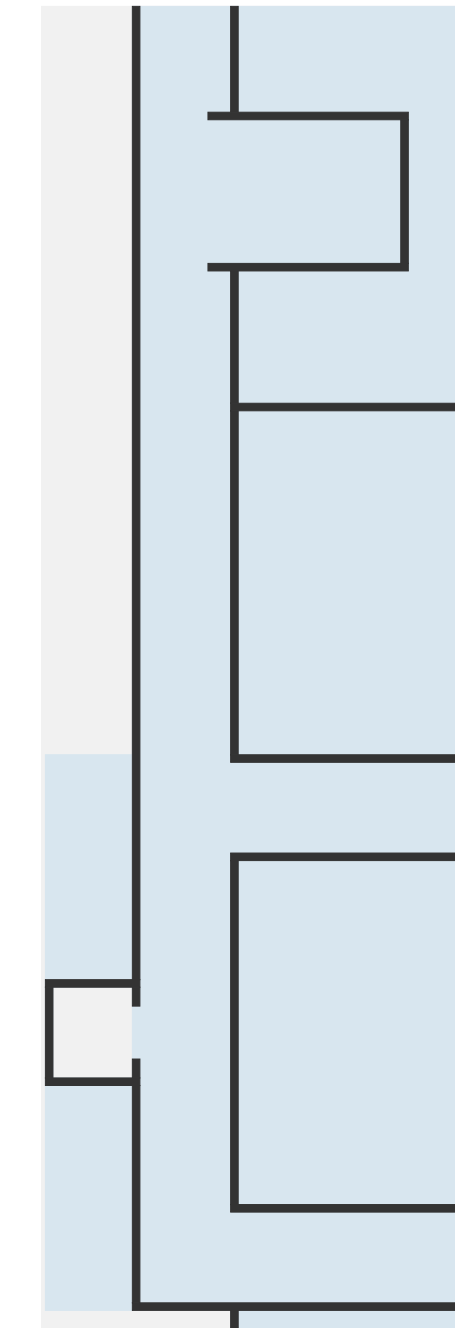

西侧节点 / 0F裁切后

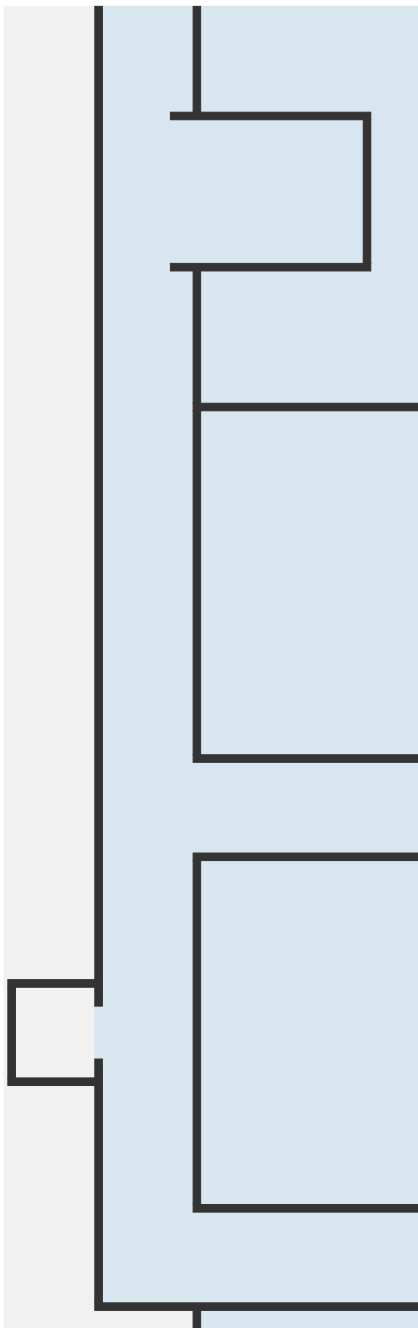

SW人员电梯井 / 修复后 / 1:50

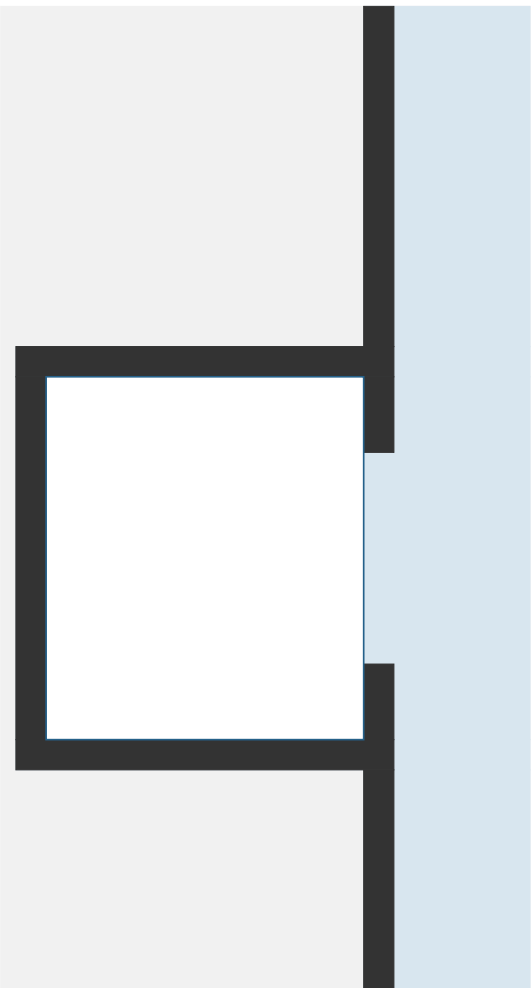


井道净洞2.10×2.40m；四处同法扣除。


0.20m井壁脚下支承保留；前室保留楼板。

独立轿厢地面参照隐藏，仅显示结构井道洞口。

南侧西墙闭合保持

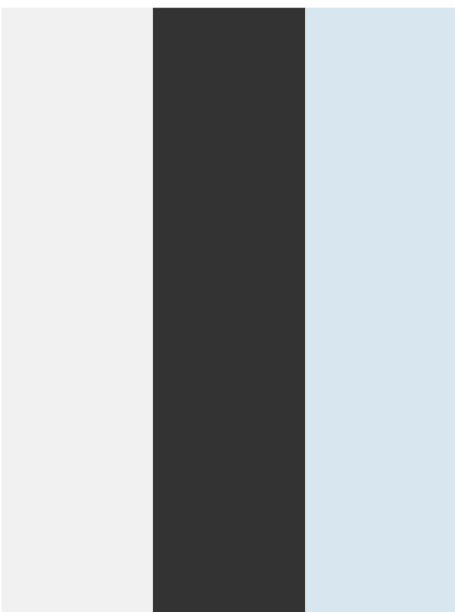

东墙镜像闭合保持 / 1:10

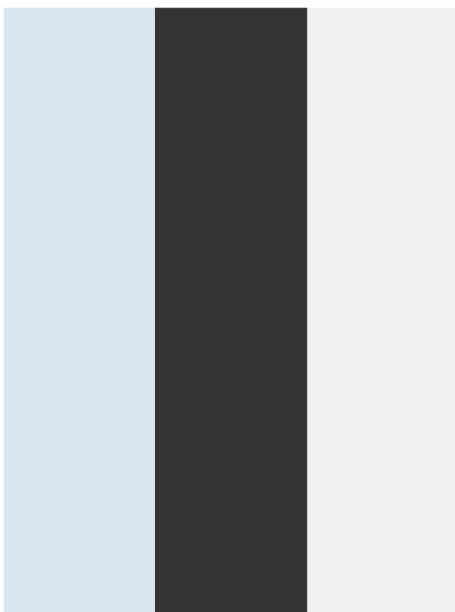

Y28.00-28.20的0.20m缝闭合；东侧镜像同步。

上轮两片补墙保留；本轮墙体与门洞完全不变。

蓝色为结构板平面；灰色为板外。

仅去除井道上下外伸板；连接廊净宽2.40m保持。

四节点镜像裁切，合计删除109.48平方米楼板。

冻结范围：48室 / 960舱、四分区、人员电梯、四楼梯、

四货梯、Q等待位、机器核心、外包和疏散拓扑均保持。

本页平面源与3D结构板共用同一floor_cells几何。

3D仍为单层空间灰模；高度与结构做法为暂定值。