



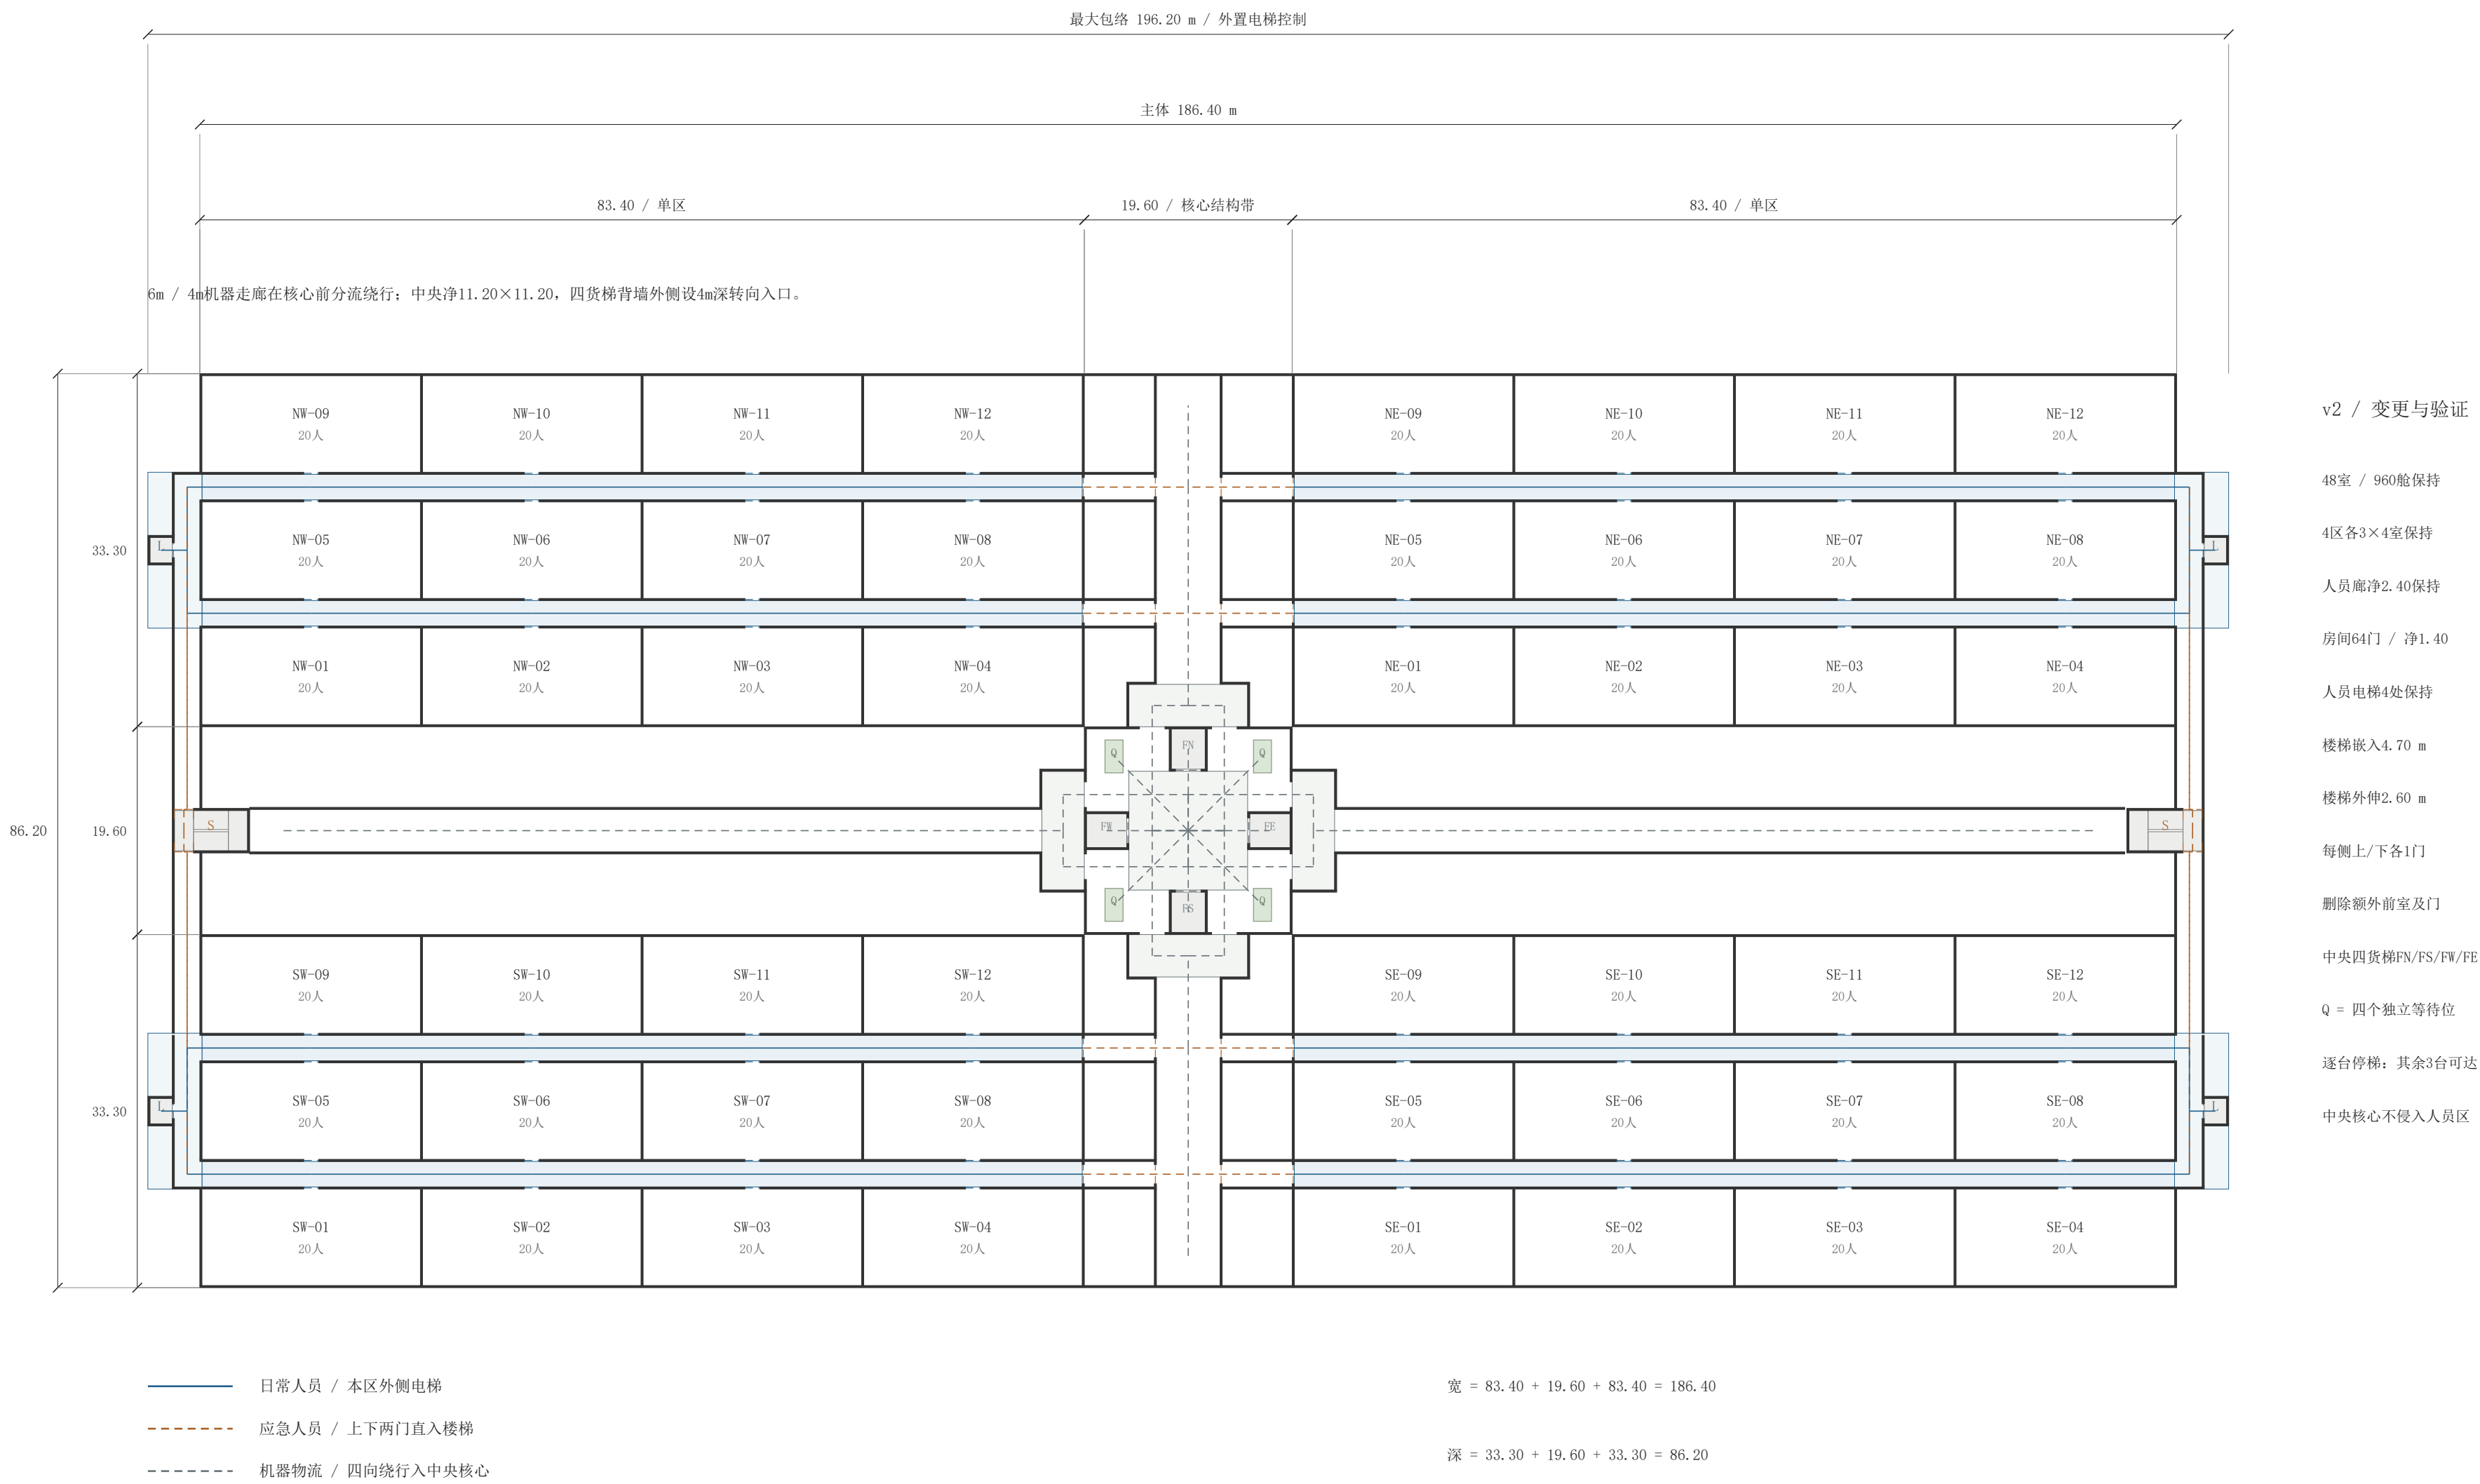

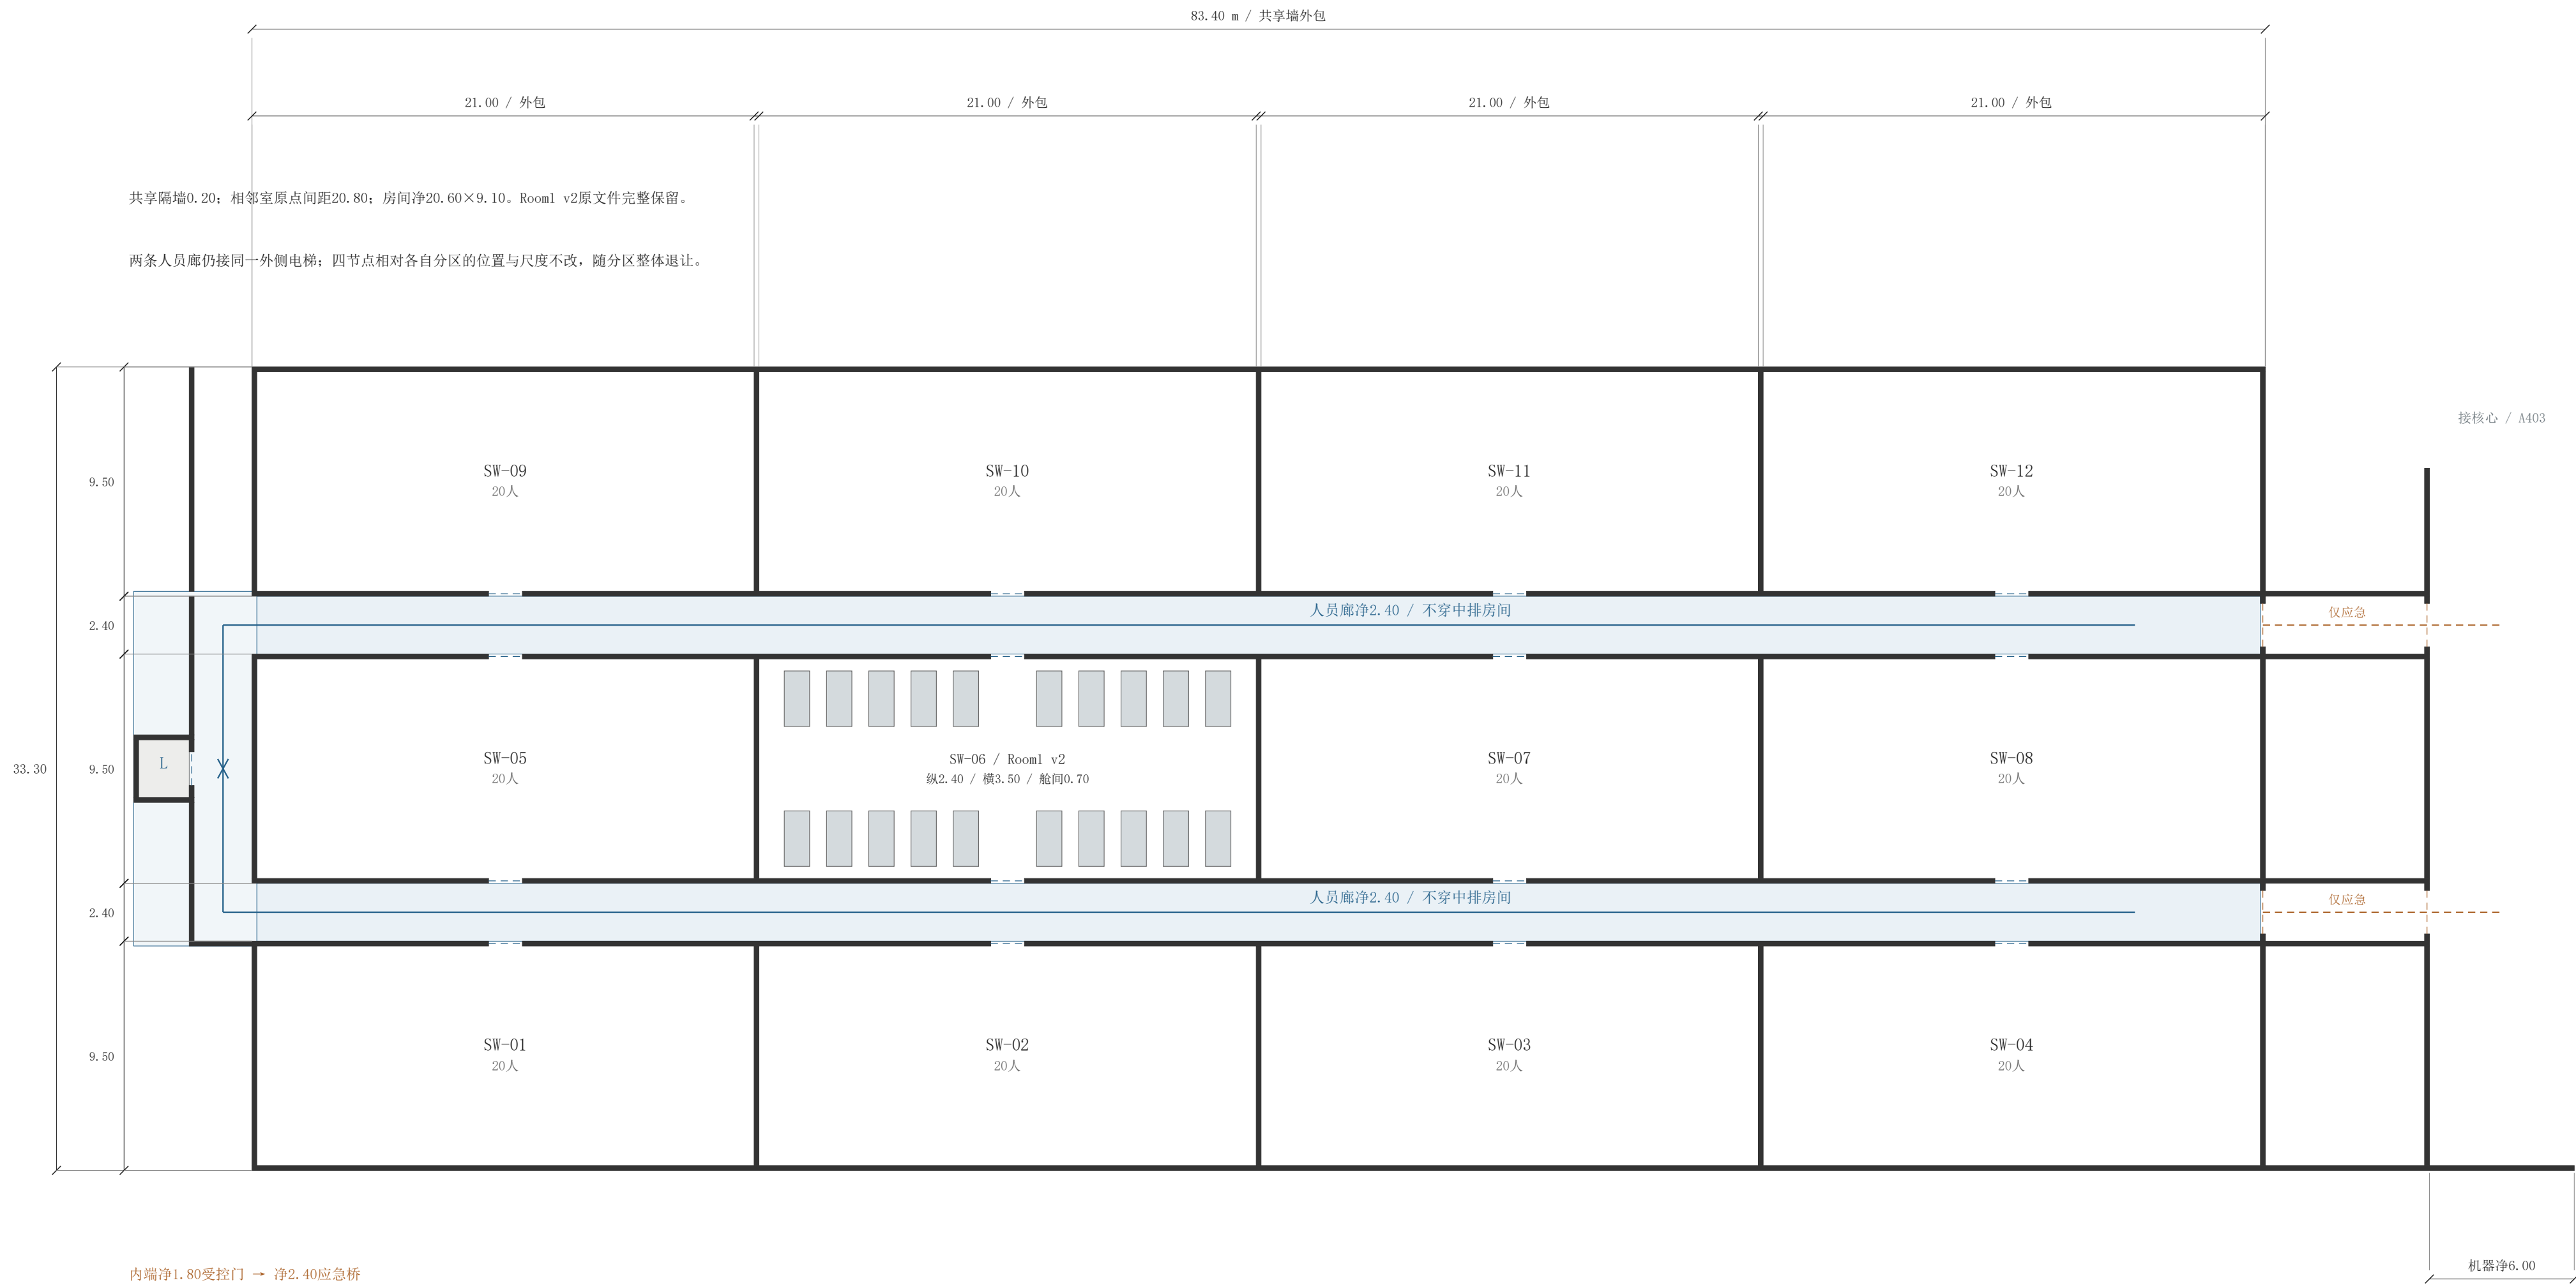


中排16室仍各有两扇1.40m人员门；普通流线不把休眠室作为公共穿行捷径。

外侧连接带继续通向本侧楼梯；上下区只通过楼梯的两道防火门相连，日常保持隔离。

6m脊柱两侧退让余量不定义新功能；跨余量的连接桥仅在应急状态使用。


四区同构镜像：单室21×9.5、20舱位置、2.4纵轴、3.5横廊、0.7操作间距均沿用既有模型。

01 左消防楼梯 / 半外置、无额外前室

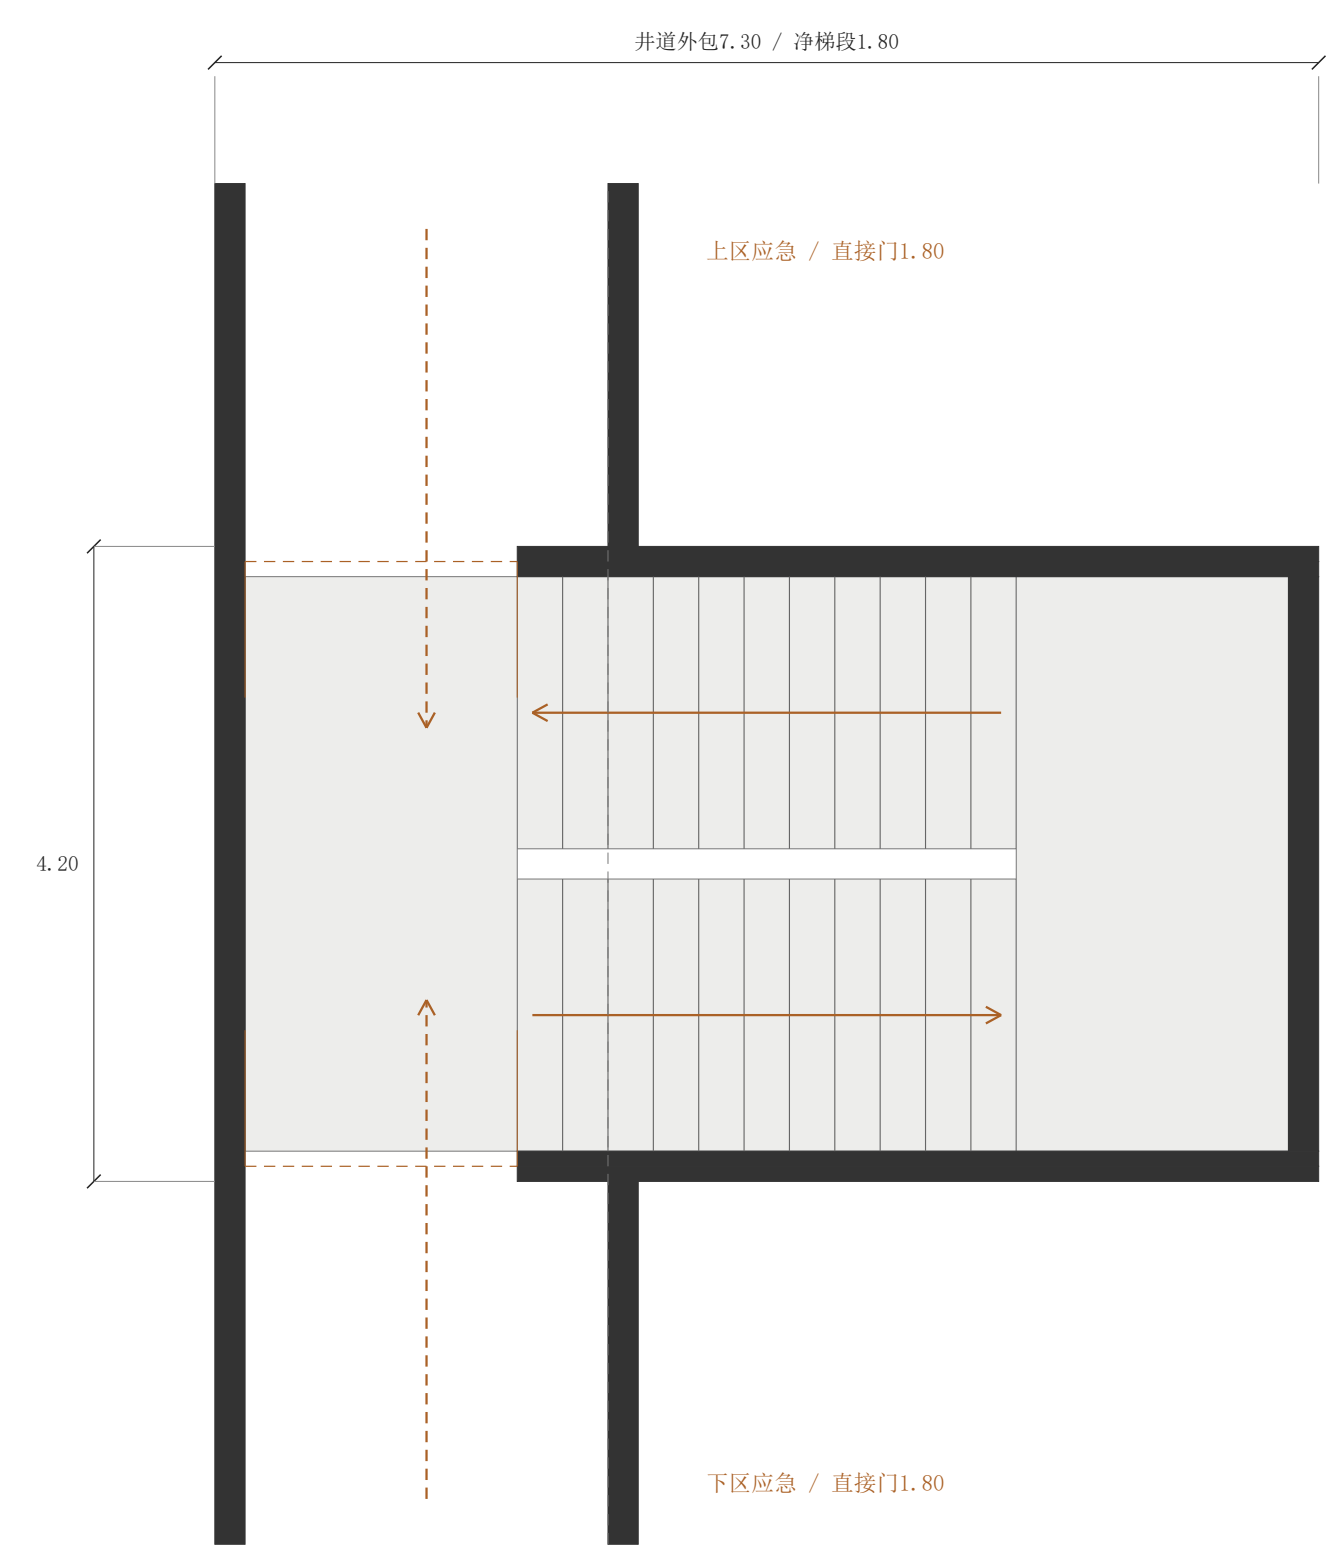


梯段净1.80 / 平台1.80 / 跑长3.30 / 踏步300mm P: 右侧镜像。
内嵌4.70 / 外伸2.60; 虚线X=0; 层高3.80 / 24级 / 级高158.33mm P。
中央净11.20×11.20 / 回转圆 Ø3.736m / 四个独立等待位Q。

02 四个人员电梯 L 与楼梯 S / 中央核心相对位置 (示意)

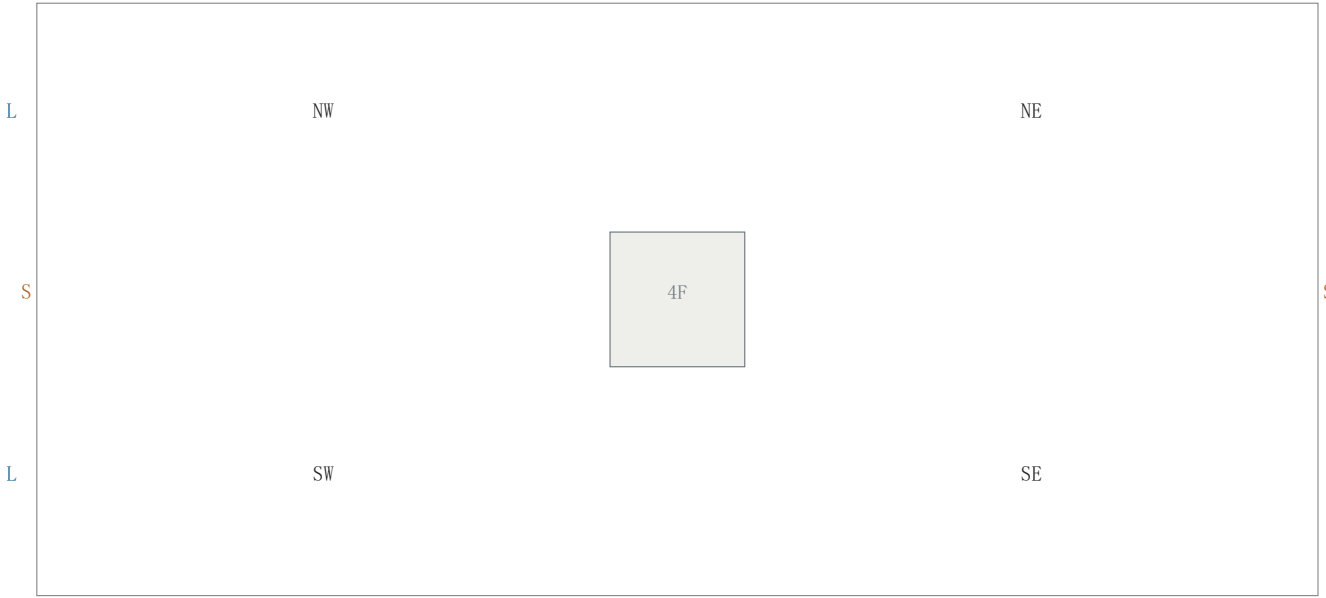

03 中央四货梯 / 原位回转、双侧绕行、四等待位

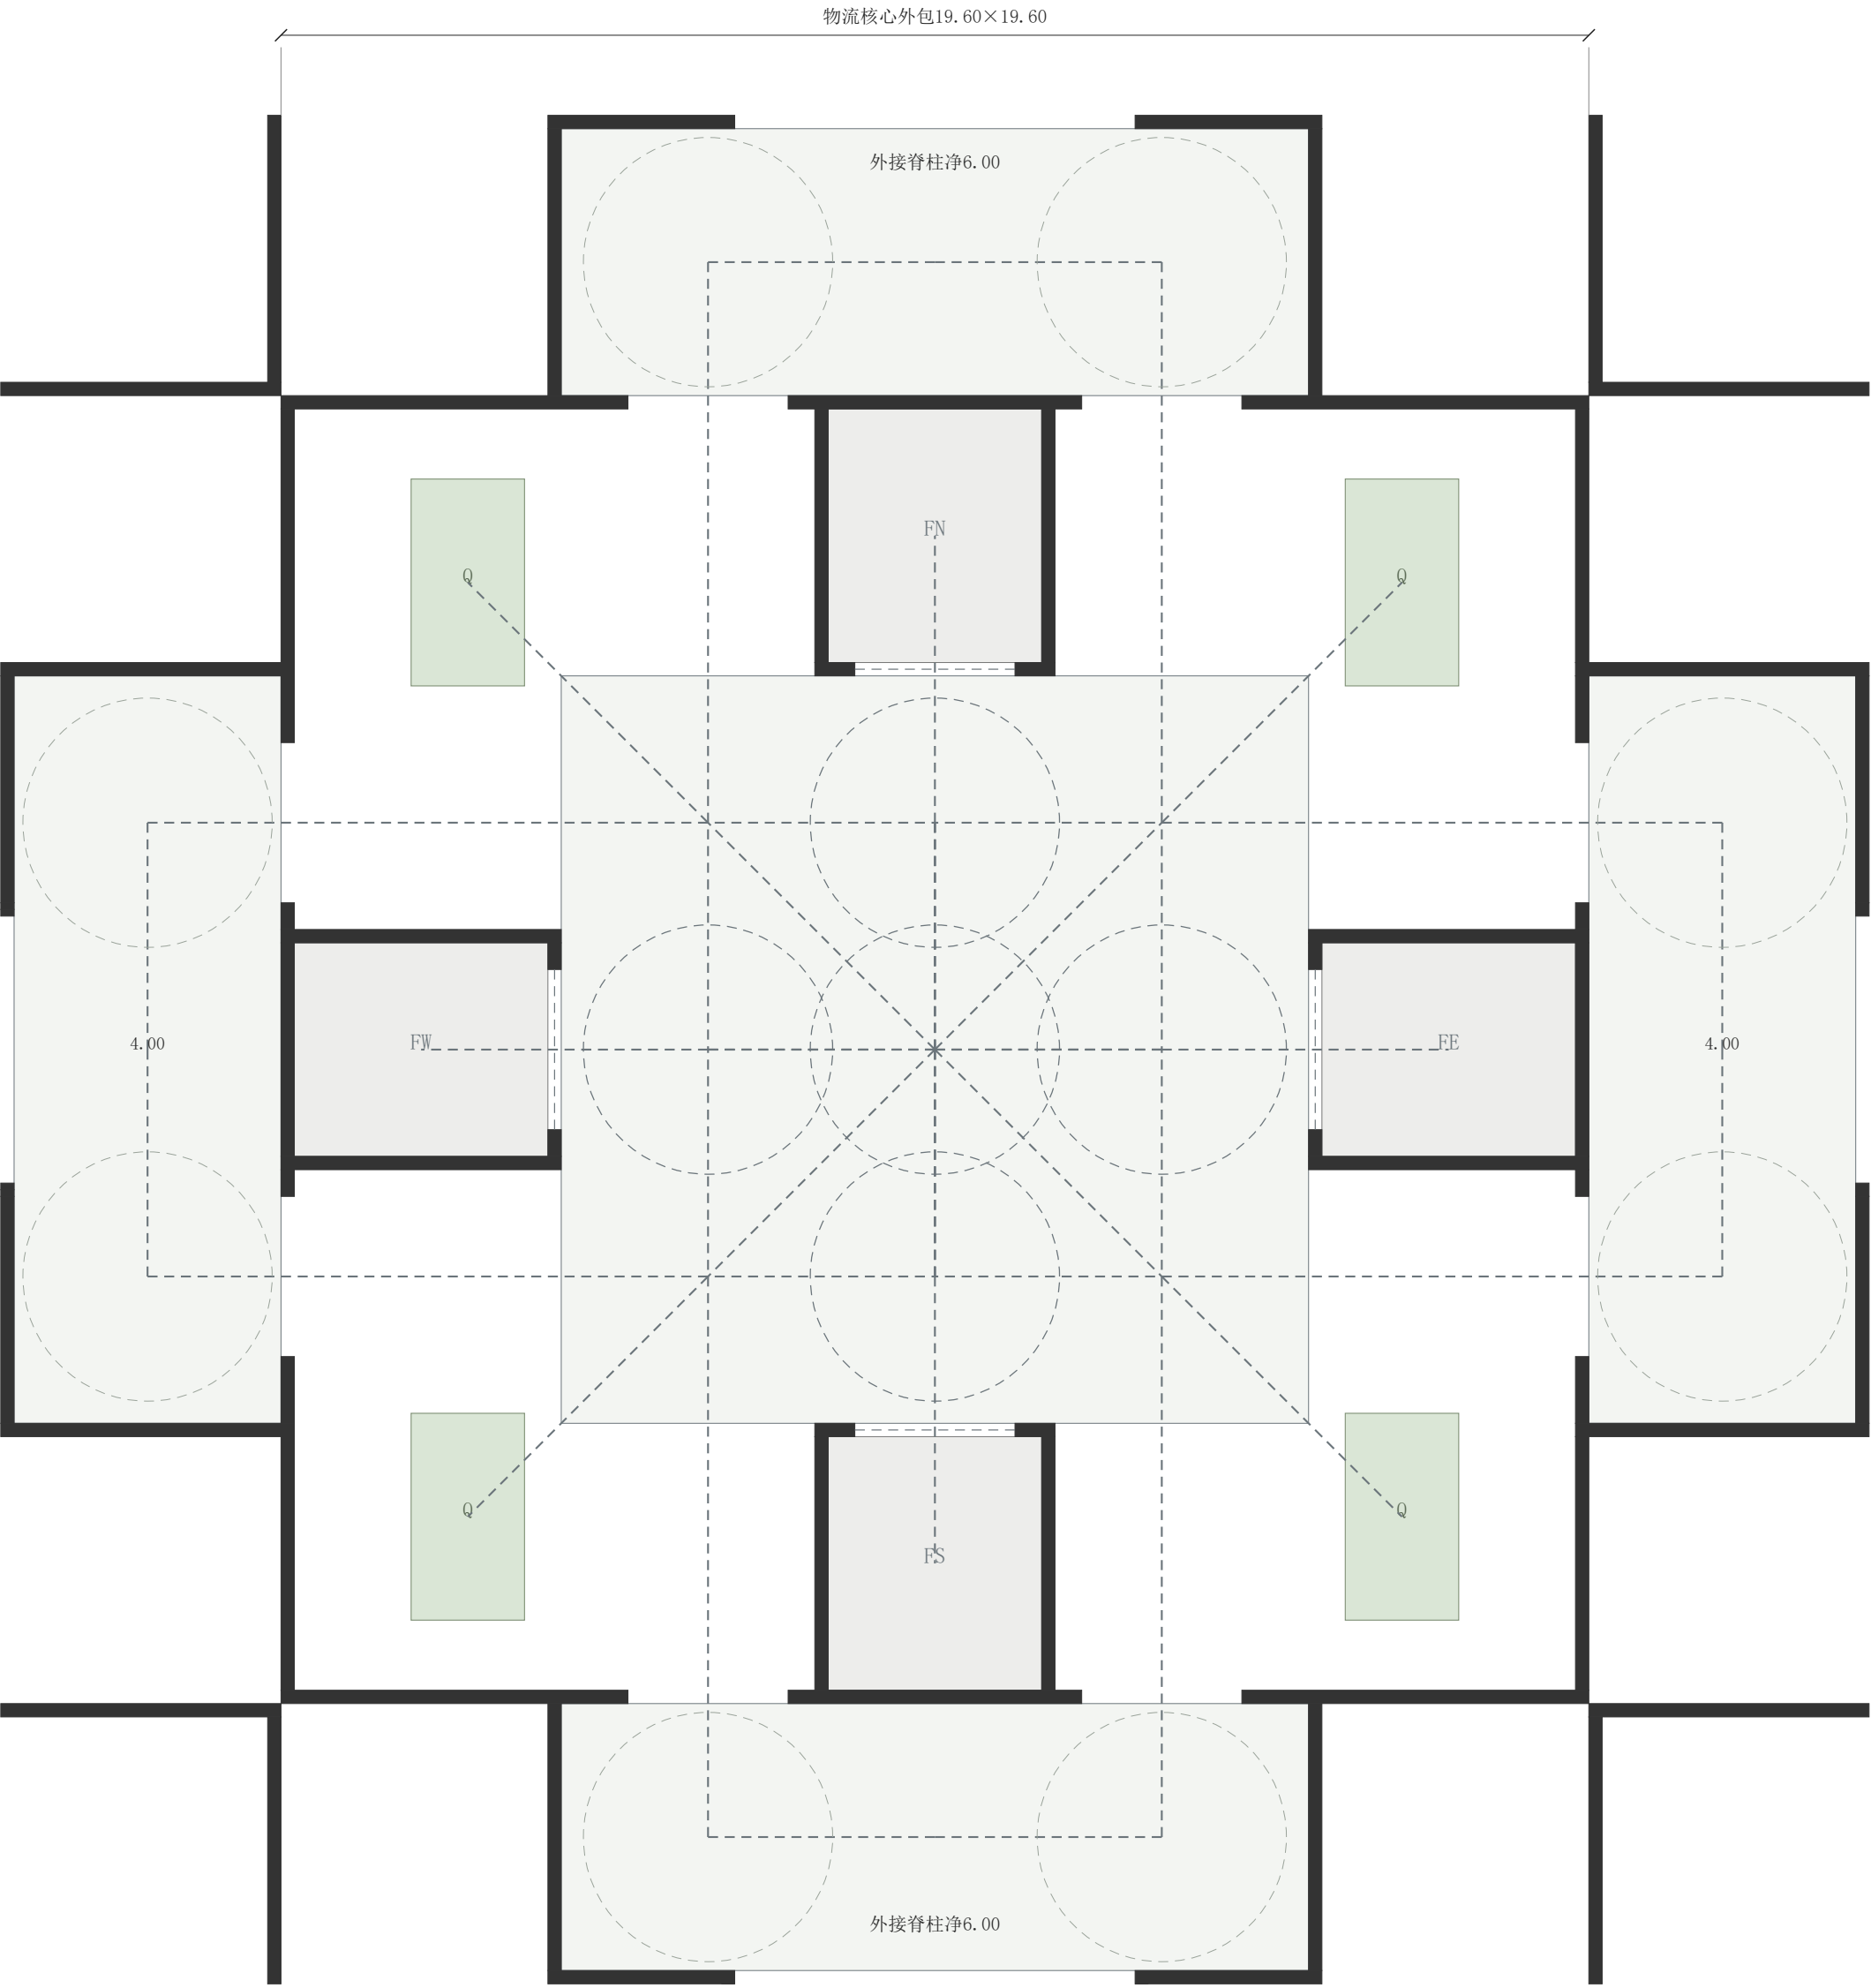

四梯净3.20×3.80 / 井道3.60×4.20; 门2.40; 背部双侧绕行开口2.40。

Q: 整车1.70×3.10等待位; 4m入口转向, 单梯停用后其余3梯均可达。