


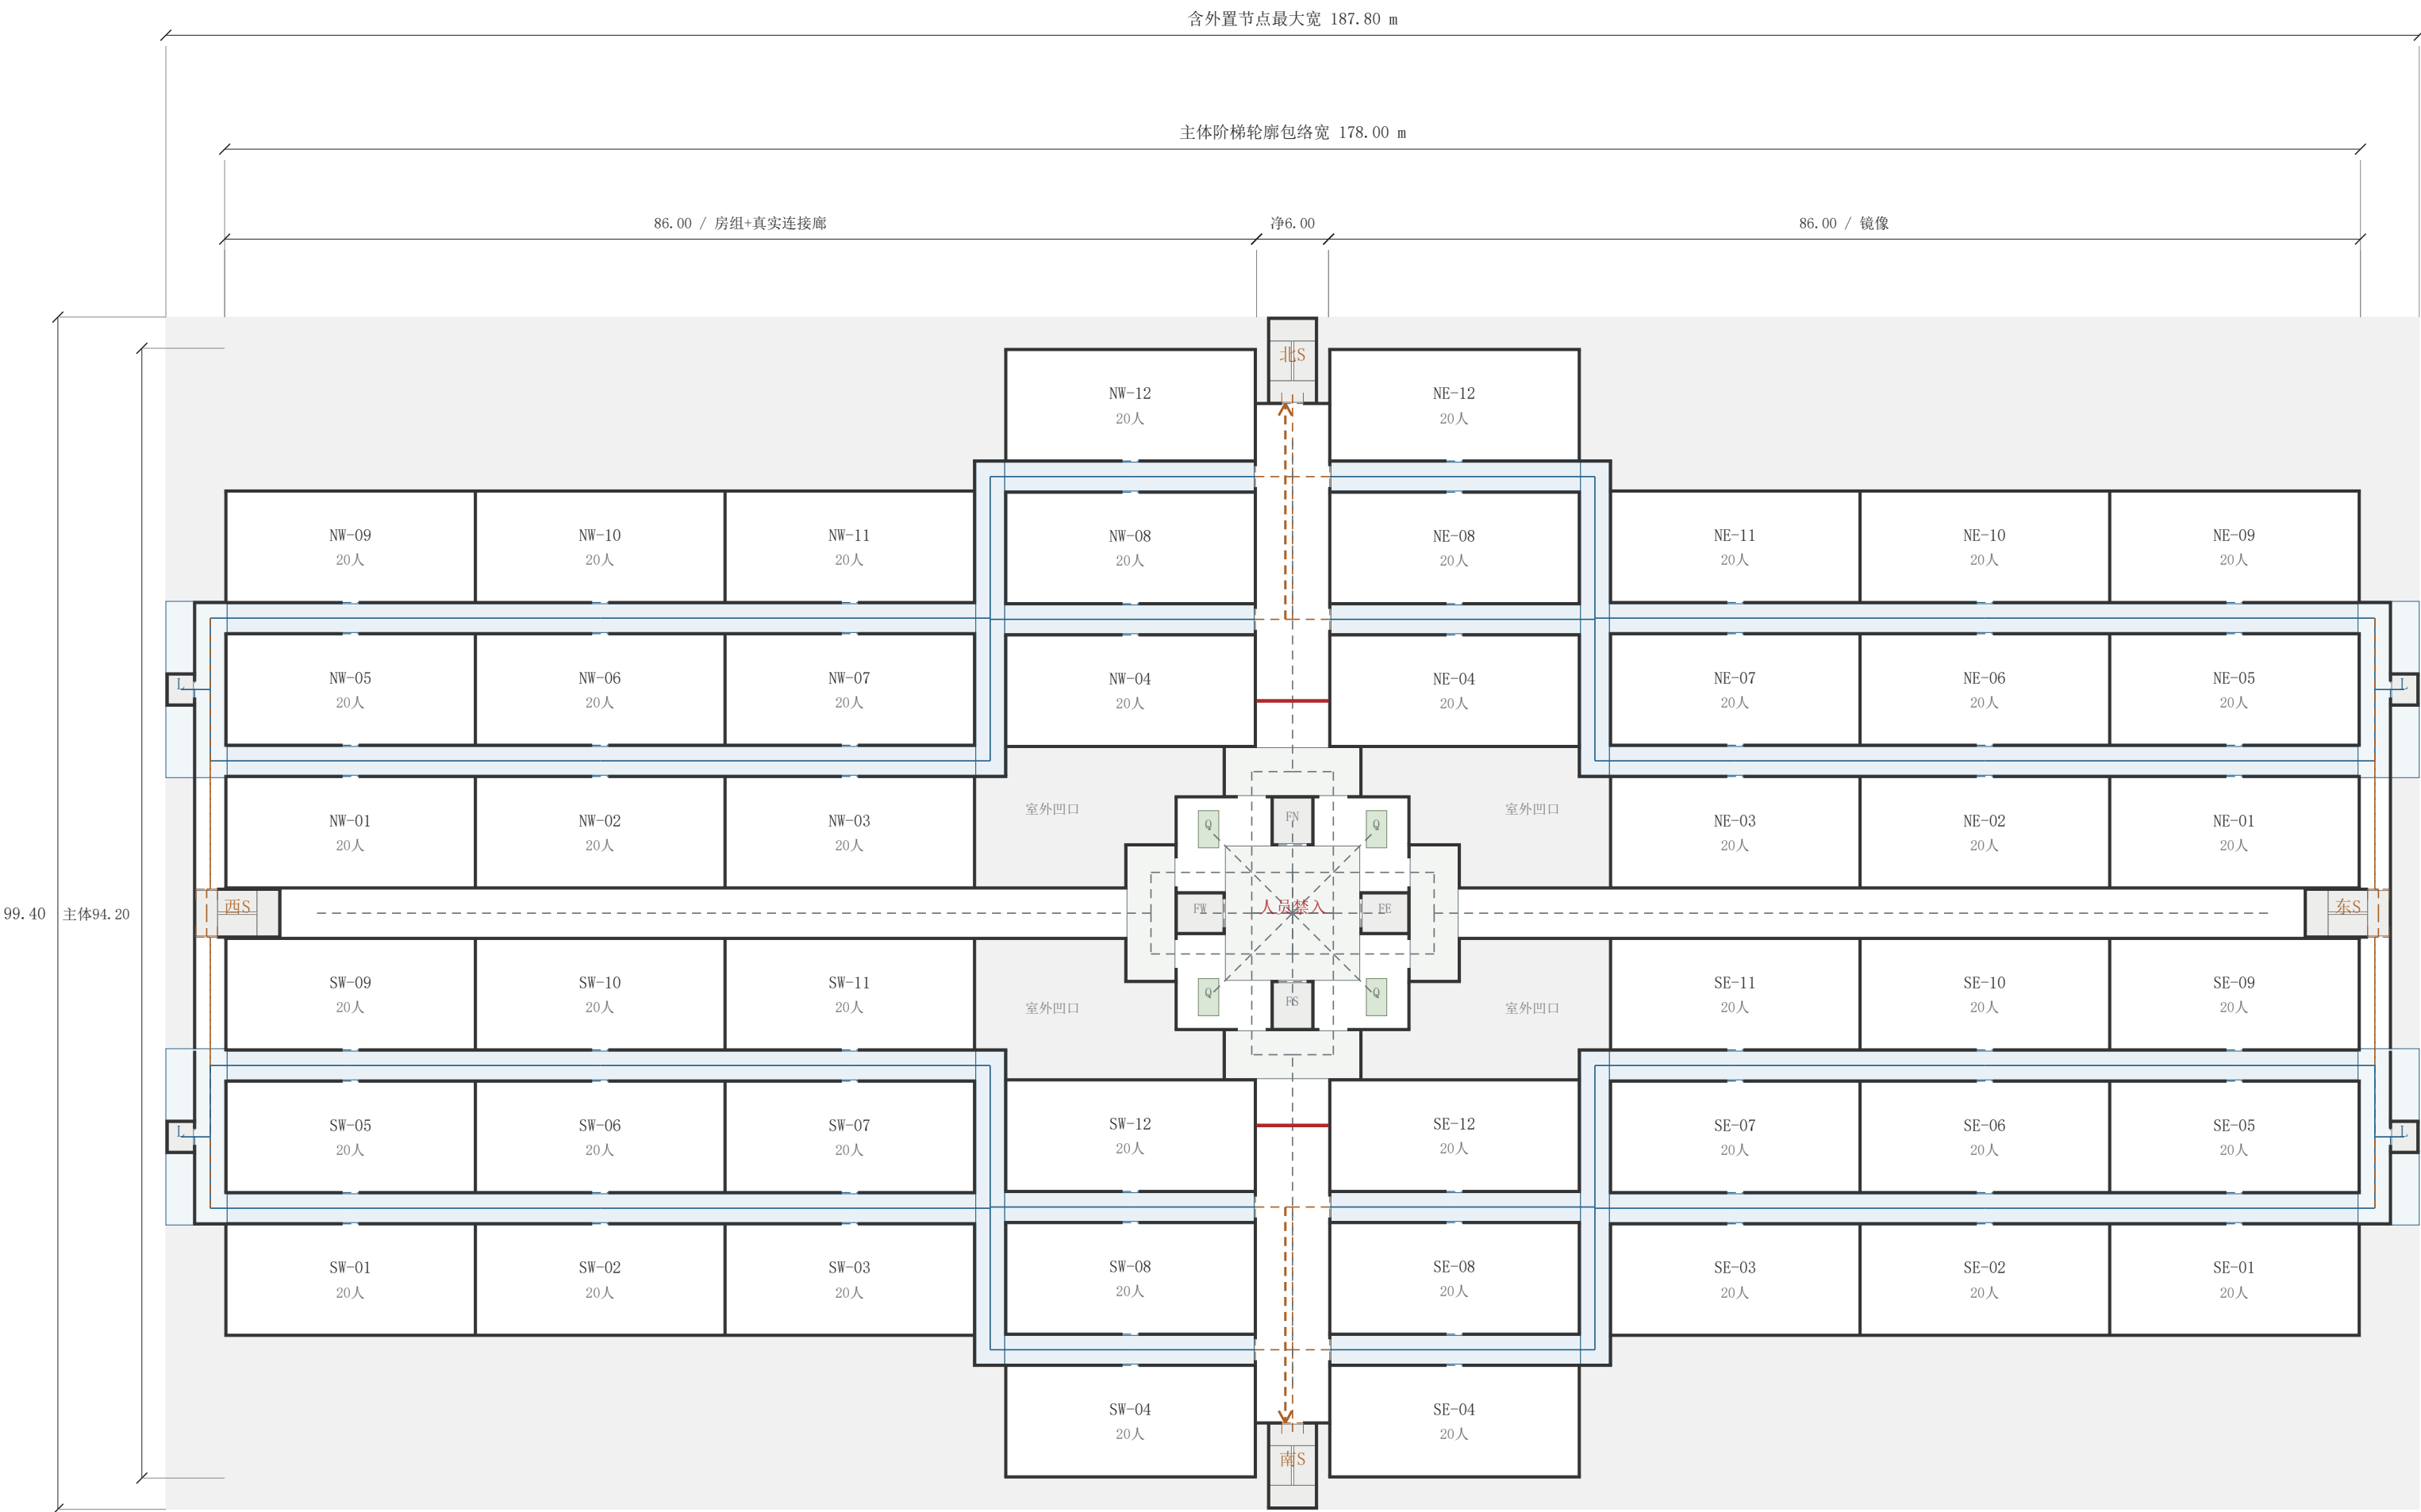

v3 / 验证与反算


- 48室 / 960舱保持
- 每区3排×4室保持
- 每区一台人员电梯：接受
- 外三列共享外包62.60
- 内一列外包21.00
- 真实人员连接廊净2.40
- 内列局部纵向错台11.80
- 普通机器段：纵6 / 横4
- 核心19.60仅在中央
- 转运净11.20×11.20
- 西/东各2门；北/南各1门
- 紧急：北段向北/南段向南
- 纵向段停机：核心对人封闭
- 浅灰为建筑轮廓外，不是空白带

- 日常人员 / 本区外侧电梯
 - 应急人员 / 四向楼梯、核心禁入
 - 机器物流 / 四向绕行入中央核心
- 宽：62.60+2.40+21.00+6.00+镜像 =178.00
- 深：33.30+4.00+33.30+2×11.80 =94.20

最远中心 → 最近楼梯72.25 m；舱侧保守83.00 m；较v2均减少40.50 m（中心35.92%）。

最远房SW-11（镜像同值）：经本区外侧人员廊到西梯。48室均有外端/内端两种疏散方向。

容量/时间与防火细节仍待验证：人员电梯按未来高速可靠、分批进入假设接受，不阻止本轮推进。

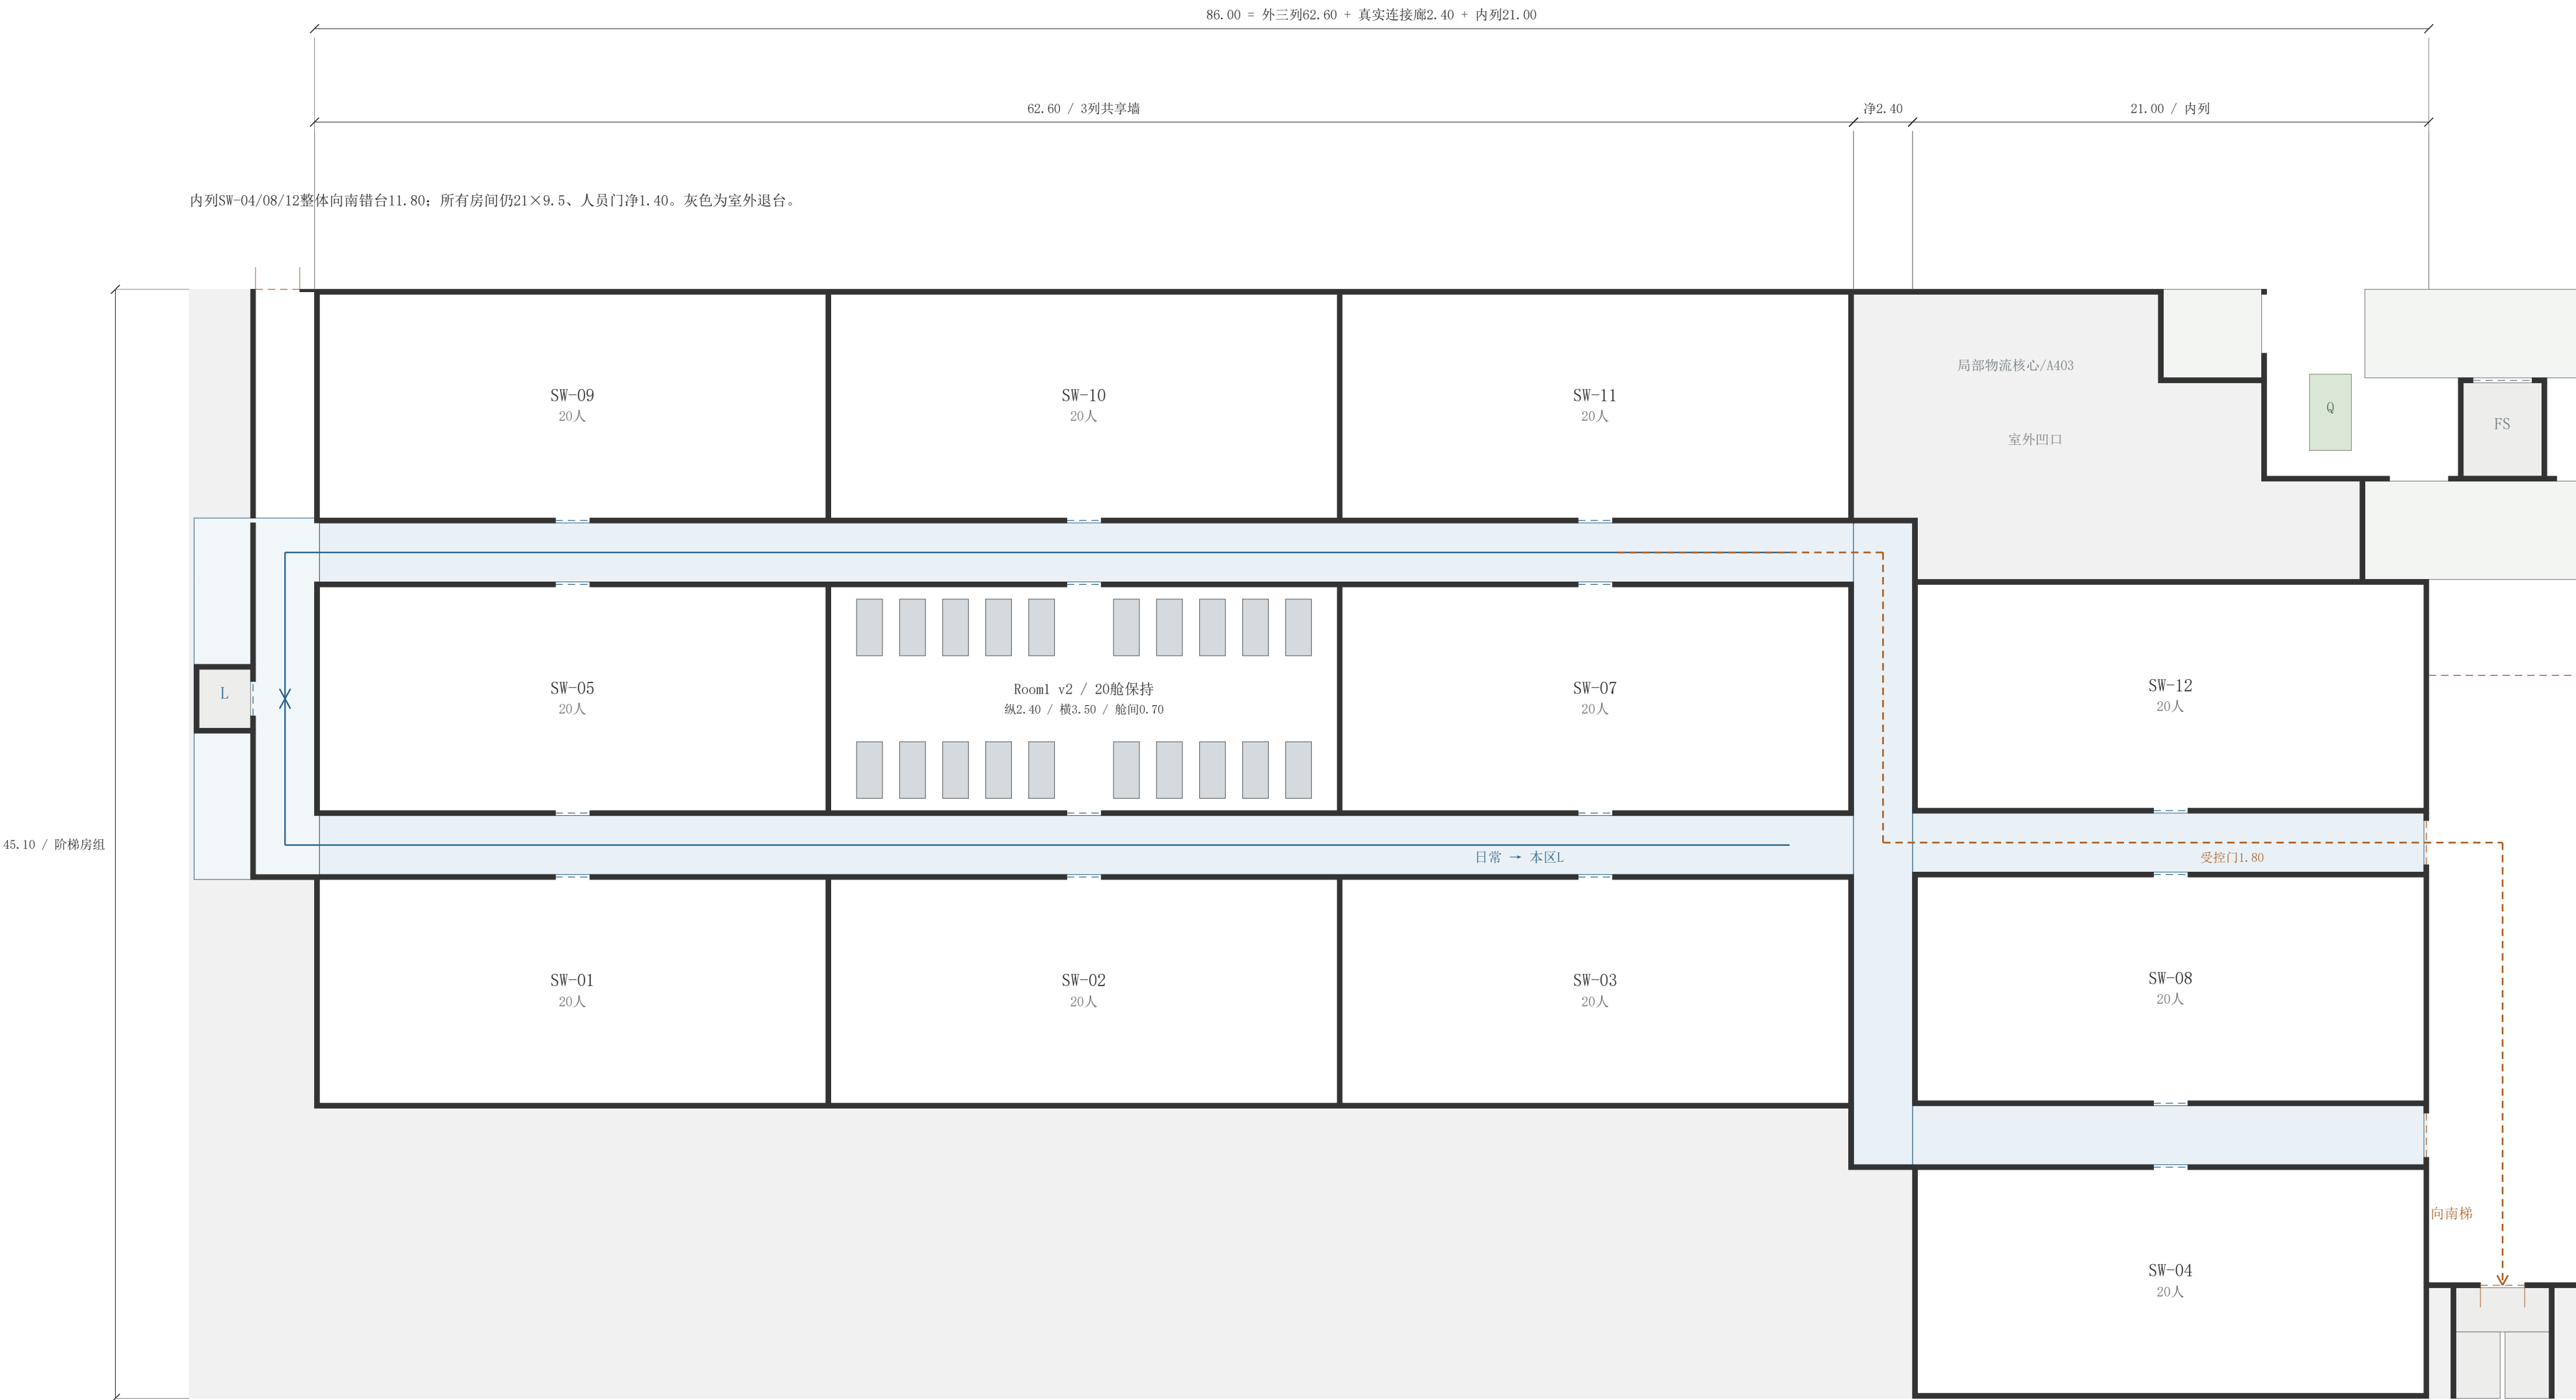


两条外段人员廊通过真实2.40m竖向连接廊接入错台内列；全程不穿休眠室。

紧急门平时关闭；应急开启后进入南半纵向通道，只向南。核心前人员隔断关闭，机器人停运。

区内电梯位置/轿厢/井道尺度保持相对外三列；其他分区按纵向、横向镜像，容量不变。

01 北段/北楼梯（南侧镜像）

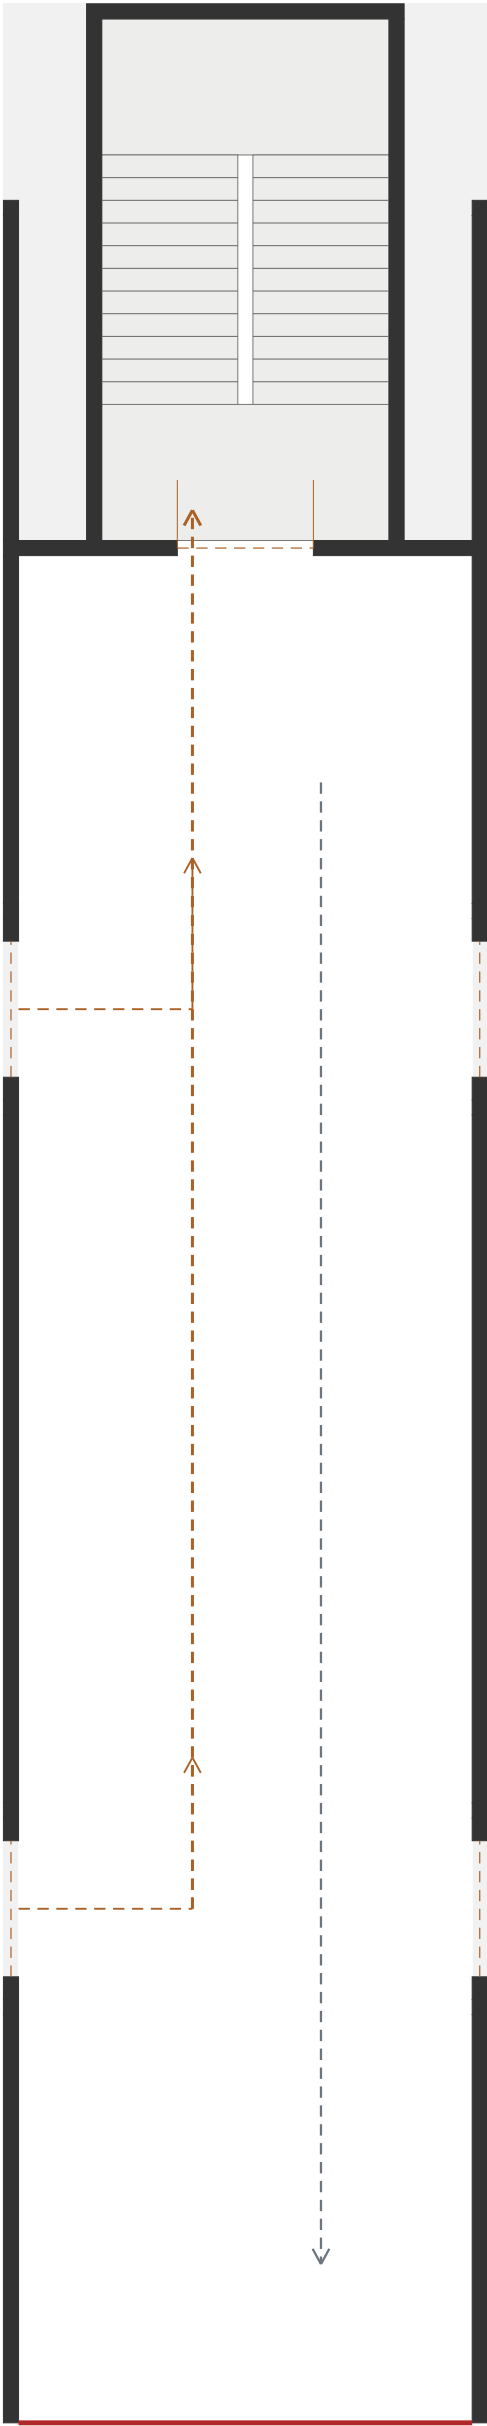

单门净1.80直入，无前室

北梯外包4.20×7.30 P

净梯段1.80 / 平台1.80

内嵌4.70 / 外伸2.60

24级 / 级高158.33 mm

机器正常：往返物流


紧急：本段机器人停运

人员门开，只向外楼梯

核心边界关闭，禁止向内

南梯与南段关系镜像

02 西/东楼梯：保持两门直入

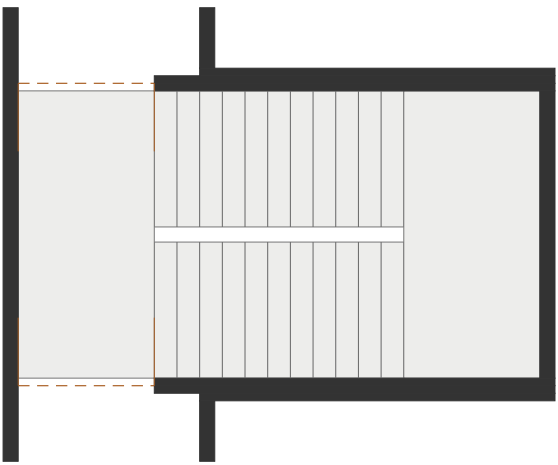

西/东井道7.30×4.20；右侧镜像。


上/下各1门，无额外前室或第三门。

红线：应急时对人关闭；

常态机器门可用，人不得穿核心。

门扇扫掠/消防等级仍待详细设计。

03 几何中央四货梯 / 净转运11.20×11.20

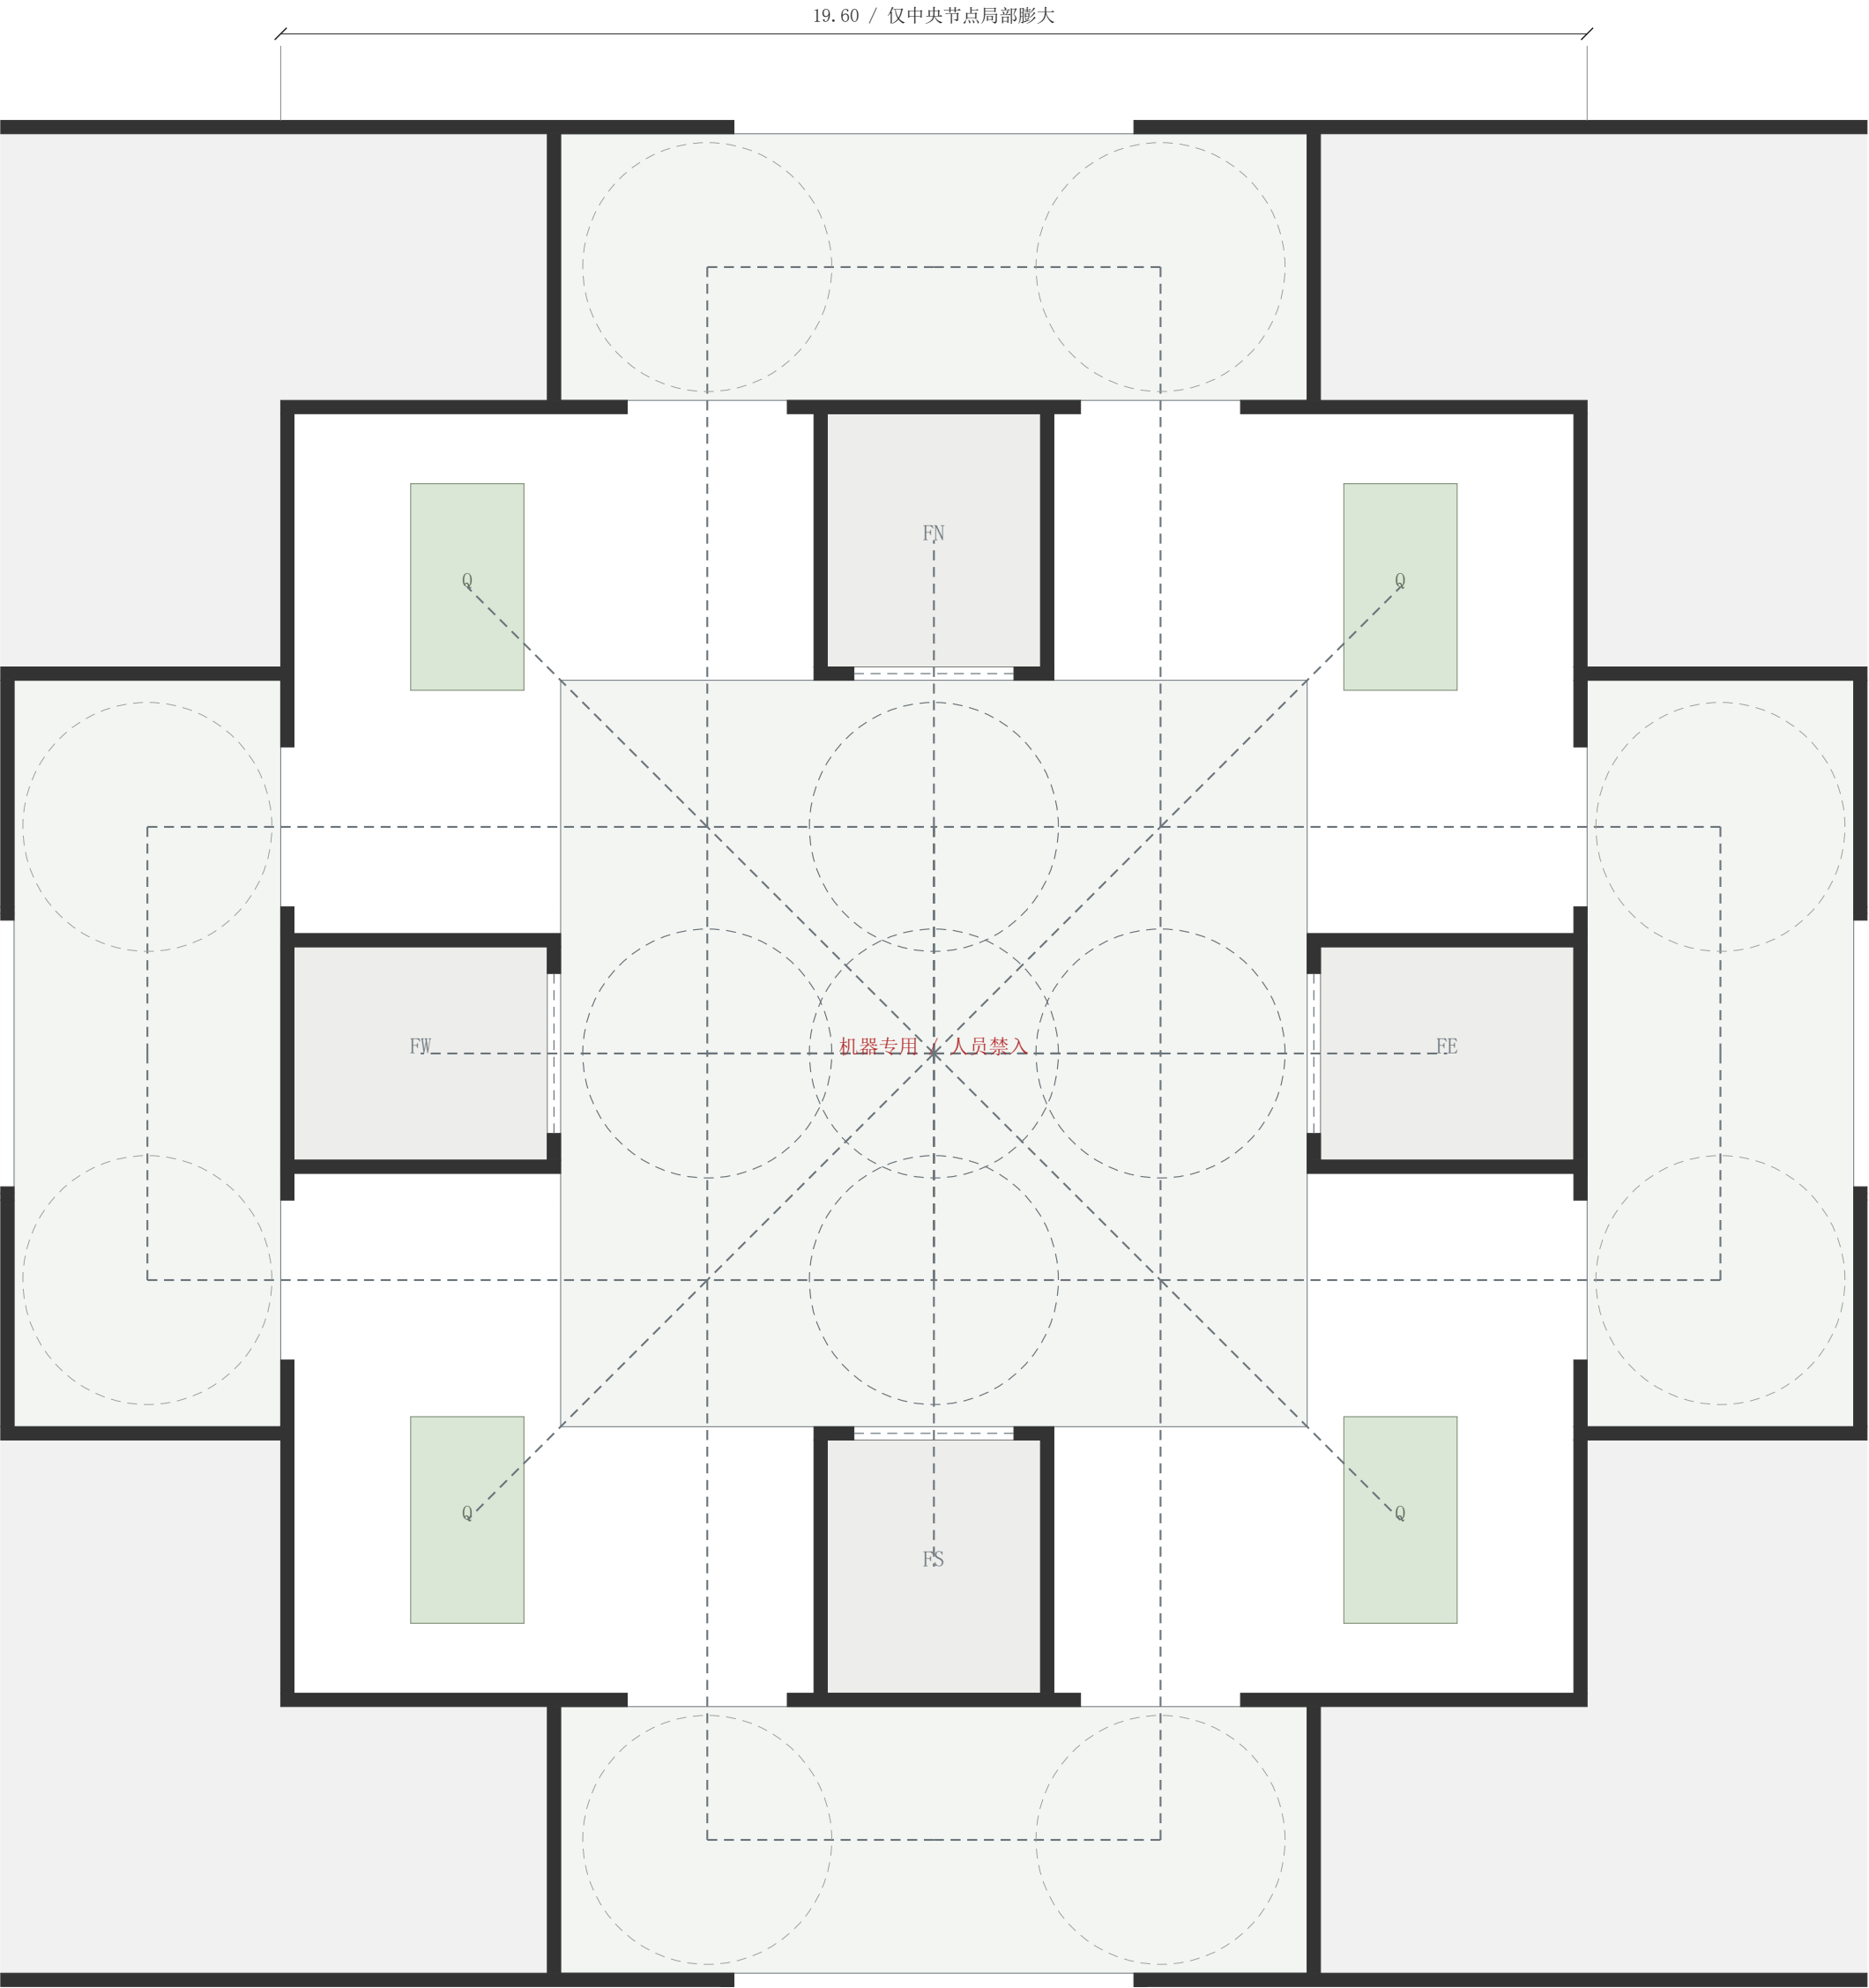

外接窄段净6/4；四梯净3.20×3.80、门2.40、八个绕行口净2.40。

Q四个整车等待位；回转圆03.736；逐台停梯后其余三梯可达。